



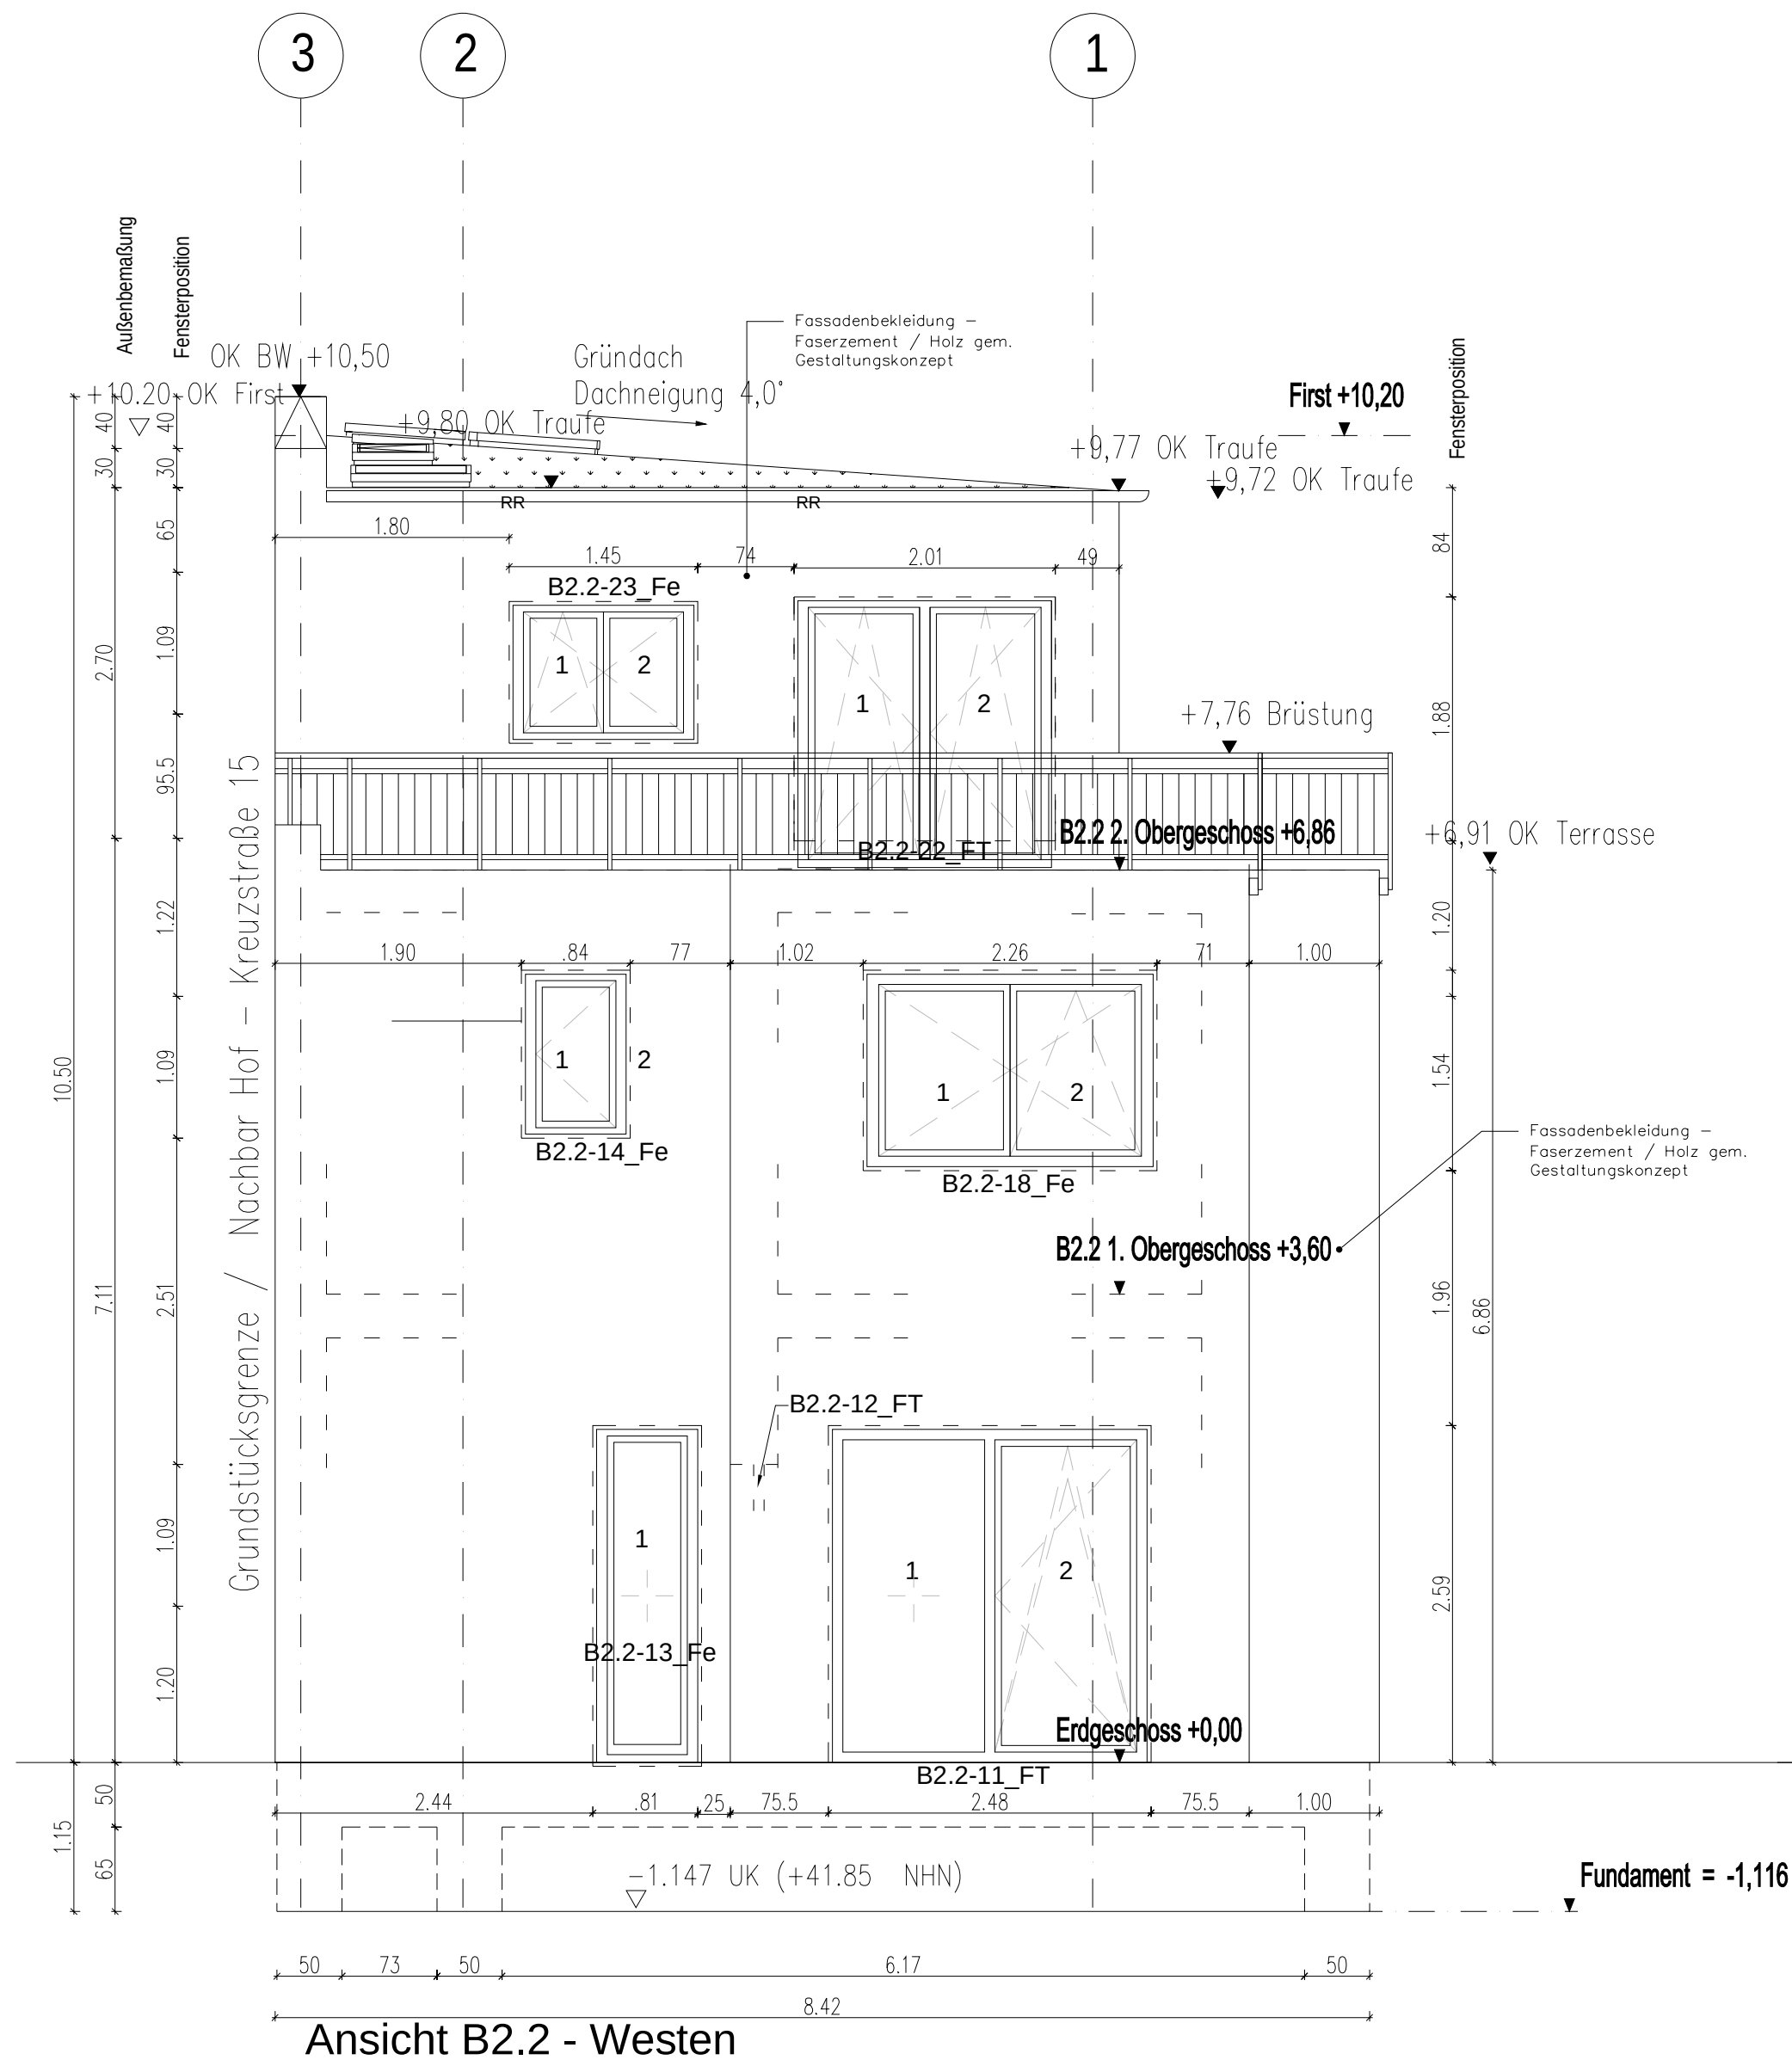

Ansicht B2.2 - Westen

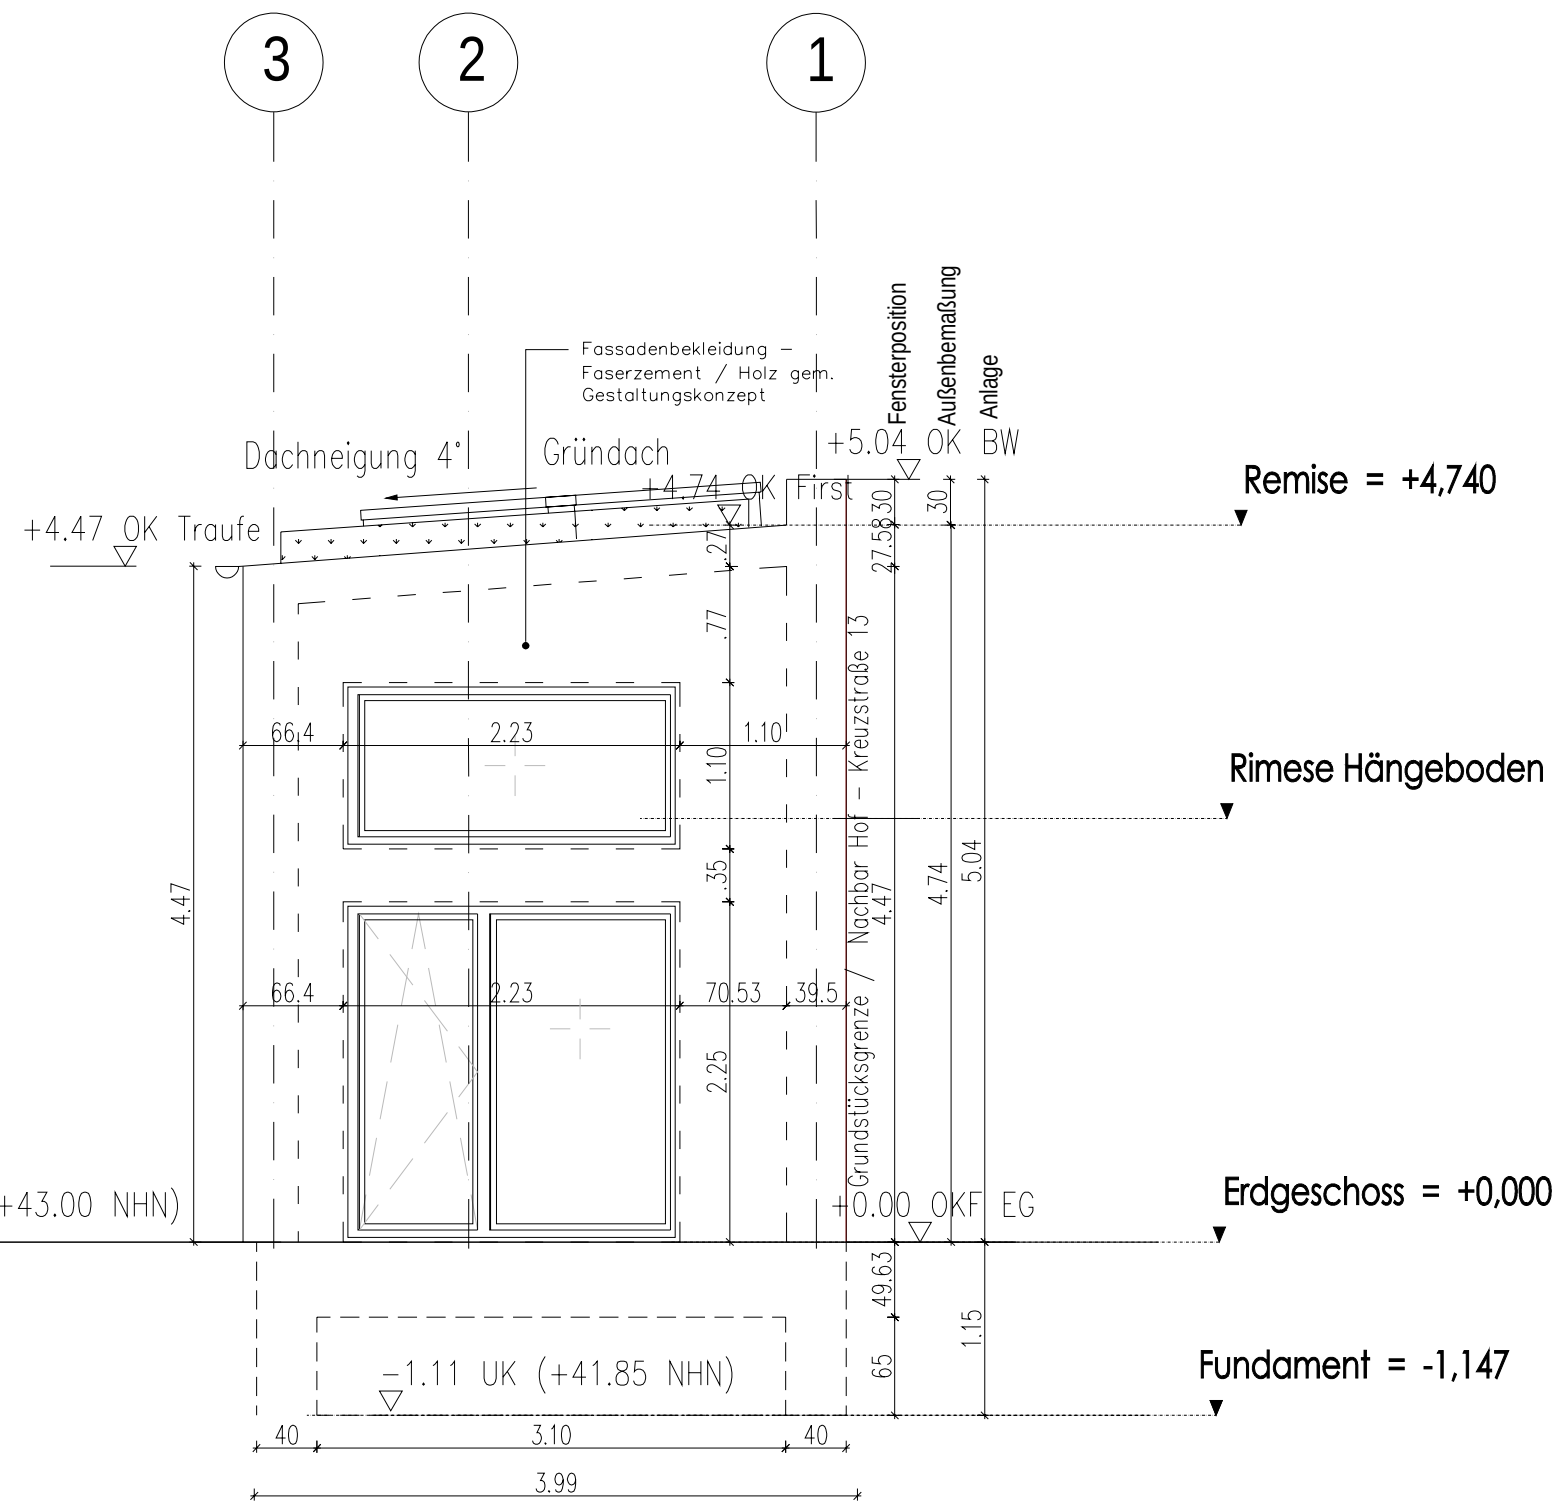

Ansicht B2.3 - Westen

LEGENDE

- AHD abgehängte Decke
- AN Ansicht
- AW Abwasser
- BDW Badewanne
- BRH Brüstungshöhe ab OKFF
- BW Brandwand
- BS Balkenschuh
- d dichtschlieend
- DB Deckenbalken
- DDF Dachdurchfhrung
- dstr dicht- und selbstschlieend
- EB Elastisch gebetteter Balken
- ELT Elektrounterverteilung
- FL Flche
- F30 Feuerwiderstandsfhigkeit 30min (feuerhemmend)
- F60 Feuerwiderstandsfhigkeit 60min (hochfeuerhemmend)
- F90 Feuerwiderstandsfhigkeit 90min (feuerbestndig)
- GR Grundriss
- H Hhe
- HK Heizkrper
- HKV Heizkreisverteiler
- HT Haustechnik
- IW Installationswand
- L Lftung
- OK Oberkante
- OKFFB Oberkante Fertigfuboden
- OKG Oberkante Gelnde
- OL Oberlicht
- RB Ringbalken
- RFR Regenfallrohr
- rs rauchdicht
- RR Regenrinne
- RA Rauchabzug
- RH Raumhoch
- RW Rettungsweg
- SN Schnitt
- T30 Tr feuerhemmend
- T30 rs Tr feuerhemmend, rauchdicht selbstschlie.
- T90 Tr feuerbestndig
- T90 rs Tr feuerbestndig, rauchdicht selbstschlie.
- TRH Traufhhe
- TW Trennwand
- UB unbewehrte Frostschrze
- UK Unterkante
- US Unterschnitt
- UZ Unterzug
- Z berzug
- VSS Vorsatzschale
- WE Wohneinheit
- Wfl Wohnflche
- wmB widerstandsfhig gegen mechanische Beanspruchung
- verdeckte Element Unterzug, Sparren, usw.
- Mauerwerk Bestand
- Dmmung
- Abriss Wand
- Mauerwerk Porenbeton
- Mauerwerk Kalksandstein
- Trockenbau-Innenwnde (innerhalb Wohneinheit), gem. Schallschutz und Brandschutz (Montage gem Herstellerangaben, z.B. Knauf W112 o.g.w.)
- uenwnde in Holztafelbauweise mit Faserzementtafeln oder Holz Verkleidung gem. Schallschutz und Brandschutz
- Stahlbeton
- Beton
- Brandschutzanforderungen
- Positionennummern, Angaben siehe Statik
- Positionennummern, Fenster / Tren
- Durchbruch

HINWEIS zur PLANUNG

Dieser Plan gilt nur in Verbindung mit den Ausfuhrungsdetails.
Fr alle Ausfuhrungs- bzw. Anschlussdetails siehe aktuellen
Detailplansatz. Fenster- und Trenlisten sind zu beachten.
Diese Planung gilt in Verbindung mit dem Ausstattungskatalog.


Die Anwendbarkeit der Detailzeichnung ist durch den
Verarbeiter vor Ort an Hand der tatschlichen Gegebenheiten zu
Prfen. Die Technischen Merkbltter der Hersteller und
Systemzulassungen sind zu beachten!

Alle Mae und Zeichnungsmae sind am Bau von der
auszufuhrenden Firma eigenverantwortlich zu prfen.
Der Ausfuhrende ist verpflichtet, den Auftraggeber auf etwaige
Unstimmigkeiten der Ausfuhrungsunterlagen hinzuweisen.
(VOB/B 3 nr. 3)

HINWEIS CAD-Zeichnung

Die Erstellung der vorliegenden Planungsunterlagen (GNEISE, basiert auf
der durch CAD KON und der Scherbeck Gruppe berggebenen
CAD-Zeichnung
Hhenangaben zu den jeweiligen Hausnummern sind dem amtlichen
Lageplan zu entnehmen. Die in den Schnitten dargestellte Hhe (x)
entspricht der im Lageplan zu entnehmende Hhenkote Gelnde /
OKFFBEG an Einzelaufgang.

Alle Mae sind am Bau zu prfen!

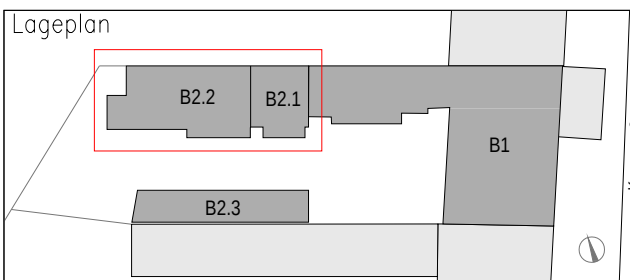

Bauherr

Albert Immo 4 S..r.l.
8d, rue Collart, 8414 Steinfort
Luxemburg

Bauvorhaben
**Dachgeschoss-Neubau (Bauteil 1) und
Neubau Seitenflgel-Erweiterung (Bauteil 2.1) /
Reihenhuser (Bauteil 2.2) / Remise (Bauteil 2.3)**

Kreuzstrae 14 in 13187 Berlin, Pankow

Architekten/Ingenieure
GNEISE
Planungs- und Beratungsgesellschaft

GNEISE
Dipl.-Ing. E.-R. Frevert-Henske
Planungs- und Beratungsgesellschaft mbH

Kiehlholzstrae 176, 12437 Berlin
Tel. 030 536 01-0
Fax 030 536 01-333

Planinhalt
Ausfuhrungsplanung
Ansicht Westen
Bauteile 2.1, 2.3 - Neubau
Kreuzstrae 14 in 13187 Berlin, Pankow

C	-	-	-
B	-	-	-
A	01.03.2022	AE	SF Erweiterung, Fensterhhen
Index	Datum	Gez	nderung

Datum:	Mastab:
30.11.2021	1:50
Bearbeitung:	Projektnummer:
AE	19049
Blattgre:	Zeichnungsnr.
830x297	KRE14_AP-19049-AN-B2.1.2-6.1

Plotted by Gneise Schutzvermerk nach DIN 34 beachten !

Vorabzug