


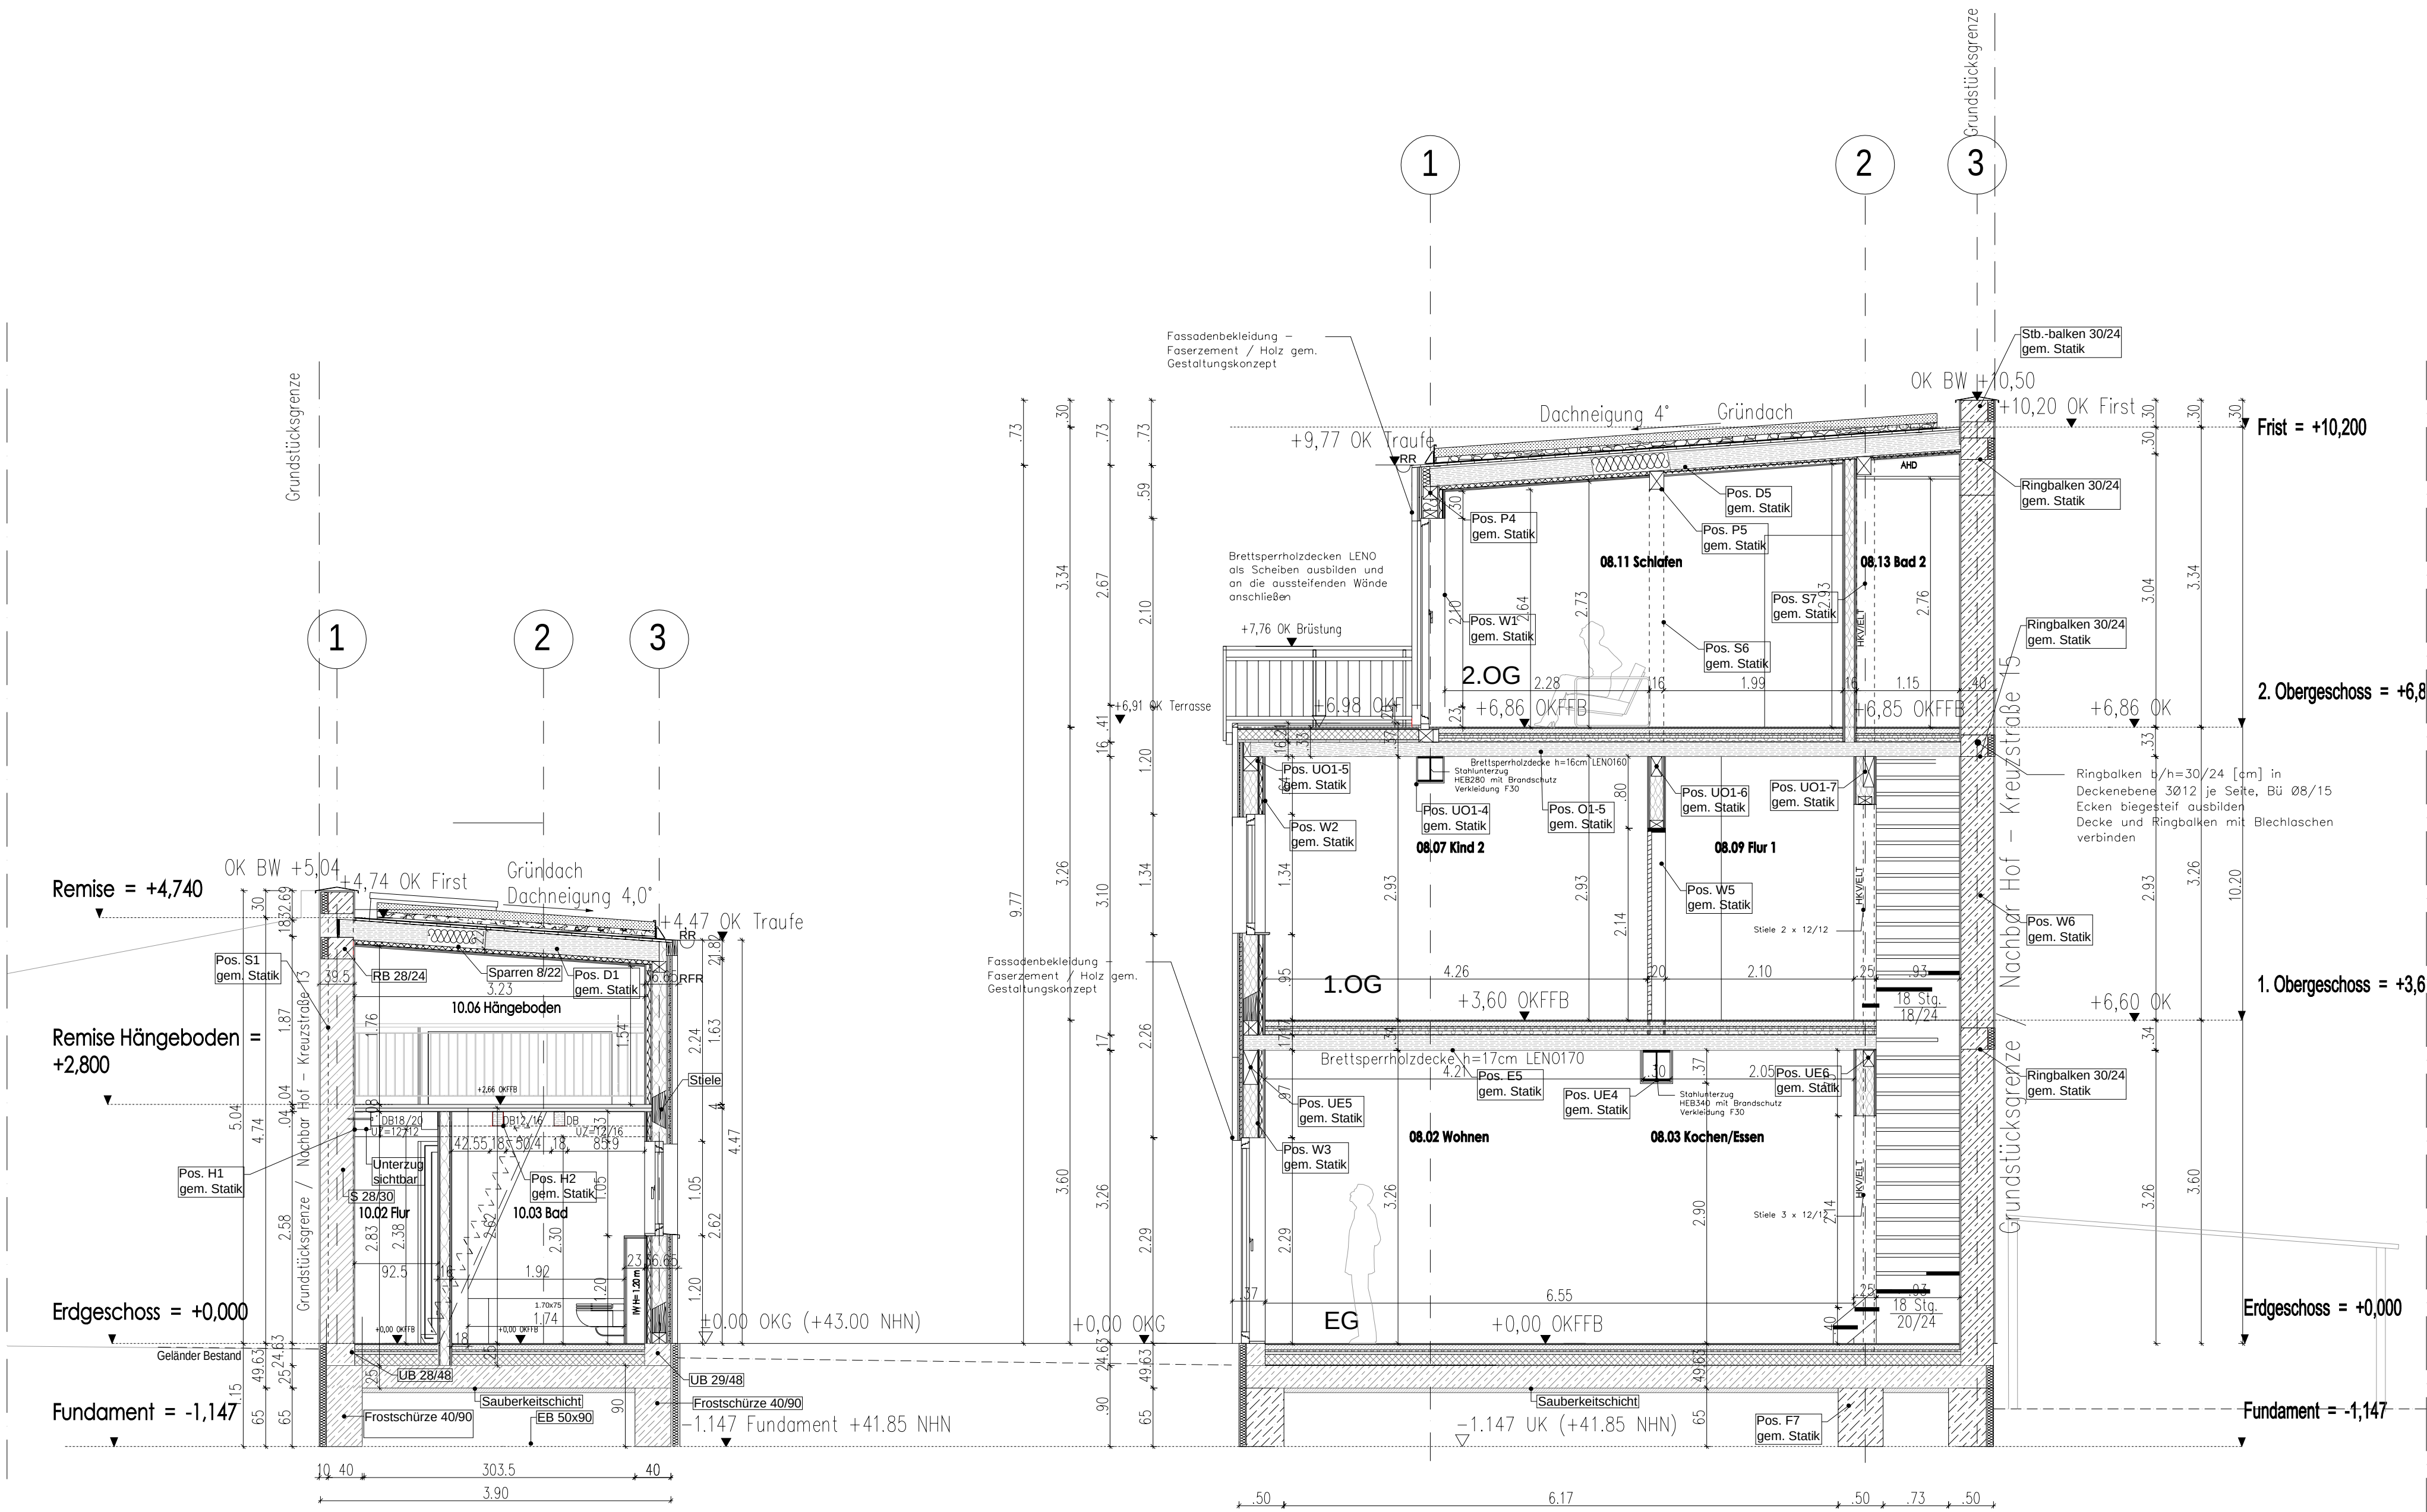

LEGENDE

AHD

abgehängte Decke

AN

Ansicht

AW

Abwasser

BDW

Badewanne

BRH

Brüstungshöhe ab OKFF

BW

Brandwand

BS

Balkenschuh

d

dichtschließend

DB

Deckenbalken

DDF

Dachdurchführung

dstür

dicht- und selbstschließend

EB

Elastisch gebetteter Balken

ELT

Elektrounterverteilung

FL

Fläche

F30

Feuerwiderstandsfähigkeit 30min (feuerhemmend)

F60

Feuerwiderstandsfähigkeit 60min (hochfeuerhemmend)

F90

Feuerwiderstandsfähigkeit 90min (feuerbeständig)

GR

Grundriss

H

Höhe

HK

Heizkörper

HKV

Heizkreisverteiler

HT

Haus Technik

IW

Installationswand

LÜ

Lüftung

OK

Oberkante

OKFFB

Oberkante Fertigfußboden

OKG

Oberkante Gelände

OL

Oberlicht

RB

Ringbalken

RFR

Regenfallrohr

rs

rauchdicht

RR

Regenrinne

RA

Rauchabzug

RH

Raumhoch

RW

Rettungsweg

SN

Schnitt

T30

Tür feuerhemmend

T30 rs

Tür feuerhemmend, rauchdicht selbstschließend

T90

Tür feuerbeständig

T90 rs

Tür feuerbeständig, rauchdicht selbstschließend

TRH

Traufhöhe

TW

Trennwand

UB

unbewehrte Frostschrünze

UK

Unterkante

US

Unterschnitt

UZ

Unterzug

ÜZ

Überzug

VSS

Vorsatzschale

WE

Wohneneinheit

Wfl

Wohnfläche

wmb

widerstandsfähig gegen mechanische Beanspruchung

verdeckte Element Unterzug, Sparren, usw.

Mauerwerk Bestand

Dämmung

Abriss Wand

Mauerwerk Porenbeton

Mauerwerk Kalksandstein

Trockenbau-Innenwände (innerhalb Wohneinheit), gem. Schallschutz und Brandschutz (Montage gemäß Herstellerangaben, z.B. Knauf W112 o.g.w.)

Außenwände in Holztafelbauweise mit Faserzementtafeln oder Holz Verkleidung gem. Schallschutz und Brandschutz

Stahlbeton

Beton

Brandschutzanforderungen

Positionennummern, Angaben siehe Statik

Positionennummern, Fenster / Türen

Durchbruch

C

-

-

-

B

-

-

-

A

01.03.2022

AE

SF Erweiterung, Fensterhöhen

Index

Datum

Gez

Änderung

Datum:

30.11.2021

Maßstab:

1:50

Bearbeitung:

AE

Projektnummer:

19049

Blattgröße:

830x297

Zeichnungs-nr.

KRE14_AP-19049-SN-B2.1.2-5.0

Plotted by

Gneise

Schutzvermerk nach DIN 34 beachten!

HINWEIS zur PLANUNG

Dieser Plan gilt nur in Verbindung mit den Ausführungsdetails

Für alle Ausführungs- bzw. Anschlussdetails siehe aktuellen Detailplansatz Fenster- und Türenlisten sind zu beachten

Diese Planung gilt in Verbindung mit dem Ausstattungskatalog

Die Anwendbarkeit der Detailzeichnung ist durch den Verarbeiter vor Ort an Hand der tatsächlichen Gegebenheiten zu Prüfen

Die Technischen Merkblätter der Hersteller und Systemzulassungen sind zu beachten!

Alle Maße und Zeichnungsmaße sind am Bau von der auszuführenden Firma eigenverantwortlich zu prüfen

Der Ausführende ist verpflichtet, den Auftraggeber auf etwaige Unstimmigkeiten der Ausführungsunterlagen hinzuweisen (VOB/B §3 nr.3)

HINWEIS CAD-Zeichnung

Die Erstellung der vorliegenden Planungsunterlage GNEISE, basiert auf der durch CAD KON und der Scherbeck Gruppe übergebenen CAD-Zeichnung

Höhenangaben zu den jeweiligen Hausnummern sind dem amtlichen Lageplan zu entnehmen

Die in den Schnitten dargestellte Höhe (x) entspricht der im Lageplan zu entnehmende Höhenkote Gelände / OKFFBEG am Einzelaufgang

Alle Maße sind am Bau zu prüfen!

Lageplan

Bauherr

Albert Immo 4 S.ö.r.l.

8d, rue Collart, 8414 Steinfort

Luxemburg

Bauvorhaben

Dachgeschoss-Neubau (Bauteil 1) und

Neubau Seitenflügel-Erweiterung (Bauteil 2.1) /

Reihenhäuser (Bauteil 2.2) / Remise (Bauteil 2.3)

Kreuzstraße 14 in 13187 Berlin, Pankow

Architekten/Ingenieure

GNEISE

Planungs- und Beratungsgesellschaft

GNEISE

Dipl.-Ing. E.-R. Frevert-Henske

Planungs- und Beratungsgesellschaft mbH

Kiehlholzstraße 176, 12437 Berlin

Tel. 030 536 01-0

Fax 030 536 01-333

Planinhalt

Ausführungsplanung

Schnitt C-C

Bauteile 2.1, 2.2 + B2.3 Neubau

Kreuzstraße 14 in 13187 Berlin, Pankow

C

-

-

-

B

-

-

-

A

01.03.2022

AE

SF Erweiterung, Fensterhöhen

Index

Datum

Gez

Änderung

Datum:

30.11.2021

Maßstab:

1:50

Bearbeitung:

AE

Projektnummer:

19049

Blattgröße:

830x297

Zeichnungs-nr.

KRE14_AP-19049-SN-B2.1.2-5.0

Plotted by

Gneise

Schutzvermerk nach DIN 34 beachten!

Diese Zeichnung ist urheberrechtlich geschützt. Bei Weitergabe -auch auszugsweise- ist die Gneise Planungs- und Beratungsgesellschaft mbH als Urheber auf dem Plan zu vermerken!