


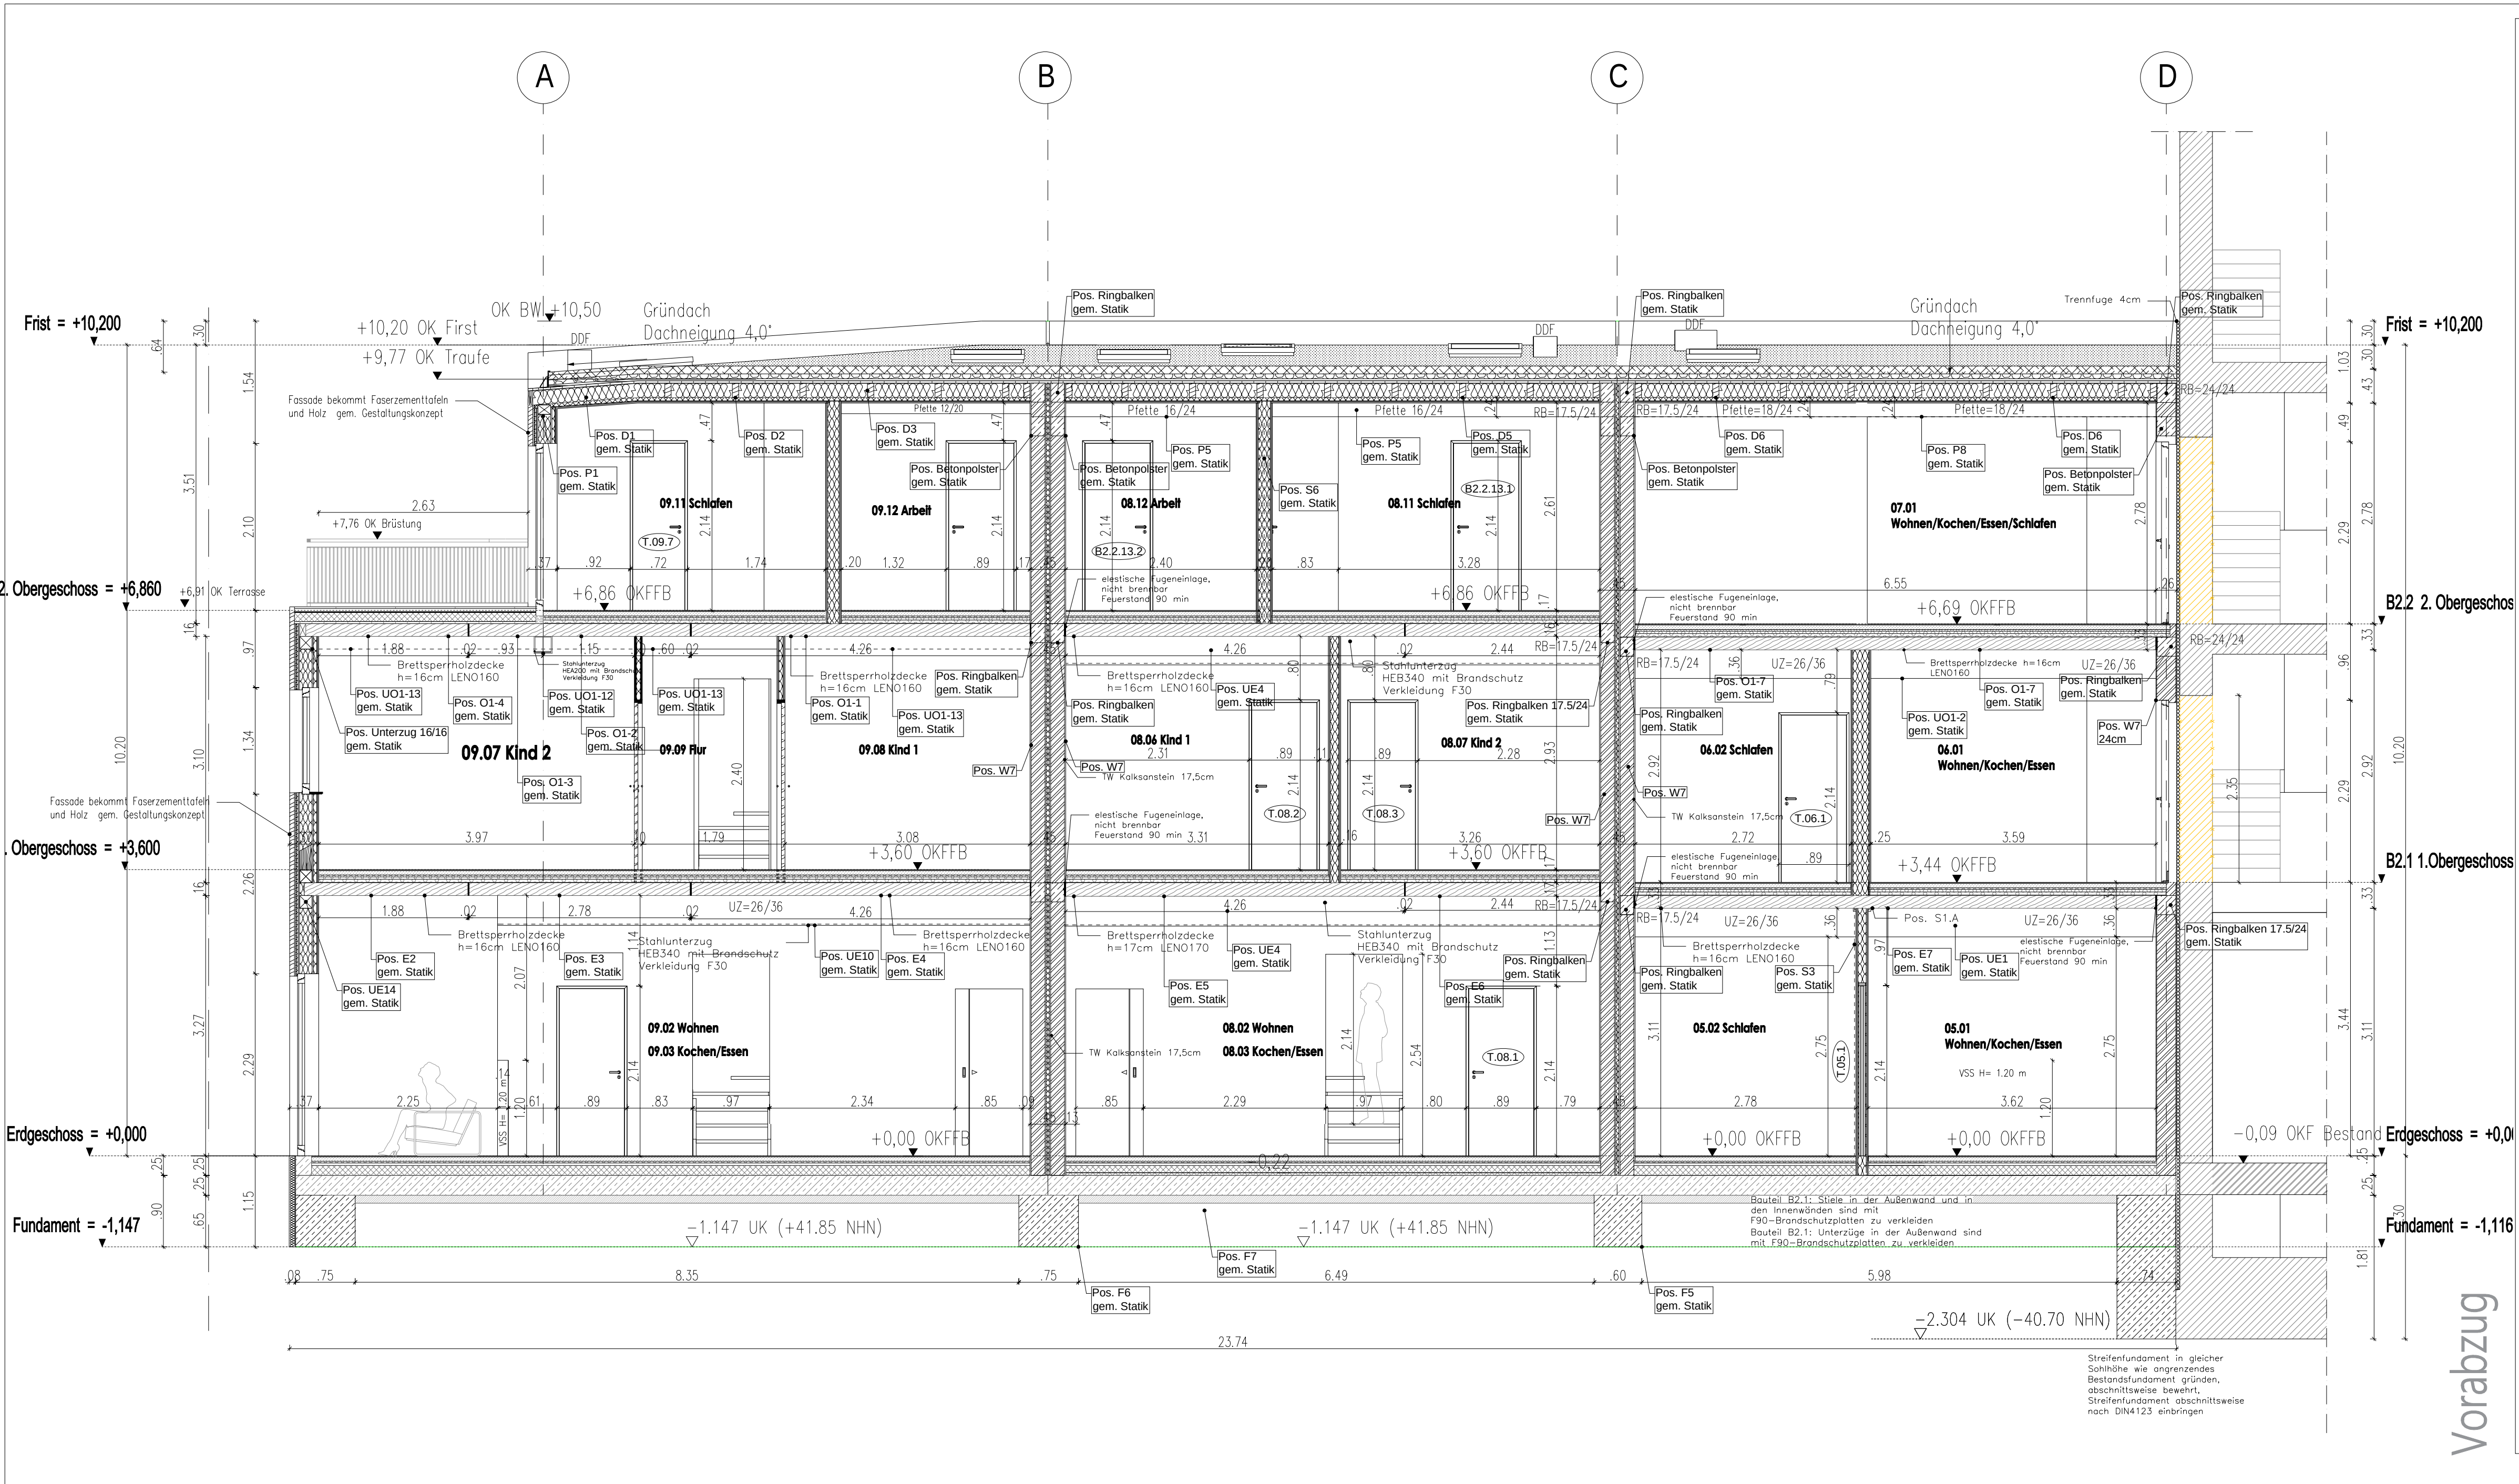

LEGENDE

AHD abgehängte Decke
AN Ansicht
AW Abwasser
BDW Badewanne
BRH Brüstungshöhe ab OKFF
BW Brandwand
BS Balkenschuh
d dichtschießend
DB Deckenbalken
DDF Dachdurchführung
dstür dicht- und selbstschließend
EB Elastisch gebetteter Balken
ELT Elektroverteilung
FL Fläche
F30 Feuerwiderstandsfähigkeit 30min (feuerhemmend)
F60 Feuerwiderstandsfähigkeit 60min (hochfeuerhemmend)
F90 Feuerwiderstandsfähigkeit 90min (feuerbeständig)
GR Grundriss
H Höhe
HK Heizkörper
HKV Heizkreisverteiler
HT Haustechnik
IW Installationswand
LÜ Lüftung
OK Oberkante
OKFFB Oberkante Fertigfußboden
OKG Oberkante Gelände
OL Oberlicht
RB Ringbalken
RFR Regenfallrohr
rs rauchdicht
RR Regenrinne
RA Rauchabzug
RH Raumhoch
RW Rettungsweg
SN Schnitt
T30 Tür feuerhemmend
T30 rs Tür feuerhemmend, rauchdicht selbstschließend
T90 Tür feuerbeständig
T90 rs Tür feuerbeständig, rauchdicht selbstschließend
TRH Traufhöhe
TW Trennwand
UB unbewehrte Frostschränke
UK Unterkante
US Unterschnitt
UZ Unterzug
ÜZ Überzug
VSS Vorsatzschale
WE Wohneinheit
Wfl Wohnfläche
wmb widerstandsfähig gegen mechanische Beanspruchung

verdeckte Element Unterzug, Sparren, usw.
Mauerwerk Bestand
Dämmung
Abriss Wand
Mauerwerk Porenbeton
Mauerwerk Kalksandstein
Trockenbau-Innenwände (innerhalb Wohneinheit), gem. Schallschutz und Brandschutz (Montage gemäß Herstellerangaben, z.B. Knauf W112 o.g.w.)
Außenwände in Holztafelbauweise mit Faserzementtafeln oder Holz Verkleidung gem. Schallschutz und Brandschutz

Stahlbeton
Beton
T30 rs Brandschutzanforderungen
Pos 01-1 Positionsnr., Angaben siehe Statik
B3.1-18.1 Positionsnr., Fenster / Türen
Durchbruch

HINWEIS zur PLANUNG

Dieser Plan gilt nur in Verbindung mit den Ausführungsdetails.
Für alle Ausführungs- bzw. Anschlussdetails siehe aktuellen Detailplansatz Fenster- und Türenlisten sind zu beachten.
Diese Planung gilt in Verbindung mit dem Ausstattungskatalog.

Die Anwendbarkeit der Detailzeichnung ist durch den Verarbeiter vor Ort an Hand der tatsächlichen Gegebenheiten zu Prüfen.
Die Technischen Merkblätter der Hersteller und Systemzulassungen sind zu beachten!

Alle Maße und Zeichnungsmaße sind am Bau von der auszuführenden Firma eigenverantwortlich zu prüfen.
Der Ausführende ist verpflichtet, den Auftraggeber auf etwaige Unstimmigkeiten der Ausführungsunterlagen hinzuweisen.
(VOB/B §3 nr.3)

HINWEIS CAD-Zeichnung

Die Erstellung der vorliegenden Planungsunterlagen (GNEISE, basiert auf der durch CAD KON und der Schenck Gruppe übergebenen CAD-Zeichnung.
Höhenangaben zu den jeweiligen Hausnummern sind dem amtlichen Lageplan zu entnehmen. Die in den Schnitten dargestellte Höhe (x) entspricht der im Lageplan zu entnehmende Höhenkote Gelände / OKFFB EG an Einzelaufgang.

Alle Maße sind am Bau zu prüfen!

Lageplan

Bauherr

Albert Immo 4 S.ä.r.l.
8d, rue Collart, 8414 Steinfort
Luxemburg

Bauvorhaben

**Dachgeschoss-Neubau (Bauteil 1) und
Neubau Seitenflügel-Erweiterung (Bauteil 2.1) /
Reihenhäuser (Bauteil 2.2) / Remise (Bauteil 2.3)**

Kreuzstraße 14 in 13187 Berlin, Pankow

Architekten/Ingenieure

GNEISE
Planungs- und Beratungsgesellschaft

GNEISE
Dipl.-Ing. E.-R. Frevert-Henske
Planungs- und Beratungsgesellschaft mbH

Kiehlholzstraße 176, 12437 Berlin
Tel. 030 536 01-0
Fax 030 536 01-333

Planinhalt

Ausführungsplanung

Schnitt D-D

Bauteile 2.1, 2.2 + B2.3 Neubau

Kreuzstraße 14 in 13187 Berlin, Pankow

Index	Datum	Gez	Änderung
C	-	-	-
B	-	-	-
A	01.03.2022	AE	SF Erweiterung, Fensterhöhen

Datum:	Maßstab:
30.11.2021	1:50

Bearbeitung:	Projektnummer:
AE	19049

Blattgröße:	Zeichnungsnr.
830x297	KRE14_AP-19049-SN-B2.1.2-5.1

Plotted by Gneise
Schutzvermerk nach DIN 34 beachten!