

Zeichnungsliste 50tel

AUSFÜHRUNGSPLANUNG

VORABZUG

**Bauteil 2.1,
2.2**

Stand:

01.03.2022

INDEX:

A

Bauvorhaben:


**Dachgeschoss-Neubau (Bauteil 1) und
Neubau Seitenflügel-Erweiterung (Bauteil 2.1) /
Reihenhäuser (Bauteil 2.2) / Remise (Bauteil 2.3)**

Kreuzstraße 14
13187 Berlin

Bauherr:

Albert Immo 4 S.à.r.l.
8d, Rue Collart
8414 Steinfort
Luxemburg

Zeichnungs-Nr.	Inhalt	Maßstab	Datum	Index
Ansichten				
LP5 19049 KRE14_AP-19049-GR-B2.1B2.2-6.0	Ansicht Süden	1:50	01.03.2022	A
LP5 19049 KRE14_AP-19049-GR-B2.1B2.2-6.1	Ansicht Westen	1:50	01.03.2022	A
LP5 19049 KRE14_AP-19049-DA-B2.1B2.2-1.0	Dachaufsicht	1:50	01.03.2022	A
Grundrisse				
LP5 19049 KRE14_AP-19049-GR-B2.1B2.2-4.0	Erdgeschoss	1:50	01.03.2022	A
LP5 19049 KRE14_AP-19049-GR-B2.1B2.2-4.1	1. Obergeschoss	1:50	01.03.2022	A
LP5 19049 KRE14_AP-19049-GR-B2.1B2.2-4.2	2. Obergeschoss	1:50	01.03.2022	A
LP5 19049 KRE14_AP-19049-GR-B2.1B2.2-1.1	Gründung	1:50	01.03.2022	A
Schnitte				
LP5 19049 KRE14_AP-19049-GR-B2.1B2.2-5.0	Schnitt C	1:50	01.03.2022	A
LP5 19049 KRE14_AP-19049-GR-B2.1B2.2-5.1	Schnitt D	1:50	01.03.2022	A

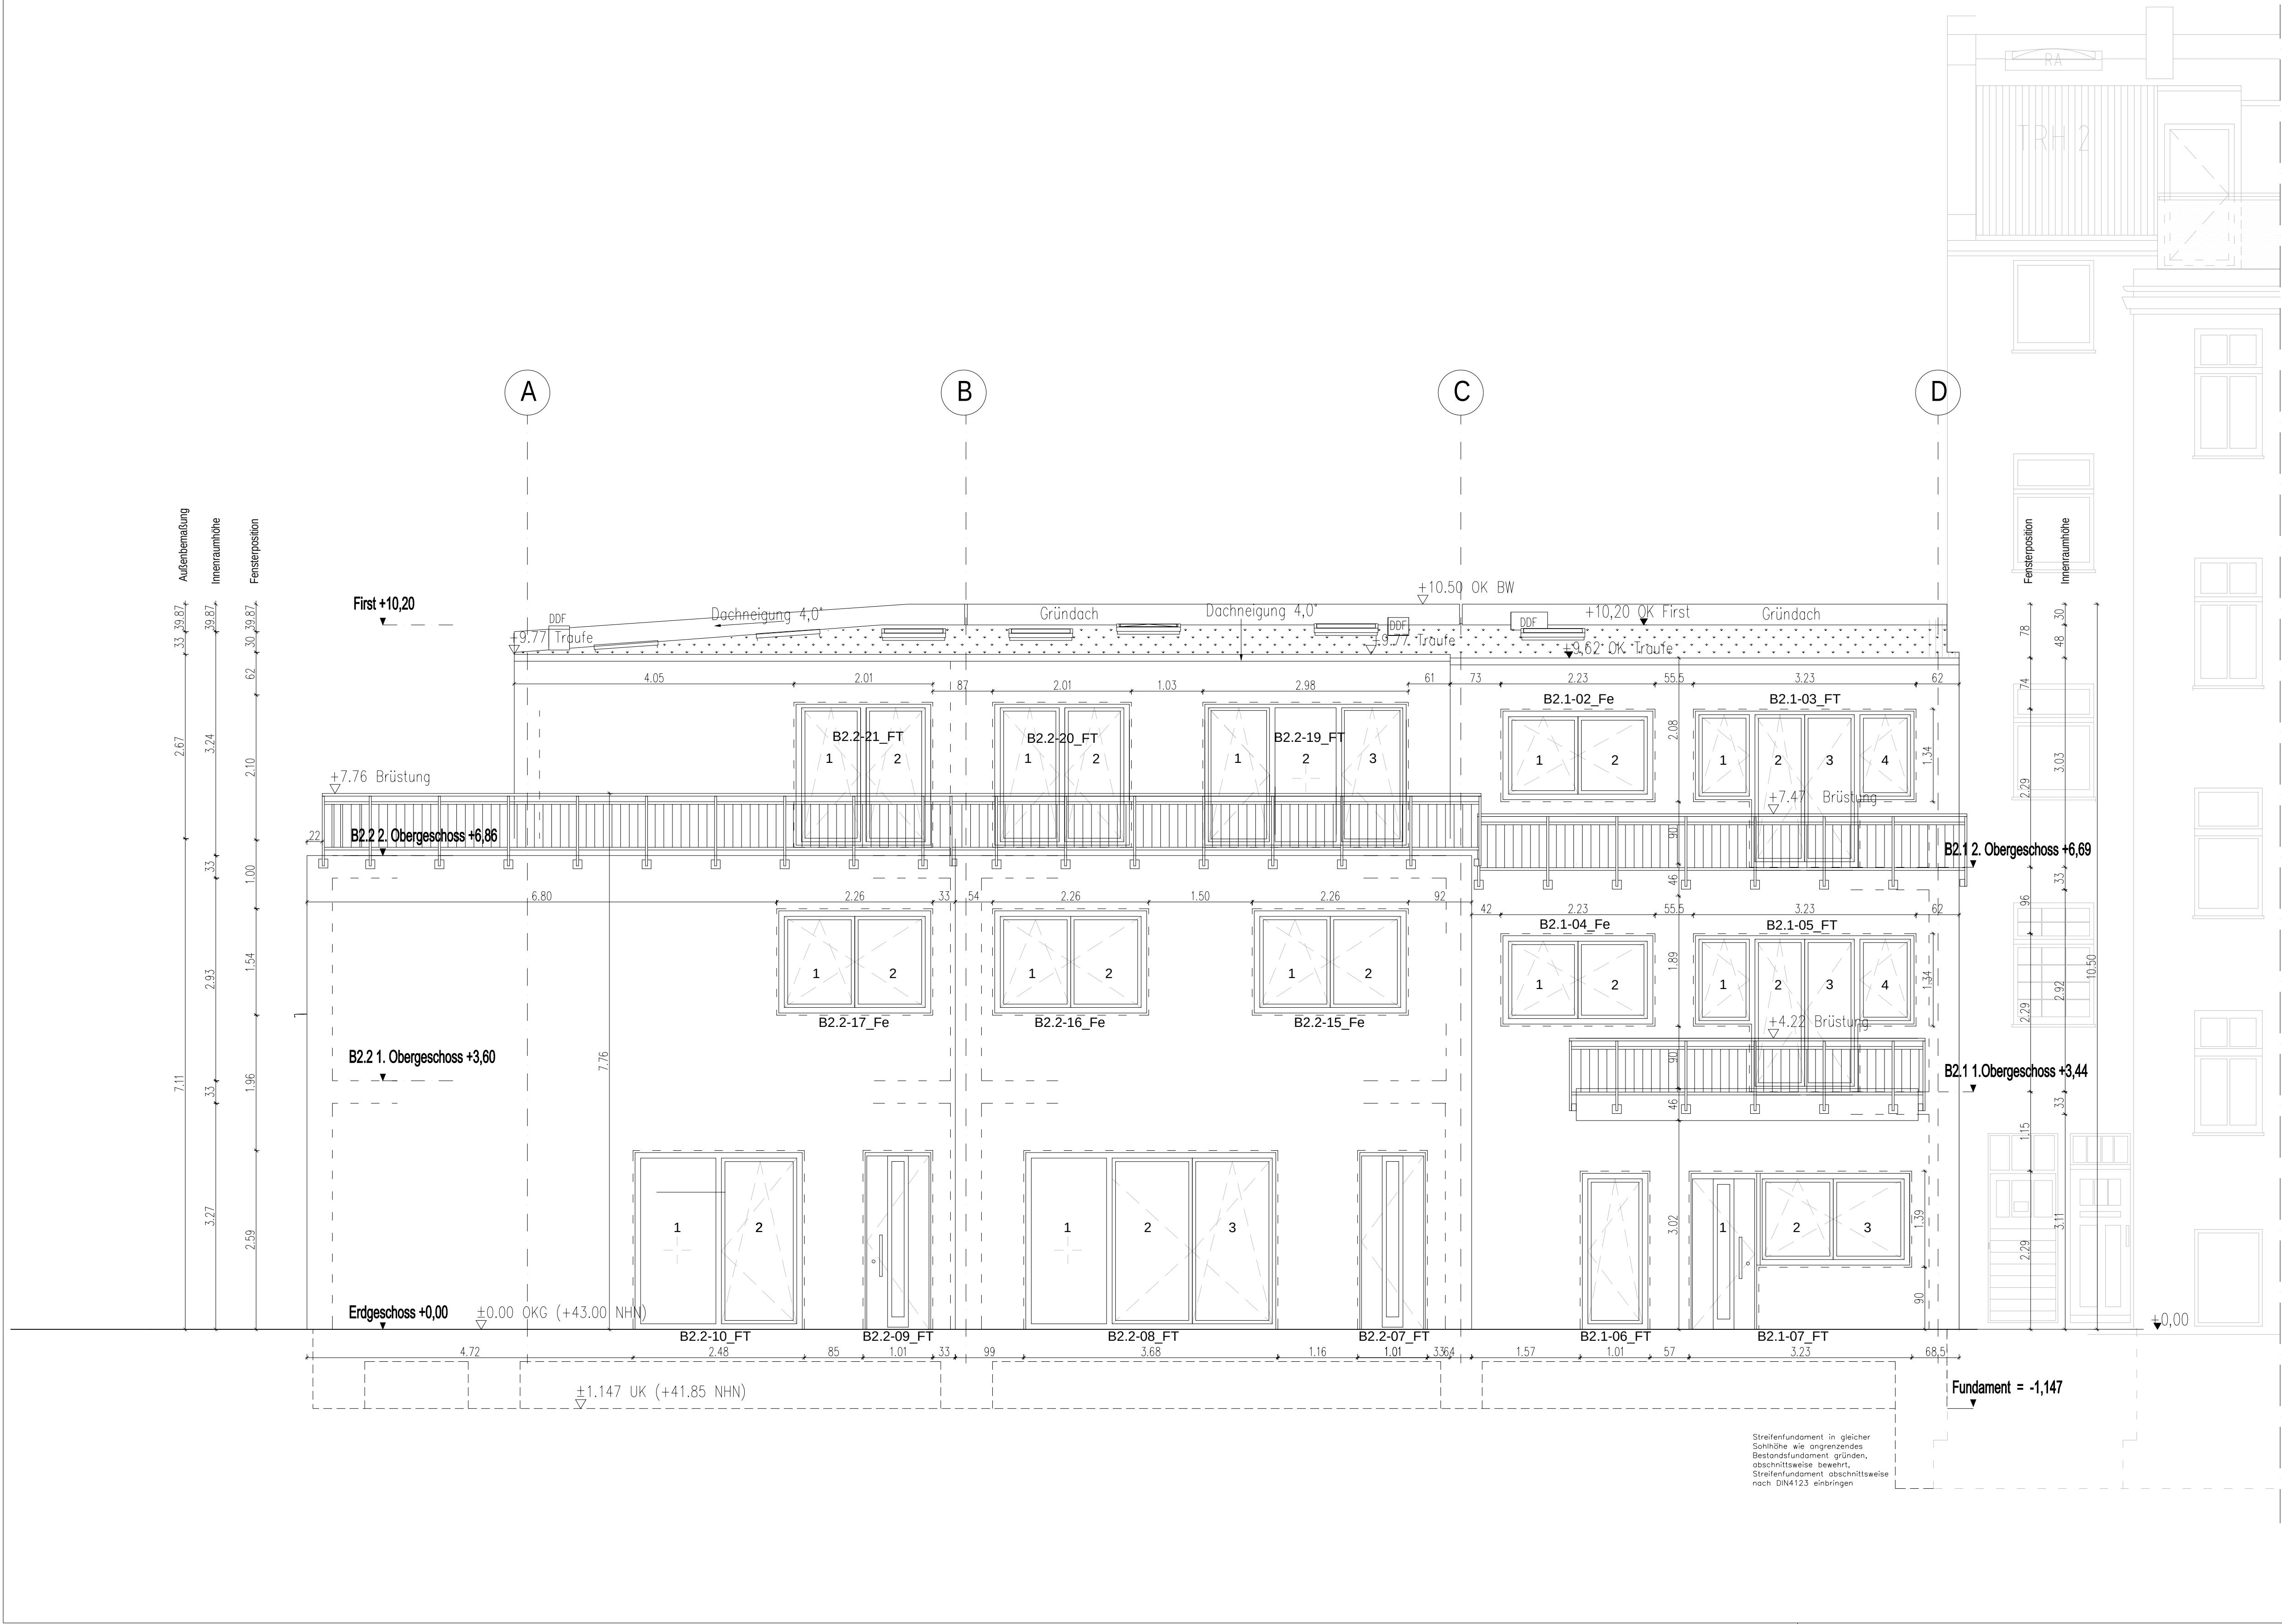

LEGENDE

- AHD abgehängte Decke
AN Ansicht
AW Abwasser
BDW Badewanne
BRH Brüstungshöhe ab OKFF
BW Brandwand
BS Balkenschuh
d dichtschießend
DB Deckenbalken
DDF Dachdurchführung
dstür dicht- und selbstschießend
EB Elastisch gebetteter Balken
ELT Elektrounterverteilung
FL Fläche
F30 Feuerwiderstandsfähigkeit 30min (feuerhemmend)
F60 Feuerwiderstandsfähigkeit 60min (hochfeuerhemmend)
F90 Feuerwiderstandsfähigkeit 90min (feuerbeständig)
GR Grundriss
H Höhe
HK Heizkörper
HKV Heizkreisverteiler
HT Haustechnik
IW Installationswand
LÜ Lüftung
OK Oberkante
OKFFB Oberkante Fertigfußboden
OKG Oberkante Gelände
OL Oberlicht
RB Ringbalken
RFR Regenfallrohr
rs rauchdicht
RR Regenrinne
RA Rauchabzug
RH Raumhoch
RW Rettungsweg
SN Schnitt
T30 Tür feuerhemmend
T30 rs Tür feuerhemmend, rauchdicht selbstschieß.
T90 Tür feuerbeständig
T90 rs Tür feuerbeständig, rauchdicht selbstschieß.
TRH Traufhöhe
TW Trennwand
UB unbewehrte Frostschürze
UK Unterkante
US Unterschnitt
UZ Unterzug
ÜZ Überzug
VSS Vorsatzschale
WE Wohneinheit
Wfl Wohnfläche
wmb widerstandsfähig gegen mechanische Beanspruchung
- verdeckte Element Unterzug, Sparren, usw.
Mauerwerk Bestand
Dämmung
Abriß Wand
Mauerwerk Porenbeton
Mauerwerk Kalksandstein
Trockenbau-Innenwände (innerhalb Wohneinheit), gem. Schallschutz und Brandschutz (Montage gemäß Herstellerangaben, z.B. Knauf W112 o.g.Ä.)
Außenwände in Holztafelbauweise mit Faserzementtafeln oder Holz Verkleidung gem. Schallschutz und Brandschutz
- Stahlbeton
Beton
T30/RS Brandschutzanforderungen
Pos 01-1 Positionsnr., Angaben siehe Statik
B2.1-01-1 Positionsnr., Fenster / Türen
Durchbruch

HINWEIS zur PLANUNG

Dieser Plan gilt nur in Verbindung mit den Ausführungsdetails.
Für alle Ausführungs- bzw. Anschlussdetails siehe aktuellen
Detailplansatz. Fenster- und Türenlisten sind zu beachten.
Diese Planung gilt in Verbindung mit dem Ausstattungskatalog.


Die Anwendbarkeit der Detailzeichnung ist durch den
Verarbeiter vor Ort an Hand der tatsächlichen Gegebenheiten zu
Prüfen. Die Technischen Merkblätter der Hersteller und
Systemzulassungen sind zu beachten!

Alle Maße und Zeichnungsmaße sind am Bau von der
auszuführenden Firma eigenverantwortlich zu prüfen.
Der Ausführende ist verpflichtet, den Auftraggeber auf etwaige
Unstimmigkeiten der Ausführungsunterlagen hinzuweisen.
(VOB/B §3 nr.3)

HINWEIS CAD-Zeichnung

Die Erstellung der vorliegenden Planungsunterlage GNEISE, basiert auf
der durch CAD KON und der Scherneck Gruppe übergebenen
CAD-Zeichnung.
Höhenangaben zu den jeweiligen Hausnummern sind dem amtlichen
Lageplan zu entnehmen. Die in den Schnitten dargestellte Höhe (w)
entspricht der im Lageplan zu entnehmende Höhenkote Gelände /
OKFFBEG am Einzelaufgang.

Alle Maße sind am Bau zu prüfen!

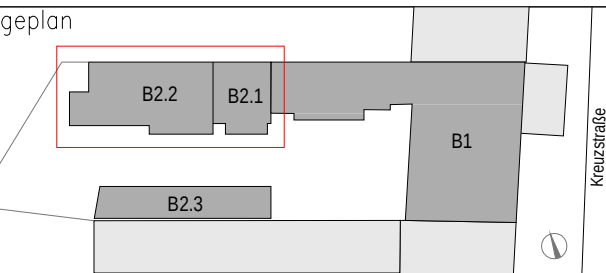

Bauherr

Albert Immo 4 S.ä.r.l.
8d, rue Collart, 8414 Steinfort
Luxemburg

Bauvorhaben
**Dachgeschoss-Neubau (Bauteil 1) und
Neubau Seitenflügel-Erweiterung (Bauteil 2.1) /
Reihenhäuser (Bauteil 2.2) / Remise (Bauteil 2.3)**

Kreuzstraße 14 in 13187 Berlin, Pankow



Architekten/Ingenieure
GNEISE
Planungs- und Beratungsgesellschaft

GNEISE
Dipl.-Ing. E.-R. Frevert-Henske
Planungs- und Beratungsgesellschaft mbH
Kiehlholzstraße 176, 12437 Berlin
Tel. 030 536 01-0
Fax 030 536 01-333

Planinhalt
**Ausführungsplanung
Ansicht Süden**
Bauteile 2.1, 2.2 - Neubau
Kreuzstraße 14 in 13187 Berlin, Pankow

C	-	-	-
B	-	-	-
A	01.03.2022	AE	SF Erweiterung, Fensterhöhen
Index	Datum	Gez	Änderung

Datum:	30.11.2021	Maßstab:	1:50
Bearbeitung:	AE	Projektnummer:	19049
Blattgröße:	940x450	Zeichnungsnr.	KRE14_AP-19049-AN-B2.1.2-6.0
Plotted by:	Gneise	Schutzvermerk nach DIN 34 beachten!	

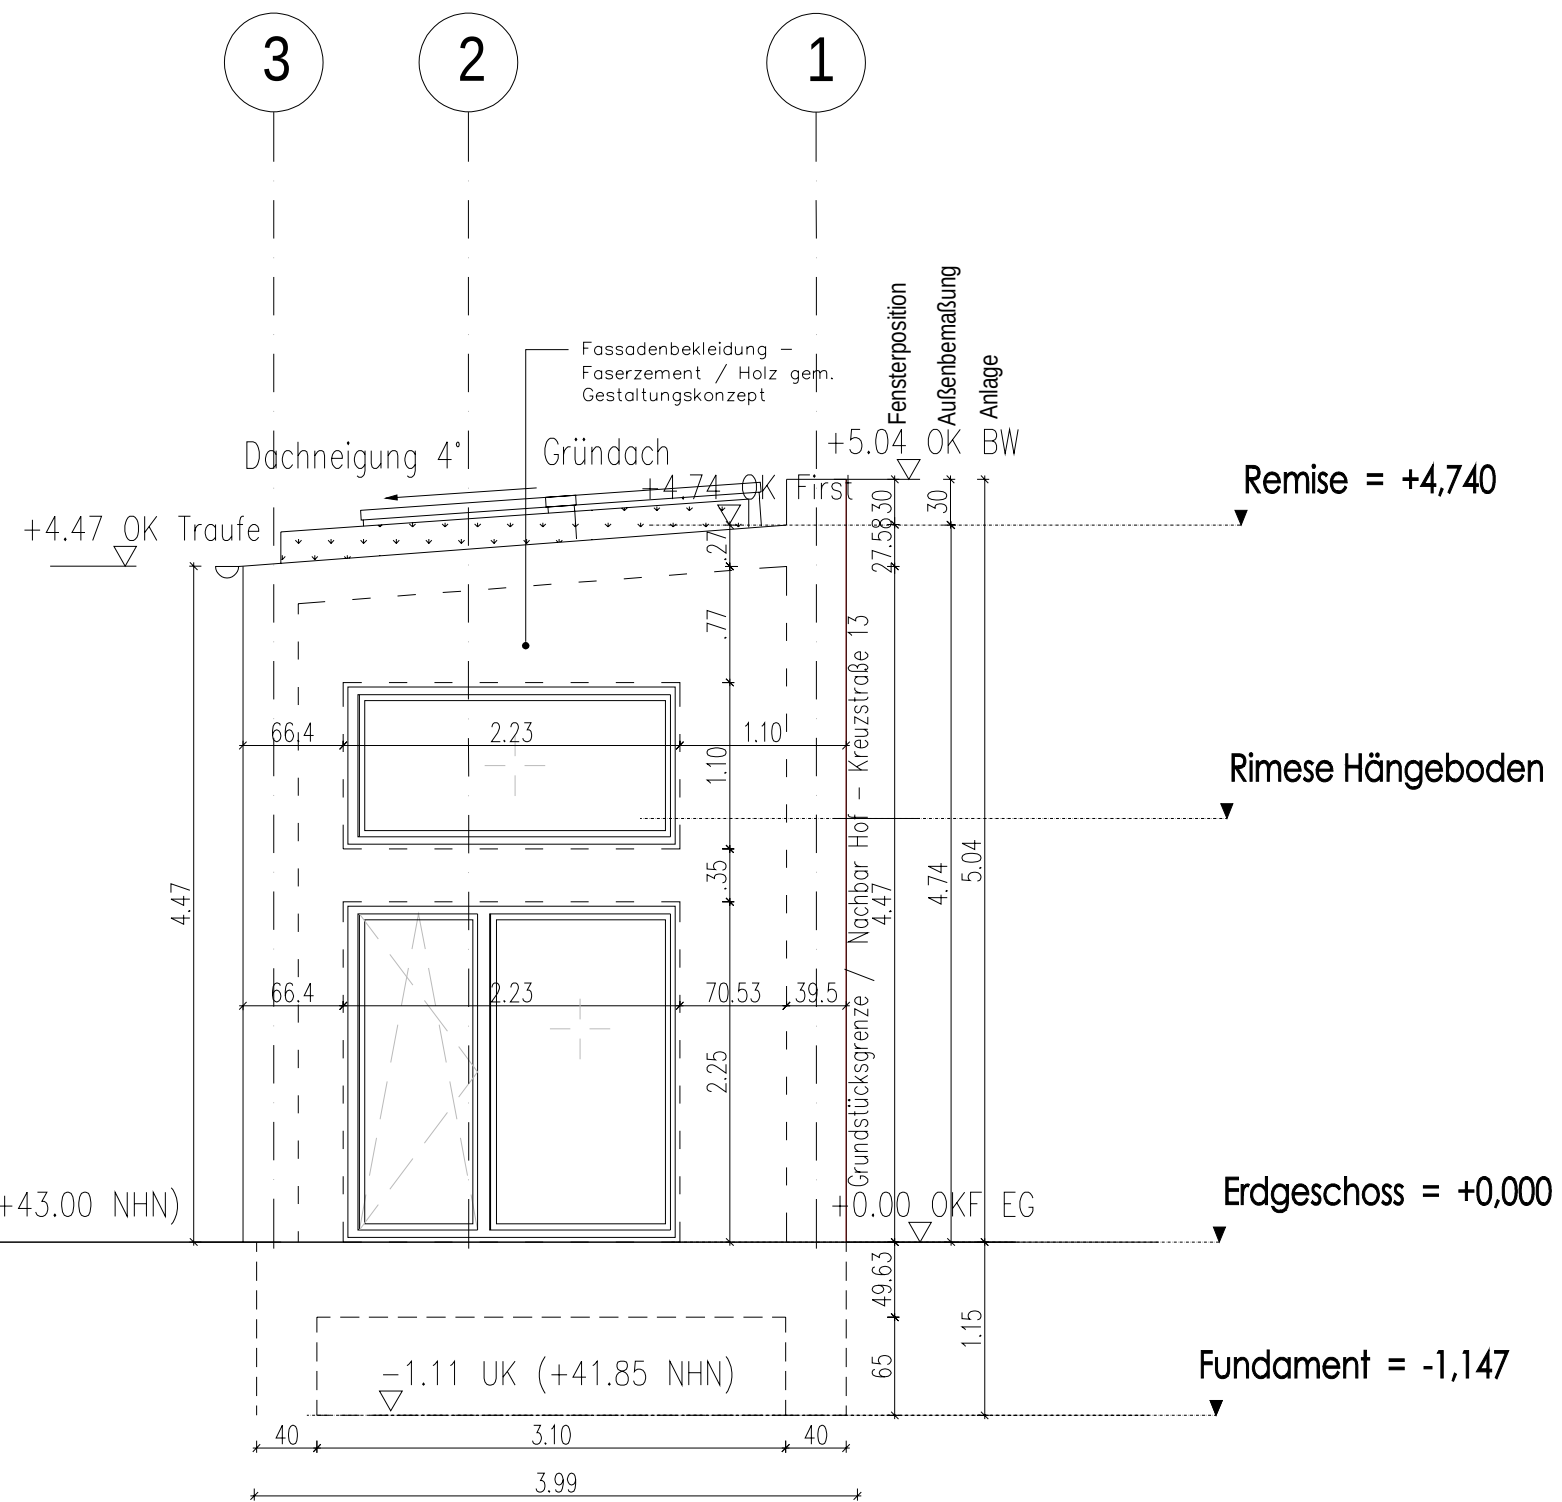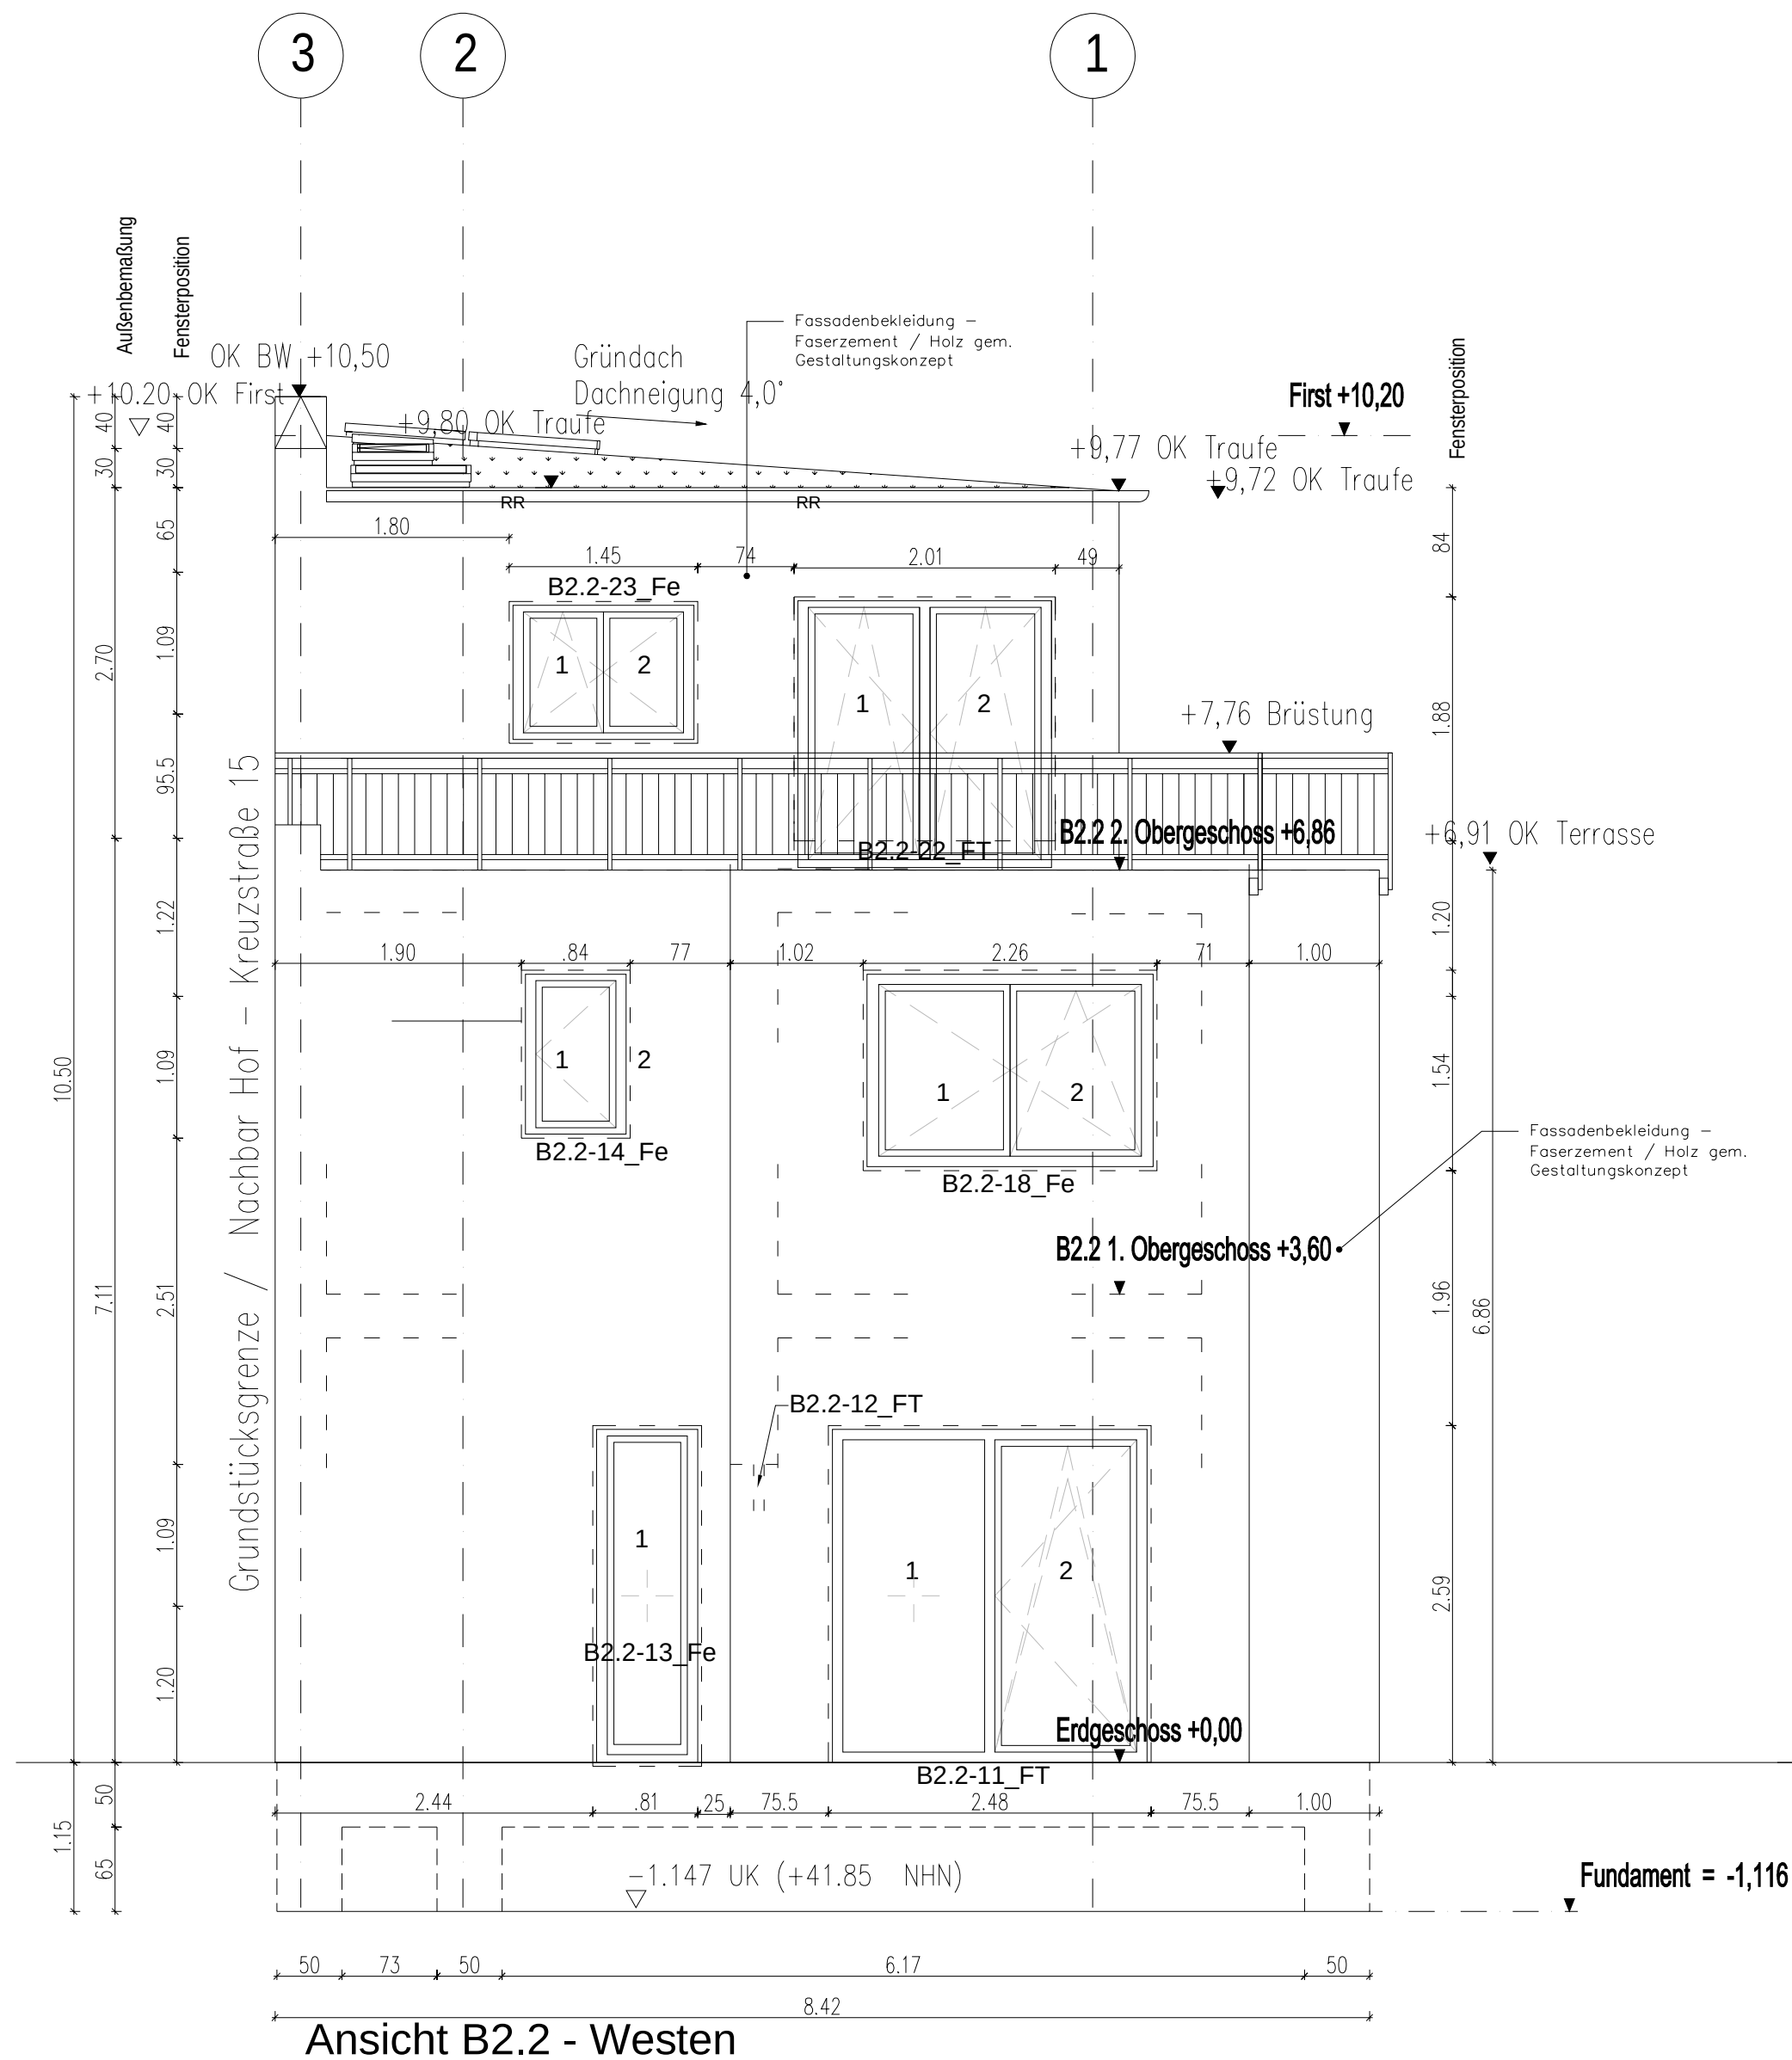

LEGENDE			
AHD	abgehängte Decke		
AN	Ansicht		
AW	Abwasser		
BDW	Badewanne		
BRH	Brüstungshöhe ab OKFF		
BW	Brandwand		
BS	Balkenschuh		
d	dichtschließend		
DB	Deckenbalken		
DDF	Dachdurchführung		
dstür	dicht- und selbstschließend		
EB	Elastisch gebetteter Balken		
ELT	Elektrounterverteilung		
FL	Fläche		
F30	Feuerwiderstandsfähigkeit 30min (feuerhemmend)		
F60	Feuerwiderstandsfähigkeit 60min (hochfeuerhemmend)		
F90	Feuerwiderstandsfähigkeit 90min (feuerbeständig)		
GR	Grundriss		
H	Höhe		
HK	Heizkörper		
HKV	Heizkreisverteiler		
HT	Haustechnik		
IW	Installationswand		
LÜ	Lüftung		
OK	Oberkante		
OKFFB	Oberkante Fertigfußboden		
OKG	Oberkante Gelände		
OL	Oberlicht		
RB	Ringbalken		
RFR	Regenfallrohr		
rs	rauchdicht		
RR	Regenrinne		
RA	Rauchabzug		
RH	Raumhoch		
RW	Rettungsweg		
SN	Schnitt		
T30	Tür feuerhemmend		
T30 rs	Tür feuerhemmend, rauchdicht selbstschließ.		
T90	Tür feuerbeständig		
T90 rs	Tür feuerbeständig, rauchdicht selbstschließ.		
TRH	Traufhöhe		
TW	Trennwand		
UB	unbewehrte Frostschräge		
UK	Unterkante		
US	Unterschnitt		
UZ	Unterzug		
ÜZ	Überzug		
VSS	Vorsatzschale		
WE	Wohninheit		
Wfl	Wohnfläche		
wmB	widerstandsfähig gegen mechanische Beanspruchung		
verdeckte Element	Unterzug, Sparren, usw.		
Mauerwerk Bestand			
Dämmung			
Abriss Wand			
Mauerwerk Porenbeton			
Mauerwerk Kalksandstein			
Trockenbau-Innenwände (innerhalb Wohneinheit), gem. Schallschutz und Brandschutz (Montage gemäß Herstellerangaben, z.B. Knauf W112 o.g.l.w.)			
Außenwände in Holztafelbauweise mit Faserzementtafeln oder Holz Verkleidung gem. Schallschutz und Brandschutz			
Stahlbeton			
Beton			
Brandschutzanforderungen			
Positionennummern, Angaben siehe Statik			
Positionennummern, Fenster / Türen			
Durchbruch			

HINWEIS zur PLANUNG

Dieser Plan gilt nur in Verbindung mit den Ausführungsdetails.
Für alle Ausführungs- bzw. Anschlussdetails siehe aktuellen
Detailplansatz. Fenster- und Türenlisten sind zu beachten.
Diese Planung gilt in Verbindung mit dem Ausstattungskatalog.

Die Anwendbarkeit der Detailzeichnung ist durch den
Verarbeiter vor Ort an Hand der tatsächlichen Gegebenheiten zu
Prüfen. Die Technischen Merkblätter der Hersteller und
Systemzulassungen sind zu beachten!

Alle Maße und Zeichnungsmaße sind am Bau von der
auszuführenden Firma eigenverantwortlich zu prüfen.
Der Ausführende ist verpflichtet, den Auftraggeber auf etwaige
Unstimmigkeiten der Ausführungsunterlagen hinzuweisen.
(VOB/B §3 nr.3)

HINWEIS CAD-Zeichnung

Die Erstellung der vorliegenden Planungsunterlagen (GNEISE, basiert auf
der durch CAD KON und der Schenbeck Gruppe übergebenen
CAD-Zeichnung
Hohenangaben zu den jeweiligen Hausnummern sind dem amtlichen
Lageplan zu entnehmen. Die in den Schnitten dargestellte Höhe (x)
entspricht der im Lageplan zu entnehmende Höhenkote Gelände /
OKFFBEG an Einzelaufgang.

Alle Maße sind am Bau zu prüfen!



Bauherr

Albert Immo 4 S.ä.r.l.
8d, rue Collart, 8414 Steinfort
Luxemburg

Bauvorhaben

**Dachgeschoss-Neubau (Bauteil 1) und
Neubau Seitenflügel-Erweiterung (Bauteil 2.1) /
Reihenhäuser (Bauteil 2.2) / Remise (Bauteil 2.3)**

Kreuzstraße 14 in 13187 Berlin, Pankow

Architekten/Ingenieure

**GNEISE**
Planungs- und Beratungsgesellschaft

GNEISE
Dipl.-Ing. E.-R. Frevert-Henske
Planungs- und Beratungsgesellschaft mbH

Kiehlholzstraße 176, 12437 Berlin
Tel. 030 536 01-0
Fax 030 536 01-333

Planinhalt

Ausführungsplanung
Ansicht Westen
Bauteile 2.1, 2.3 - Neubau
Kreuzstraße 14 in 13187 Berlin, Pankow

C	-	-	-
B	-	-	-
A	01.03.2022	AE	SF Erweiterung, Fensterhöhen
Index	Datum	Gez	Änderung

Datum:	30.11.2021	Maßstab:	1:50
Bearbeitung:	AE	Projektnummer:	19049
Blattgröße:	830x297	Zeichnungsnr.	KRE14_AP-19049-AN-B2.1.2-6.1
Plotted by Gneise		Schutzvermerk nach DIN 34 beachten!	



HINWEIS zur PLANUNG

Dieser Plan gilt nur in Verbindung mit den Ausführungsdetails. Für alle Ausführungs- bzw. Anschlussdetails siehe aktuellen Detailplansatz Fenster- und Türenlisten sind zu beachten. Diese Planung gilt in Verbindung mit dem Ausstattungskatalog.

Die Anwendbarkeit der Detailzeichnung ist durch den Verarbeiter vor Ort an Hand der tatsächlichen Gegebenheiten zu Prüfen. Die Technischen Merkblätter der Hersteller und Systemzulassungen sind zu beachten!

Alle Maße und Zeichnungsmaße sind am Bau von der auszuführenden Firma eigenverantwortlich zu prüfen. Der Ausführende ist verpflichtet, den Auftraggeber auf etwaige Unstimmigkeiten der Planungsunterlagen hinzuweisen. (VOB/B §3 nr.3)

HINWEIS CAD-Zeichnung

Die Erstellung der vorliegenden Zeichnungsunterlage GNEISE, basiert auf der durch CAD KON und der Schernbeck Gruppe übergebenen CAD-Zeichnung.

Höhenangaben zu den jeweiligen Hausnummern sind dem amtlichen Lageplan zu entnehmen. Die in den Schnitten dargestellte Höhe (x) entspricht der im Lageplan zu entnehmende Höhenkote Gelände / OK FFB EG am Einzelaufgang.

Alle Maße sind am Bau zu prüfen!

Lageplan

Kreuzstraße

Bauherr

Albert Immo 4 S.ä.r.l.

8d, rue Collart, 8414 Steinfurt

Luxemburg

Bauvorhaben

**Dachgeschoss-Neubau (Bauteil 1) und
Neubau Seitenflügel-Erweiterung (Bauteil 2.1) /
Reihenhäuser (Bauteil 2.2) / Remise (Bauteil 2.3)**

Kreuzstraße 14 in 13187 Berlin, Pankow

Architekten/Ingenieure

GNEISE
Planungs- und Beratungsgesellschaft

GNEISE
Dipl.-Ing. E.-R. Frevert-Henske
Planungs- und Beratungsgesellschaft mbH

Kiehlhofstraße 176, 12437 Berlin
Tel. 030 536 01-0
Fax 030 536 01-333

Planinhalt

Ausführungsplanung

Dachaufsicht

Bauteile 2.1, 2.2 - Neubau


Kreuzstraße 14 in 13187 Berlin, Pankow


C	-	-	-
B	-	-	-
A	01.03.2022	AE	SF Erweiterung, Fensterhöhen
Index	Datum	Gez	Änderung

Datum:	Maßstab:
30.11.2021	1:50
Bearbeitung:	Projektnummer:
AE	19049
Blattgröße:	Zeichnungsnr.
830x297	KRE14_AP-19049-DA-B2.1.2-1.0

Printed by Gneise

Schutzmerkmal nach DIN 34 beachten

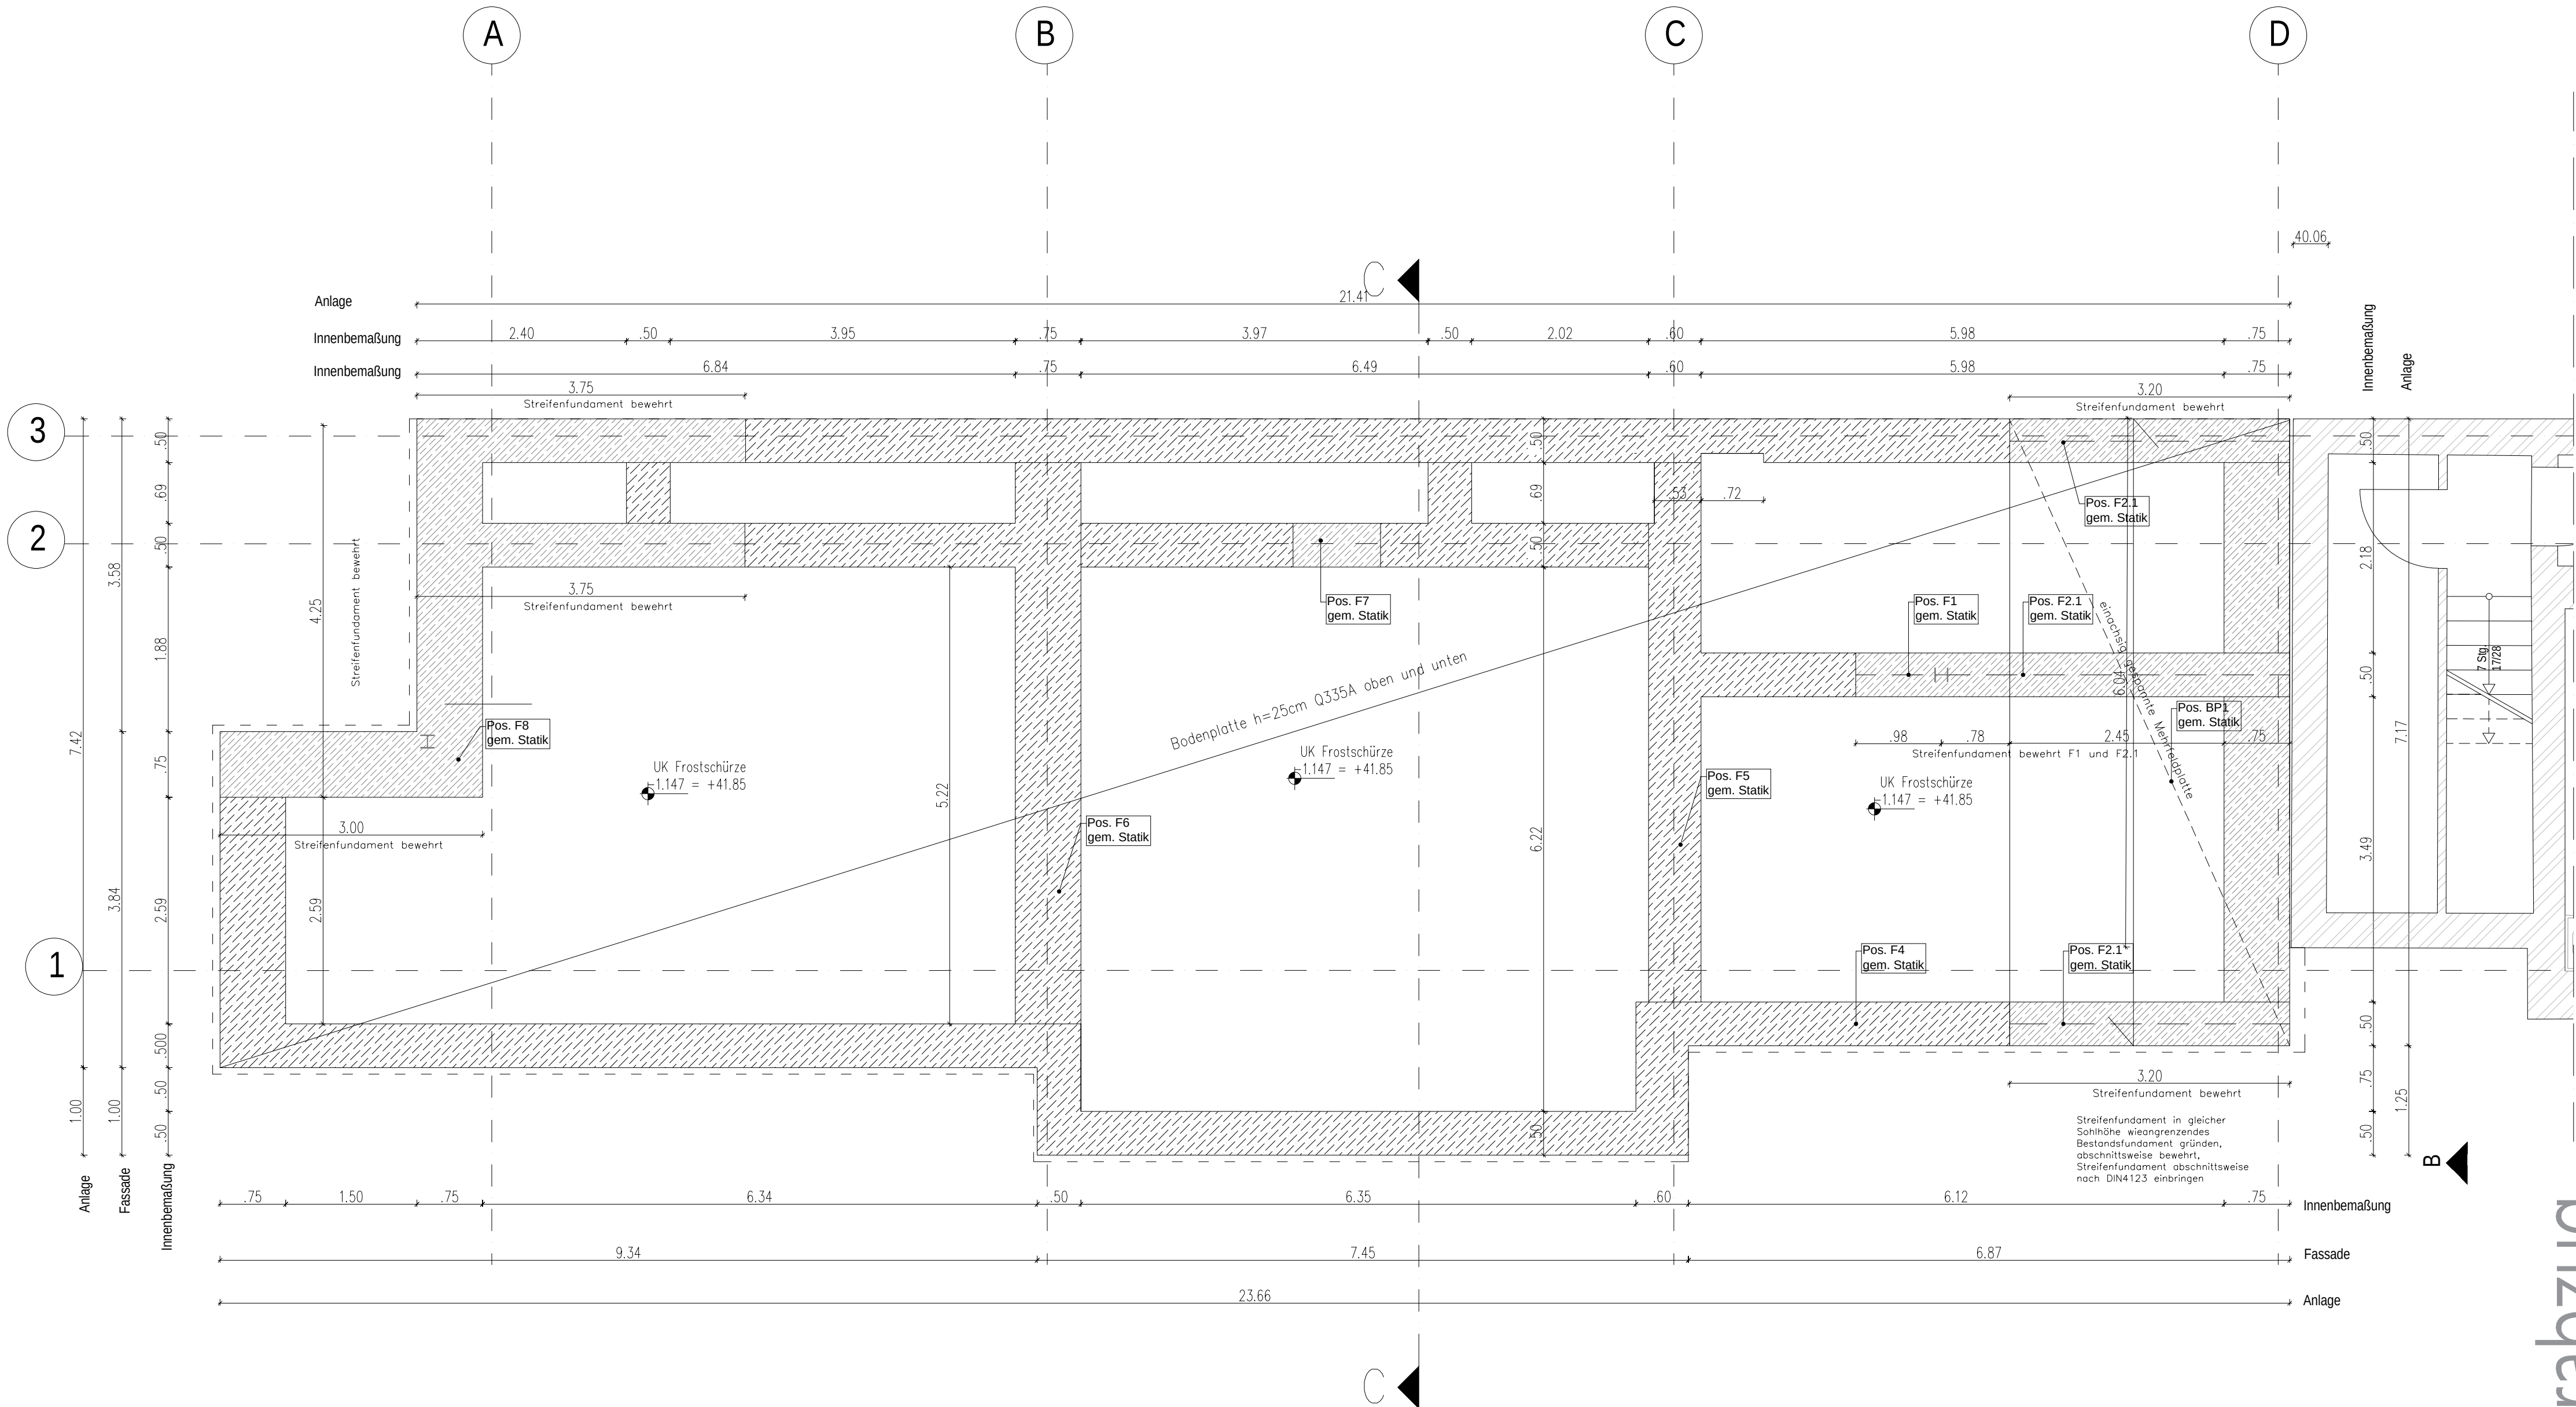

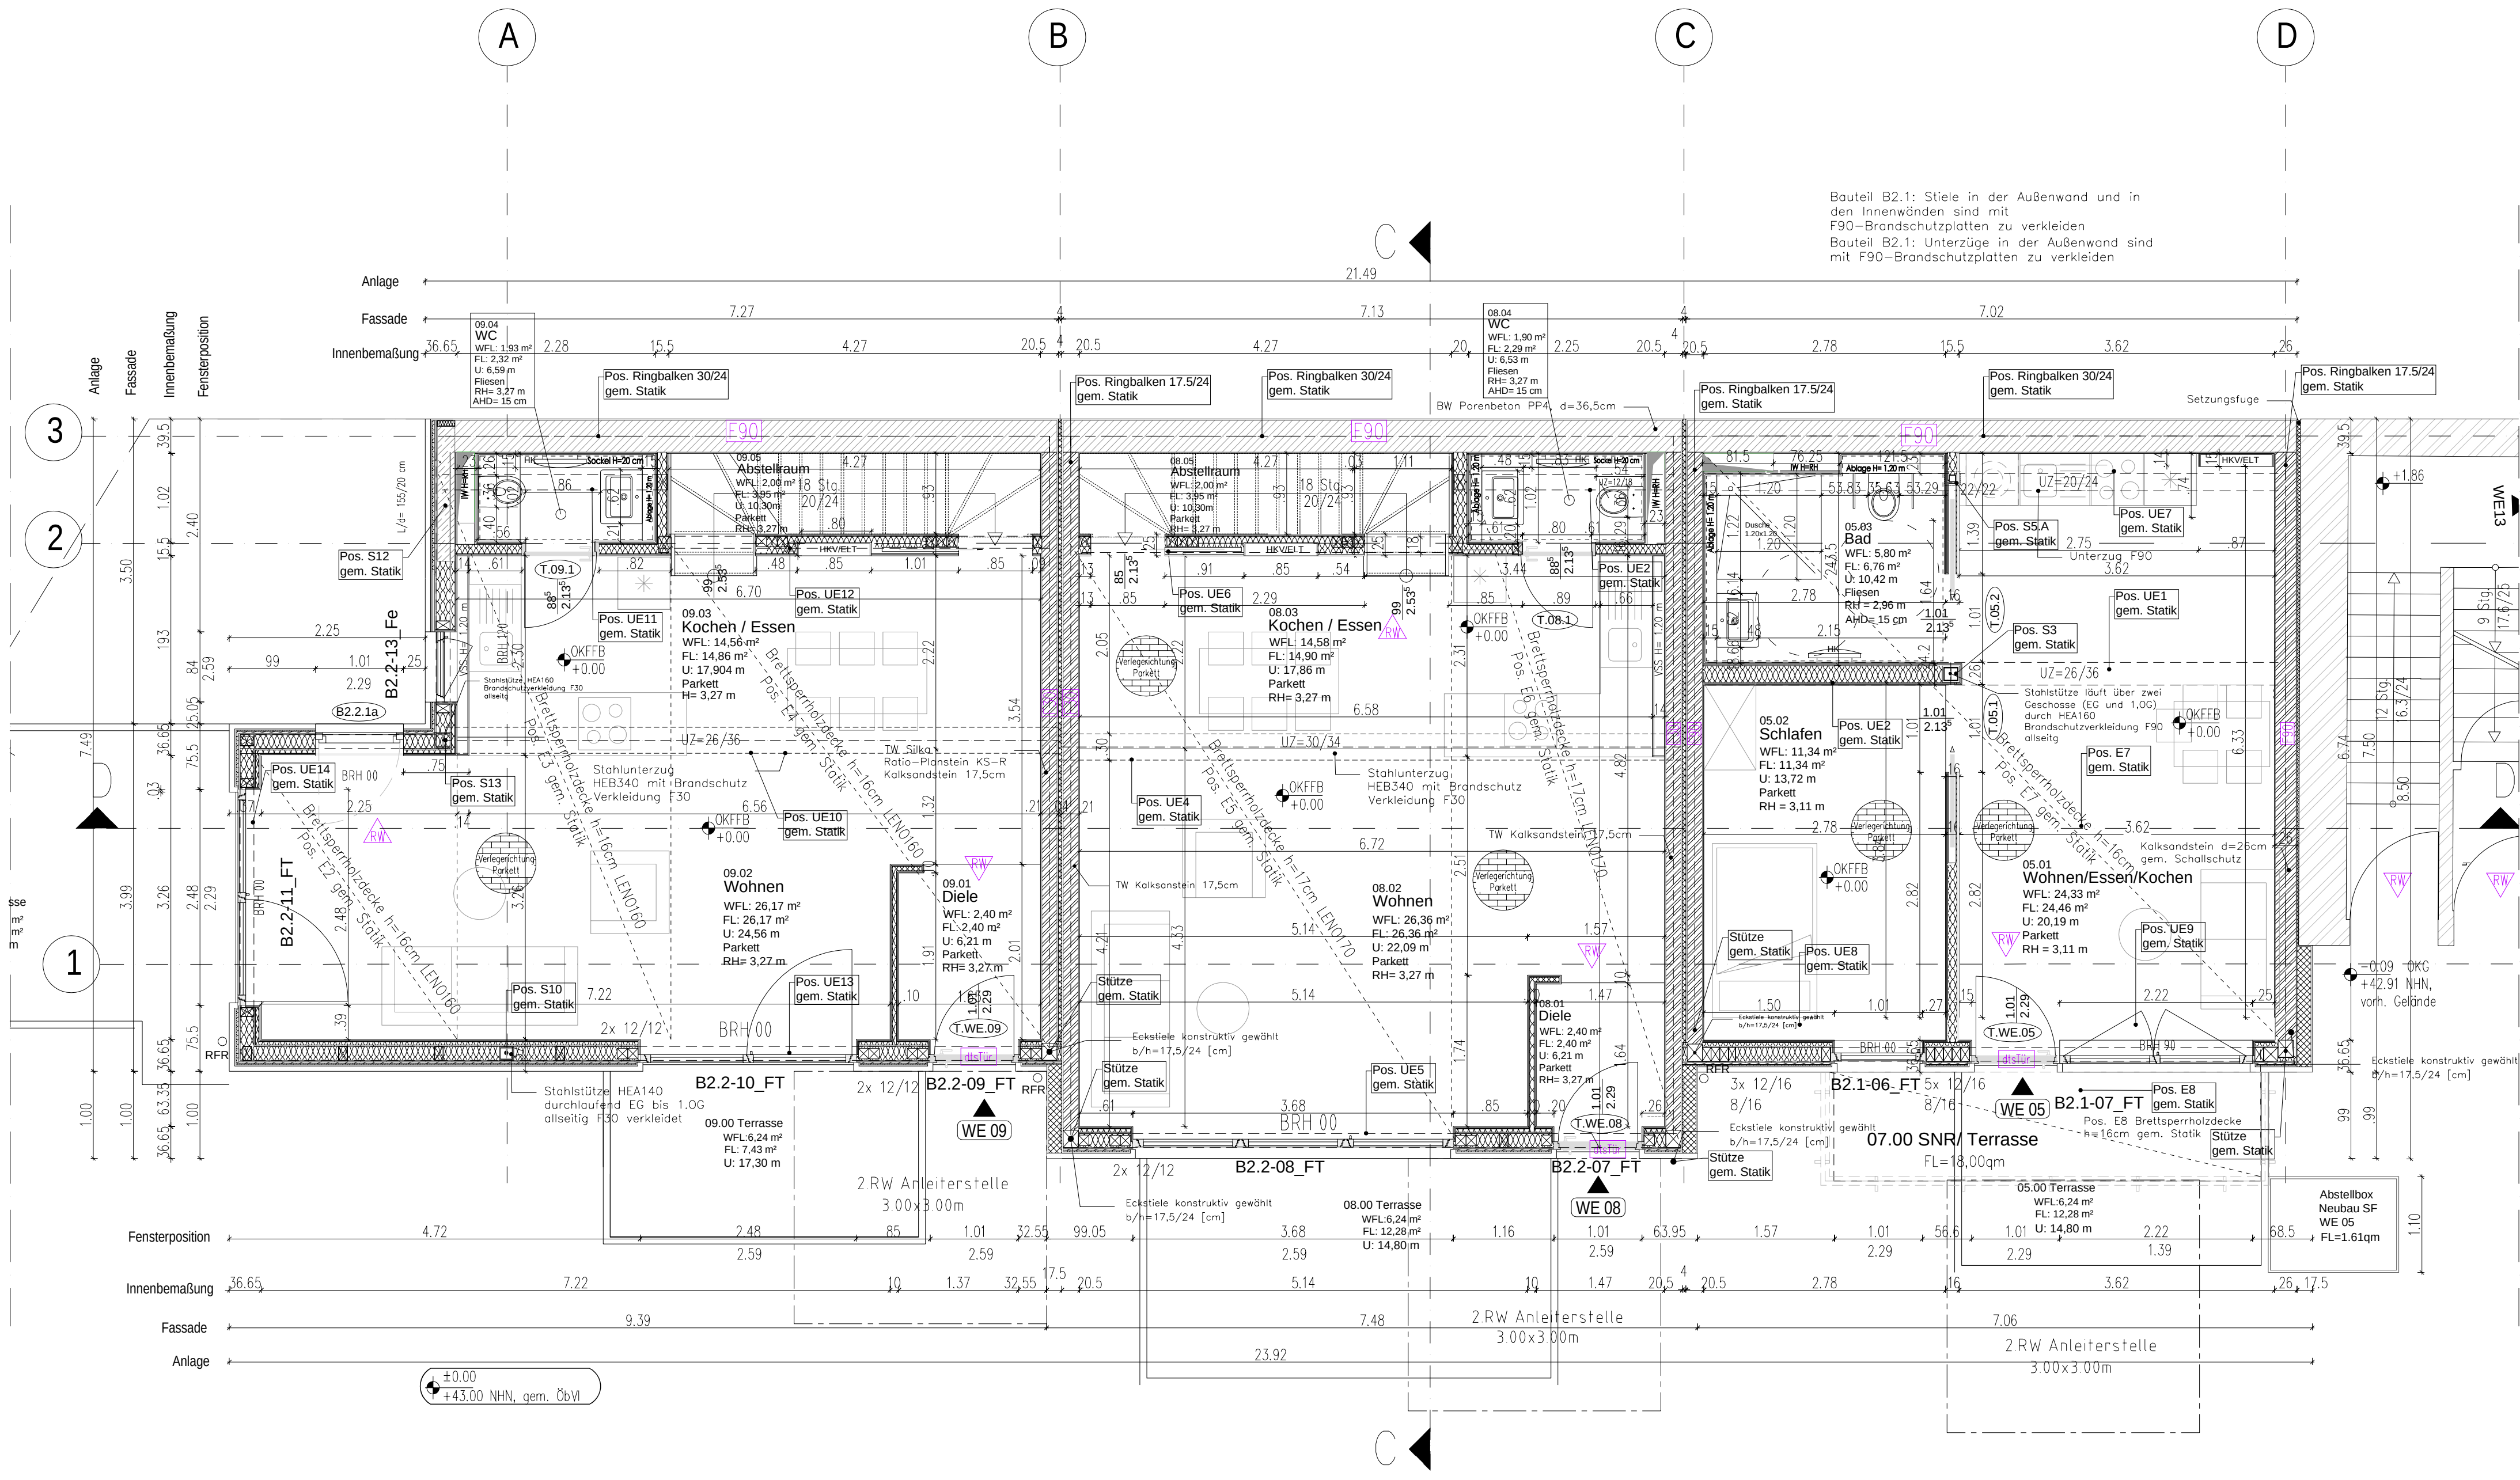

LEGENDE

- AHD abgehängte Decke
AN Ansicht
AW Abwasser
BDW Badewanne
BRH Brüstungshöhe ab OKFF
BW Brandwand
BS Balkenschuh
d dichtschießend
DB Deckenbalken
DDF Dachdurchführung
dstür dicht- und selbstschließend
EB Elastisch gebetteter Balken
ELT Elektroverteilung
FL Fläche
F30 Feuerwiderstandsfähigkeit 30min (feuerhemmend)
F60 Feuerwiderstandsfähigkeit 60min (hochfeuerhemmend)
F90 Feuerwiderstandsfähigkeit 90min (feuerbeständig)
GR Grundriss
H Höhe
HK Heizkörper
HKV Heizkreisverteiler
HT Haustechnik
IW Installationswand
LÜ Lüftung
OK Oberkante
OKFB Oberkante Fertigfußboden
OKG Oberkante Gelände
OL Oberlicht
RB Ringbalken
RFR Regenfallrohr
rs rauchdicht
RR Regenrinne
RA Rauchabzug
RH Raumhoch
RW Rettungsweg
SN Schnitt
T30 Tür feuerhemmend
T30 rs Tür feuerhemmend, rauchdicht selbstschließend
T90 Tür feuerbeständig
T90 rs Tür feuerbeständig, rauchdicht selbstschließend
TRH Traufhöhe
TW Trennwand
UB unbewehrte Frostschräge
UK Unterkante
US Unterschnitt
UZ Unterzug
ÜZ Überzug
VSS Vorsatzschale
WE Wohneinheit
wli Wohnfläche
wmb widerstandsfähig gegen mechanische Beanspruchung
- verdeckte Element Unterzug, Sparren, usw.
Mauerwerk Bestand
Dämmung
Abriss Wand
Mauerwerk Porenbeton
Mauerwerk Kalksandstein
Trockenbau-Innenwände (innerhalb Wohneinheit), gem. Schallschutz und Brandschutz (Montage gemäß Herstellerangaben, z.B. Knauf W112 o.g.w.)
Außenwände in Holztafelbauweise mit Faserzementtafeln oder Holz Verkleidung gem. Schallschutz und Brandschutz
Stahlbeton
Beton
Brandschutzanforderungen
Positionsnummern, Angaben siehe Statik
Positionsnummern, Fenster / Türen
Durchbruch

HINWEIS zur PLANUNG

Dieser Plan gilt nur in Verbindung mit den Ausführungsdetails.
Für alle Ausführungs- bzw. Anschlussdetails siehe aktuellen Detailplansatz. Fenster- und Türenlisten sind zu beachten.
Diese Planung gilt in Verbindung mit dem Ausstattungskatalog.


Die Anwendbarkeit der Detailzeichnung ist durch den Verarbeiter vor Ort an Hand der tatsächlichen Gegebenheiten zu prüfen. Die Technischen Merkblätter der Hersteller und Systemzulassungen sind zu beachten!

Alle Maße und Zeichnungsmaße sind am Bau von der auszuführenden Firma eigenverantwortlich zu prüfen.
Der Ausführende ist verpflichtet, den Auftraggeber auf etwaige Unstimmigkeiten der Ausführungsunterlagen hinzuweisen.
(VOB/B §3 nr.3)

HINWEIS CAD-Zeichnung

Die Erstellung der vorliegenden Planungsunterlagen (GNEISE, basiert auf der durch CAD KÖN und der Schenck Gruppe übergebenen CAD-Zeichnung.
Höhenangaben zu den jeweiligen Hausnummern sind dem amtlichen Lageplan zu entnehmen. Die in den Schnitten dargestellte Höhe (x) entspricht der im Lageplan zu entnehmende Höhenkote Gelände / OKFFEG am Einlaufgang.

Alle Maße sind am Bau zu prüfen!

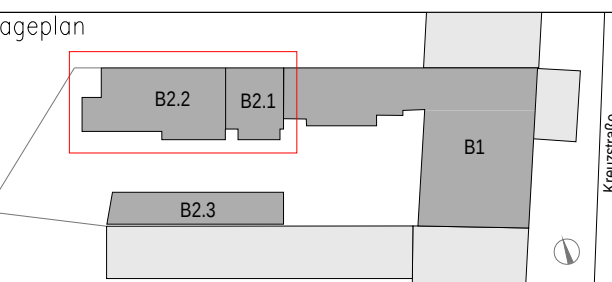

Bauherr

Albert Immo 4 S.ä.r.l.
8d, rue Collart, 8414 Steinfort
Luxemburg

Bauvorhaben

Dachgeschoss-Neubau (Bauteil 1) und
Neubau Seitenflügel-Erweiterung (Bauteil 2.1) /
Reihenhäuser (Bauteil 2.2) / Remise (Bauteil 2.3)

Kreuzstraße 14 in 13187 Berlin, Pankow

Architekten/Ingenieure

GNEISE
Planungs- und Beratungsgesellschaft

GNEISE
Dipl.-Ing. E.-R. Frevert-Henske
Planungs- und Beratungsgesellschaft mbH
Kiehlholzstraße 176, 12437 Berlin
Tel. 030 536 01-0
Fax 030 536 01-333

Planinhalt

Ausführungsplanung

Erdgeschoss

Bauteile 2.1, 2.2 - Neubau

Kreuzstraße 14 in 13187 Berlin, Pankow

C	-	-	-
B	-	-	-
A	01.03.2022	AE	SF Erweiterung, Fensterrahmen
Index	Datum	Gez	Änderung

Datum:	30.11.2021	Maßstab:	1:50
Bearbeitung:	AE	Projektnummer:	19049
Blattgröße:	850x400	Zeichnungs-nr.	KRE14_AP-19049-GR-B2.1.2-4.0
Plotted by Gneise		Schutzvermerk nach DIN 34 beachten!	

LEGENDE

- AHD abgehängte Decke
AN Ansicht
AW Abwasser
BDW Badewanne
BRH Brüstungshöhe ab OKFF
BW Brandwand
BS Balkenschuh
d dichtschießend
DB Deckenbalken
DDF Dachdurchführung
dstür dicht- und selbstschließend
EB Elastisch gebetteter Balken
ELT Elektrounterverteilung
FL Fläche
F30 Feuerwiderstandsfähigkeit 30min (feuerhemmend)
F60 Feuerwiderstandsfähigkeit 60min (hochfeuerhemmend)
F90 Feuerwiderstandsfähigkeit 90min (feuerbeständig)
GR Grundriss
H Höhe
HK Heizkörper
HKV Heizkreisverteiler
HT Haustechnik
IW Installationswand
LÜ Lüftung
OK Oberkante
OKFFB Oberkante Fertigfußboden
OKG Oberkante Gelände
OL Oberlicht
RB Ringbalken
RFR Regenfallrohr
rs rauchdicht
RR Regenrinne
RA Rauchabzug
RH Raumhoch
RW Rettungsweg
SN Schnitt
T30 Tür feuerhemmend
T30 rs Tür feuerhemmend, rauchdicht selbstschließend
T90 Tür feuerbeständig
T90 rs Tür feuerbeständig, rauchdicht selbstschließend
TRH Traufhöhe
TW Trennwand
UB unbewehrte Frostschürze
UK Unterkante
US Unterschnitt
UZ Unterzug
ÜZ Überzug
VSS Vorsatzschale
WE Wohneinheit
Wfl Wohnfläche
wmb widerstandsfähig gegen mechanische Beanspruchung
- verdeckte Element Unterzug, Sparren, usw.
Mauerwerk Bestand
Dämmung
Abriss Wand
Mauerwerk Porenbeton
Mauerwerk Kalksandstein
Trockenbau-Innenwände (innerhalb Wohneinheit), gem. Schallschutz und Brandschutz (Montage gemäß Herstellerangaben, z.B. Knauf W112 o.g.w.)
Außenwände in Holztafelbauweise mit Faserzementtafeln oder Holz Verkleidung gem. Schallschutz und Brandschutz
- Stahlbeton
Beton
T30dts Brandschutzanforderungen
Pos 01-1 Positionennummern, Angaben siehe Statik
Pos 01-1 Positionennummern, Fenster / Türen
Durchbruch

HINWEIS zur PLANUNG

Dieser Plan gilt nur in Verbindung mit den Ausführungsdetails.
Für alle Ausführungs- bzw. Anschlussdetails siehe aktuellen Detailplansatz. Fenster- und Türenlisten sind zu beachten.
Diese Planung gilt in Verbindung mit dem Ausstattungskatalog.


Die Anwendbarkeit der Detailzeichnung ist durch den Verarbeiter vor Ort an Hand der tatsächlichen Gegebenheiten zu prüfen.
Die Technischen Merkblätter der Hersteller und Systemzulassungen sind zu beachten!

Alle Maße und Zeichnungsmaße sind am Bau von der auszuführenden Firma eigenverantwortlich zu prüfen.
Der Ausführende ist verpflichtet, den Auftraggeber auf etwaige Unstimmigkeiten der Ausführungsunterlagen hinzuweisen.
(VOB/B §3 nr. 3)

HINWEIS CAD-Zeichnung

Die Erstellung der vorliegenden Planungsunterlagen (GNEISE, basiert auf der durch CAD KON und der Scherneck Gruppe übergebenen CAD-Zeichnung.
Höhenangaben zu den jeweiligen Hausnummern sind dem amtlichen Lageplan zu entnehmen. Die in den Schnitten dargestellte Höhe (x) entspricht der im Lageplan zu entnehmende Höhenkote Gelände / OKFFBEG am Einzelaufgang.

Alle Maße sind am Bau zu prüfen!

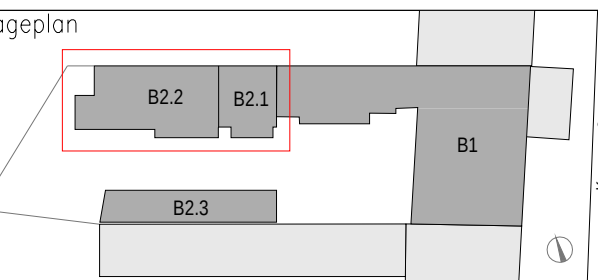

Bauherr

Albert Immo 4 S.ö.r.l.
8d, rue Collart, 8414 Steinfort
Luxemburg

Bauvorhaben

Dachgeschoss-Neubau (Bauteil 1) und
Neubau Seitenflügel-Erweiterung (Bauteil 2.1) /
Reihenhäuser (Bauteil 2.2) / Remise (Bauteil 2.3)

Kreuzstraße 14 in 13187 Berlin, Pankow

Architekten/Ingenieure

GNEISE
Planungs- und Beratungsgesellschaft

GNEISE
Dipl.-Ing. E.-R. Frevert-Henske
Planungs- und Beratungsgesellschaft mbH
Kiehlholzstraße 176, 12437 Berlin
Tel. 030 536 01-0
Fax 030 536 01-333

Planinhalt

Ausführungsplanung

1. Obergeschoss

Bauteile 2.1, 2.2 - Neubau


Kreuzstraße 14 in 13187 Berlin, Pankow

C	-	-	-
B	-	-	-
A	01.03.2022	AE	SF Erweiterung, Fensterhöhen
Index	Datum	Gez	Änderung

Datum:	30.11.2021	Maßstab:	1:50
Bearbeitung:	AE	Projektnummer:	19049
Blattgröße:	830x297	Zeichnungsnr.:	KRE14_AP-19049-GR-B2.1.2-4.1
Plotted by Gneise		Schutzvermerk nach DIN 34 beachten!	

Vorabzug

Bauteil B2.1: Stiele in der Außenwand und in den Innenwänden sind mit F90-Brandschutzplatten zu verkleiden.
Bauteil B2.1: Unterzüge in der Außenwand sind mit F90-Brandschutzplatten zu verkleiden.

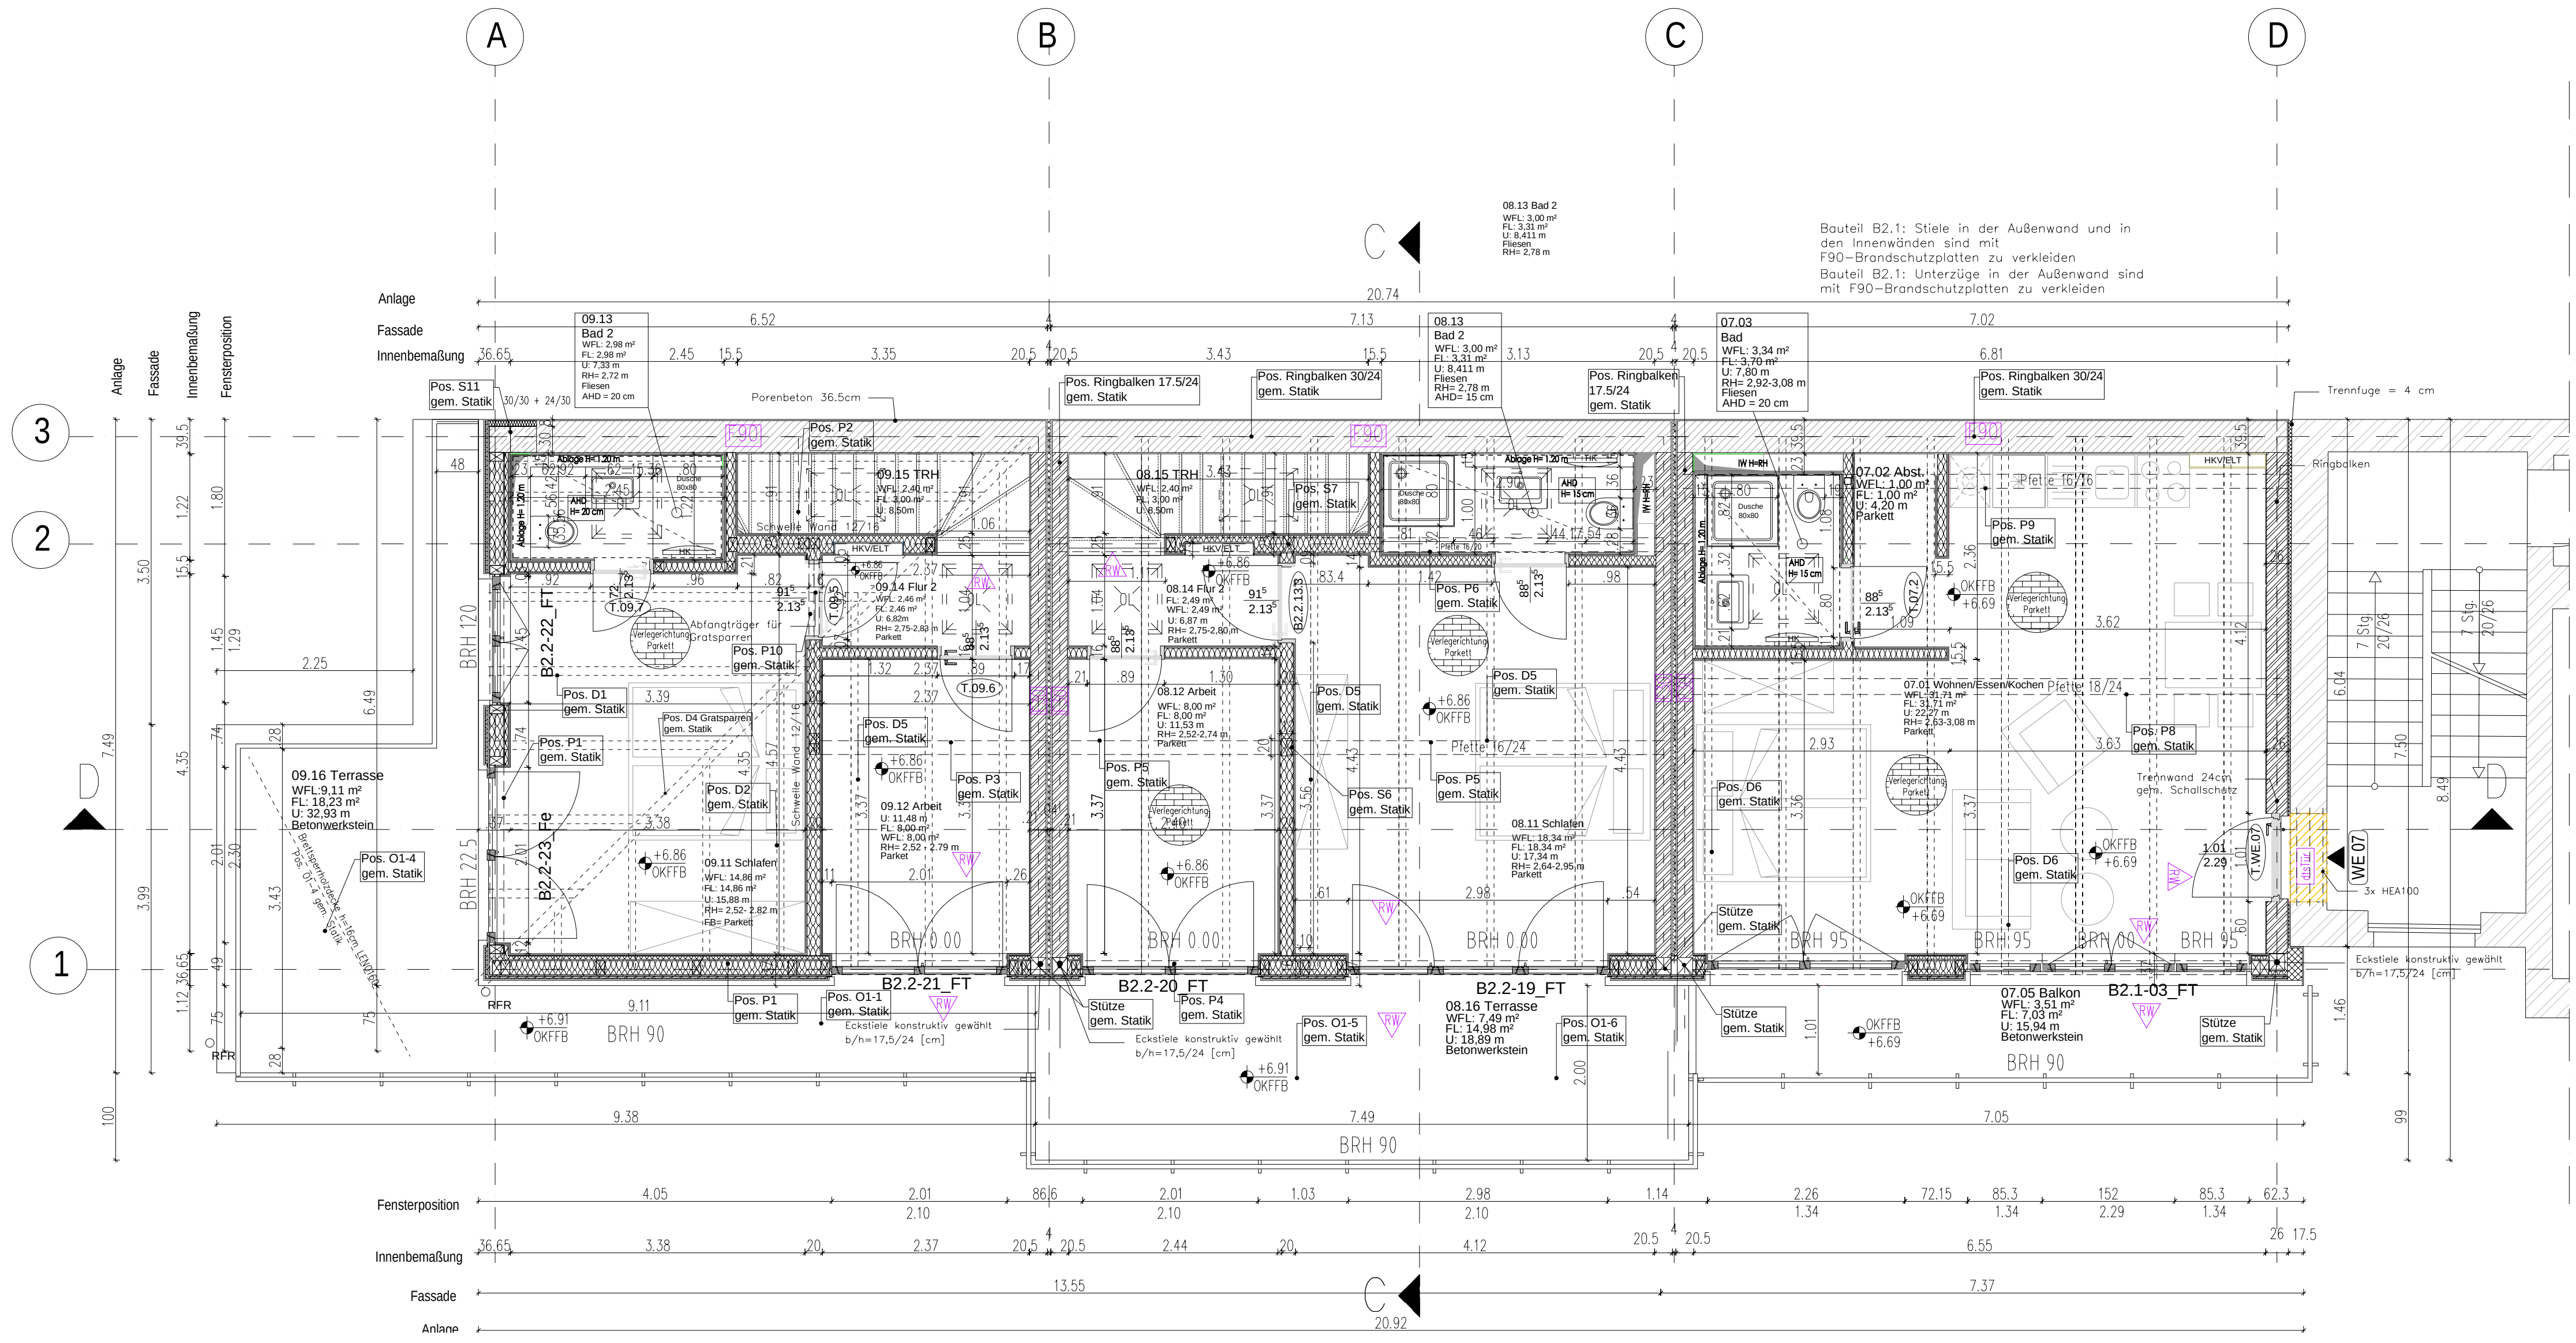

- LEGENDE**
- AHD abgehängte Decke
 - AN Ansicht
 - AW Abwasser
 - BDW Badewanne
 - BRH Brüstungshöhe ab OKFF
 - BW Brandwand
 - BS Balkenschuh
 - d dichtschießend
 - DB Deckenbalken
 - DDF Dachdurchführung
 - dstür dicht- und selbstschließend
 - EB Elastisch gebetteter Balken
 - ELT Elektrointerverteilung
 - FL Fläche
 - F30 Feuerwiderstandsfähigkeit 30min (feuerhemmend)
 - F60 Feuerwiderstandsfähigkeit 60min (hochfeuerhemmend)
 - F90 Feuerwiderstandsfähigkeit 90min (feuerbeständig)
 - GR Grundriss
 - H Höhe
 - HK Heizkörper
 - HKV Heizkreisverteiler
 - HT Haustechnik
 - IW Installationswand
 - LÜ Lüftung
 - OK Oberkante
 - OKFFB Oberkante Fertigfußboden
 - OKG Oberkante Gelände
 - OL Oberlicht
 - RB Ringbalken
 - RFR Regenfallrohr
 - rs rauchdicht
 - RR Regenrinne
 - RA Rauchabzug
 - RH Raumhoch
 - RW Rettungsweg
 - SN Schnitt
 - T30 Tür feuerhemmend
 - T30 rs Tür feuerhemmend, rauchdicht selbstschließend
 - T90 Tür feuerbeständig
 - T90 rs Tür feuerbeständig, rauchdicht selbstschließend
 - TRH Traufhöhe
 - TW Trennwand
 - UB unbewehrte Frostschrütze
 - UK Unterkante
 - US Unterschnitt
 - UZ Unterzug
 - ÜZ Überzug
 - VSS Vorsatzschale
 - WE Wohneinheit
 - Wfl Wohnfläche
 - wmb widerstandsfähig gegen mechanische Beanspruchung
 - verdeckte Element Unterzug, Sparren, usw.
 - Mauerwerk Bestand
 - Dämmung
 - Abriss Wand
 - Mauerwerk Porenbeton
 - Mauerwerk Kalksandstein
 - Trockenbau-Innenwände (innerhalb Wohneinheit), gem. Schallschutz und Brandschutz (Montage gemäß Herstellerangaben, z.B. Knauf W112 o.g.w.)
 - Außenwände in Holztafelbauweise mit Faserzementtafeln oder Holz Verkleidung gem. Schallschutz und Brandschutz
 - Stahlbeton
 - Beton
 - Brandschutzanforderungen
 - Positionsnr., Angaben siehe Statik
 - Positionsnr., Fenster / Türen
 - Durchbruch

HINWEIS zur PLANUNG

Dieser Plan gilt nur in Verbindung mit den Ausführungsdetails.
Für alle Ausführungs- bzw. Anschlussdetails siehe aktuellen Detailplansatz.
Fenster- und Türenlisten sind zu beachten.
Diese Planung gilt in Verbindung mit dem Ausstattungskatalog.


Die Anwendbarkeit der Detailzeichnung ist durch den Verarbeiter vor Ort an Hand der tatsächlichen Gegebenheiten zu prüfen.
Die Technischen Merkblätter der Hersteller und Systemzulassungen sind zu beachten!

Alle Maße und Zeichnungsmaße sind am Bau von der auszuführenden Firma eigenverantwortlich zu prüfen.
Der Ausführende ist verpflichtet, den Auftraggeber auf etwaige Unstimmigkeiten der Ausführungsunterlagen hinzuweisen.
(VOB/B §3 nr. 3)

HINWEIS CAD-Zeichnung

Die Erstellung der vorliegenden Planungsunterlagen (GNEISE, basierend auf der durch CAD KÖN und der Scherneck Gruppe übergebenen CAD-Zeichnung) ist die Verantwortung der jeweiligen Hausnummern sind dem amtlichen Lageplan zu entnehmen. Die in den Schnitten dargestellte Höhe (x) entspricht der im Lageplan zu entnehmende Höhenkote Gelände / OKFFBEG am Einzelfußgang.

Alle Maße sind am Bau zu prüfen!

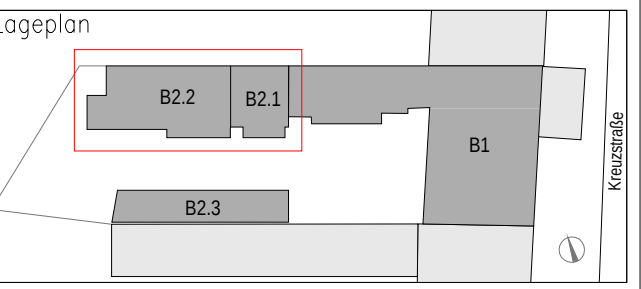

Bauherr

Albert Immo 4 S.ä.r.l.
8d, rue Collart, 8414 Steinfort
Luxemburg

Bauvorhaben

**Dachgeschoss-Neubau (Bauteil 1) und
Neubau Seitenflügel-Erweiterung (Bauteil 2.1) /
Reihenhäuser (Bauteil 2.2) / Remise (Bauteil 2.3)**

Kreuzstraße 14 in 13187 Berlin, Pankow

Architekten/Ingenieure

GNEISE
Planungs- und Beratungsgesellschaft


GNEISE
Dipl.-Ing. E.-R. Frevert-Henske
Planungs- und Beratungsgesellschaft mbH

Kiehlholzstraße 176, 12437 Berlin
Tel. 030 536 01-0
Fax 030 536 01-333

Planinhalt

Ausführungsplanung			
2. Obergeschoss			
Bauteile 2.1, 2.2 - Neubau			
Kreuzstraße 14 in 13187 Berlin, Pankow			
C	-	-	-
B	-	-	-
A	01.03.2022	AE	SF Erweiterung, Fensterhöhen
Index	Datum	Gez	Änderung

Datum:	30.11.2021	Maßstab:	1:50
Bearbeitung:	AE	Projektnummer:	19049
Blattgröße:	850x400	Zeichnungs-nr.	KRE14_AP-19049-GR-B2.1.2-4.2
Plotted by	Gneise	Schutzvermerk nach DIN 34 beachten!	

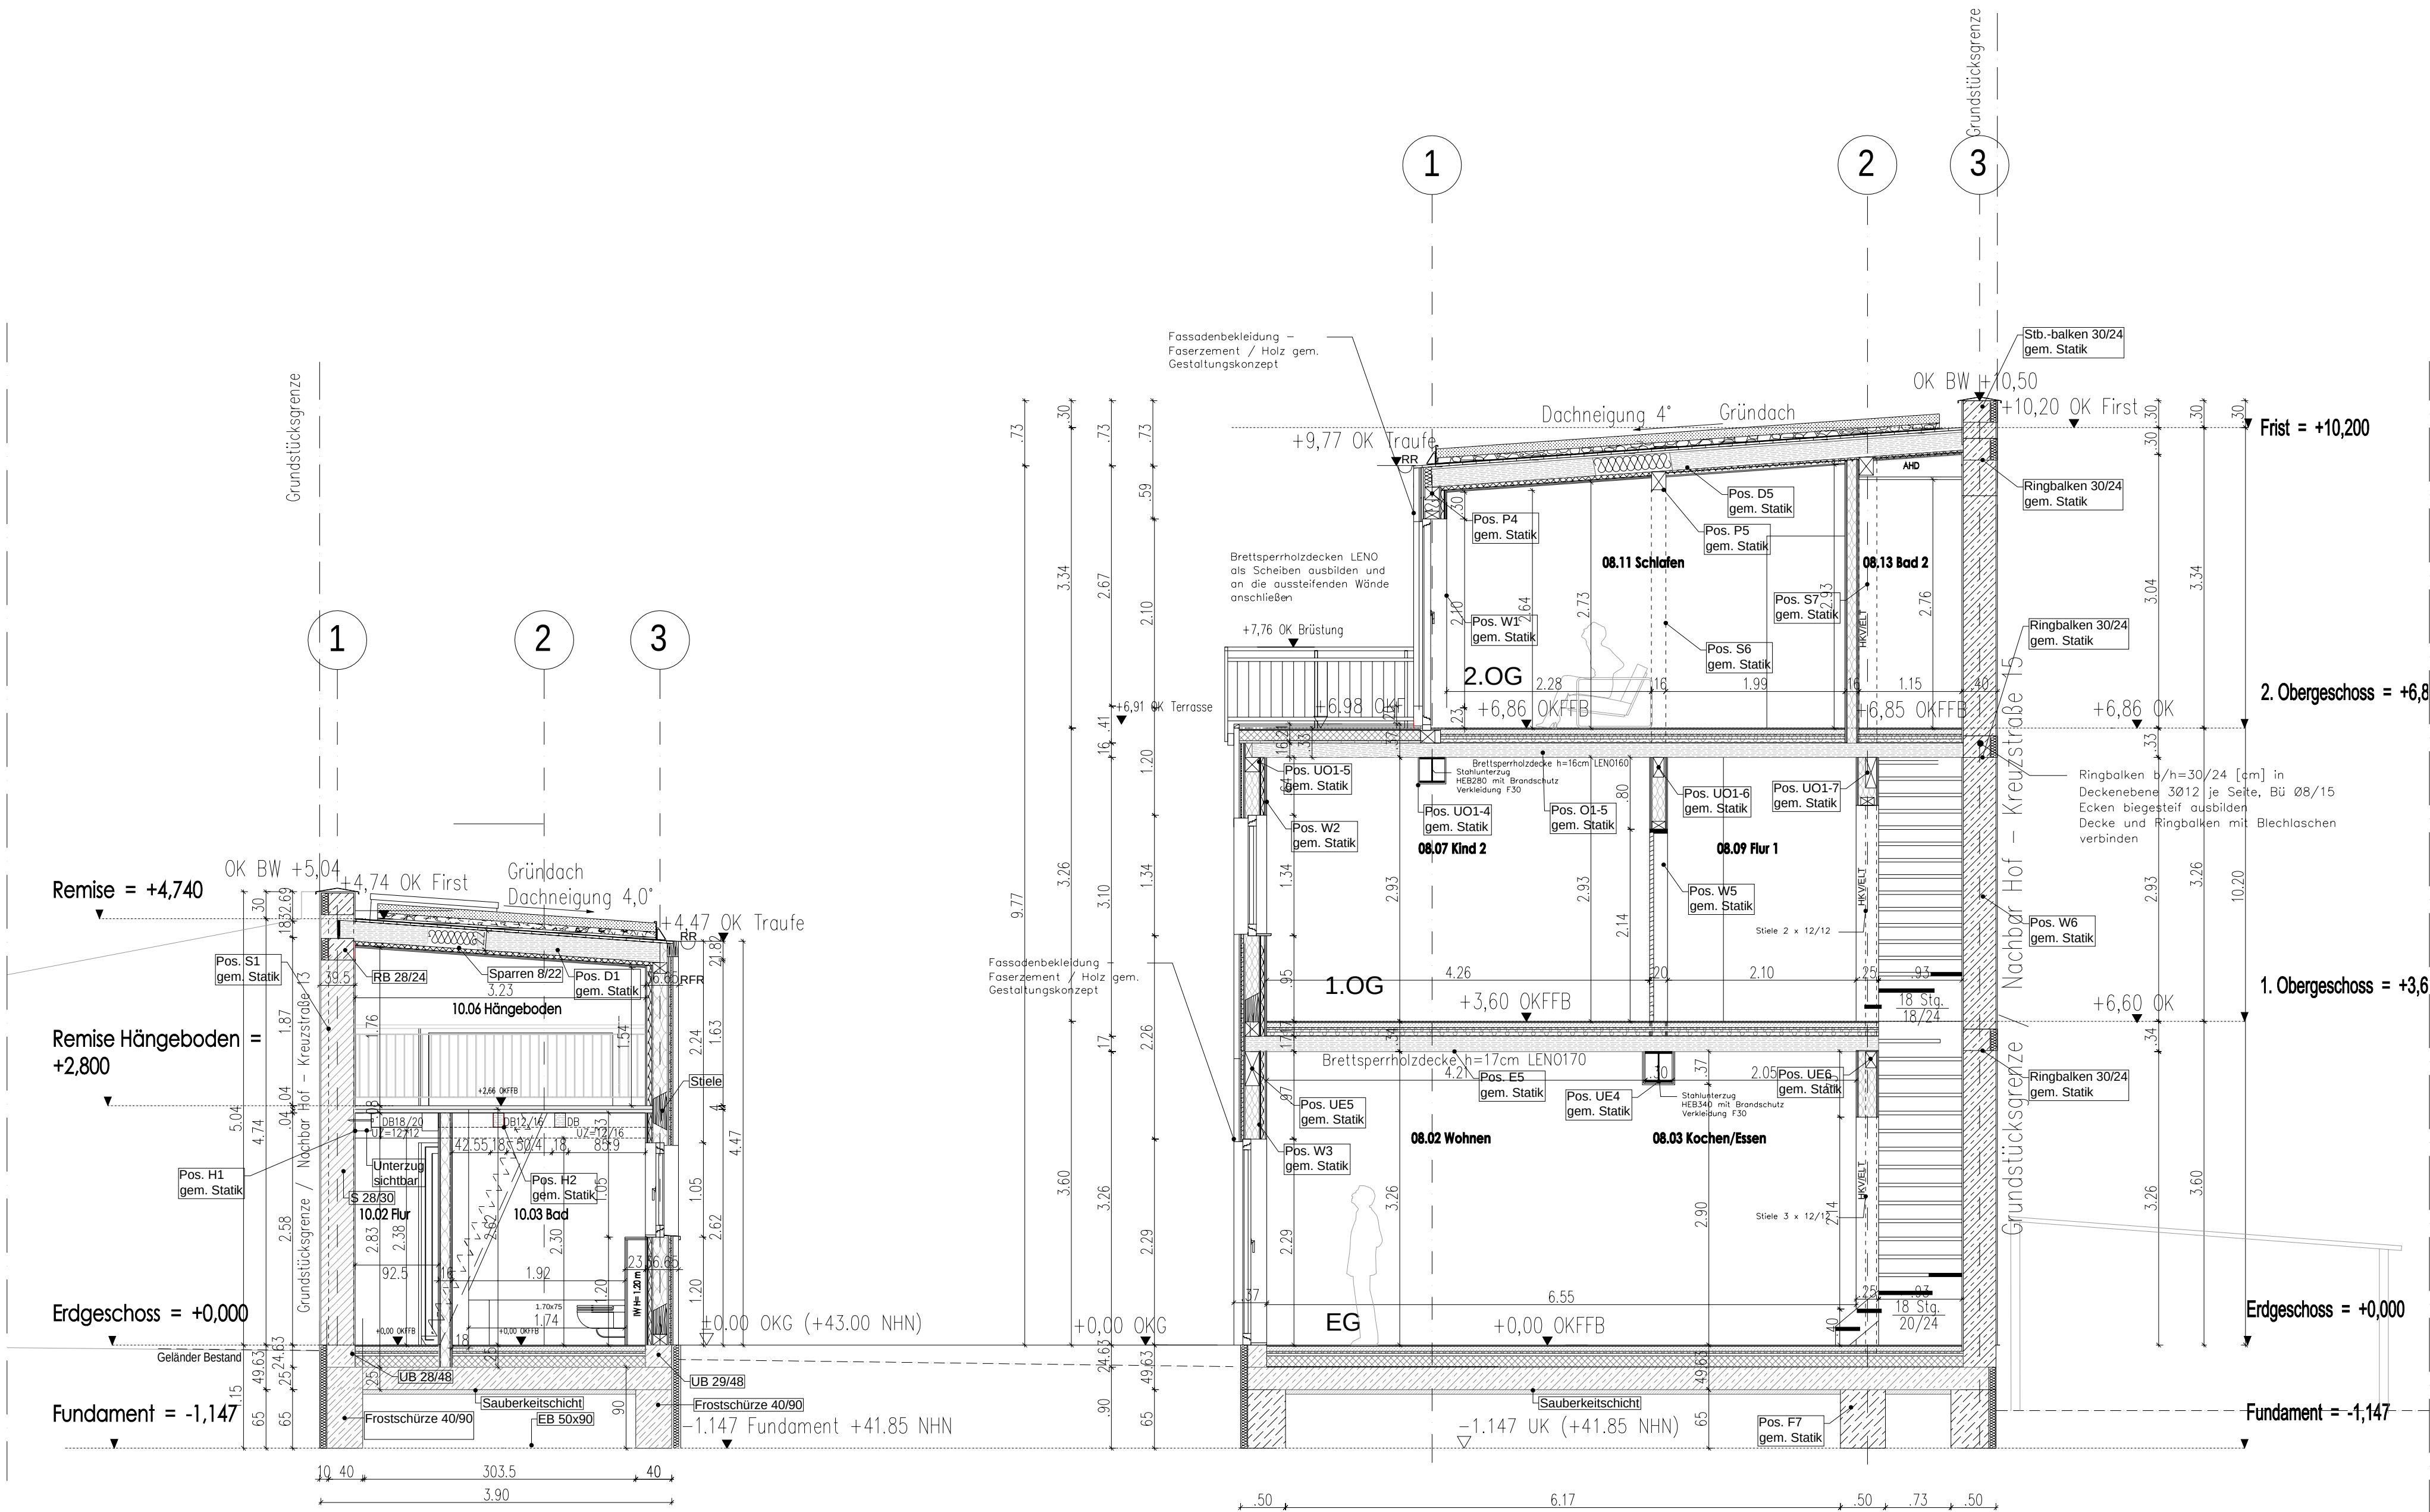

LEGENDE

AHD

abgehängte Decke

AN

Ansicht

AW

Abwasser

BDW

Badewanne

BRH

Brüstungshöhe ab OKFF

BW

Brandwand

BS

Balkenschuh

d

dichtschließend

DB

Deckenbalken

DDF

Dachdurchführung

dstür

dicht- und selbstschließend

EB

Elastisch gebetteter Balken

ELT

Elektroverteilung

FL

Fläche

F30

Feuerwiderstandsfähigkeit 30min (feuerhemmend)

F60

Feuerwiderstandsfähigkeit 60min (hochfeuerhemmend)

F90

Feuerwiderstandsfähigkeit 90min (feuerbeständig)

GR

Grundriss

H

Höhe

HK

Heizkörper

HKV

Heizkreisverteiler

HT

Haustechnik

IW

Installationswand

LÜ

Lüftung

OK

Oberkante

OKFFB

Oberkante Fertigfußboden

OKG

Oberkante Gelände

OL

Oberlicht

RB

Ringbalken

RFR

Regenfallrohr

rs

rauchdicht

RR

Regenrinne

RA

Rauchabzug

RH

Raumhoch

RW

Rettungsweg

SN

Schnitt

T30

Tür feuerhemmend

T30 rs

Tür feuerhemmend, rauchdicht selbstschließend

T90

Tür feuerbeständig

T90 rs

Tür feuerbeständig, rauchdicht selbstschließend

TRH

Traufhöhe

TW

Trennwand

UB

unbewehrte Frostschrünze

UK

Unterkante

US

Unterschnitt

UZ

Unterzug

ÜZ

Überzug

VSS

Vorsatzschale

WE

Wohneneinheit

Wfl

Wohnfläche

wmb

widerstandsfähig gegen mechanische Beanspruchung

verdeckte Element Unterzug, Sparren, usw.

Mauerwerk Bestand

Dämmung

Abriss Wand

Mauerwerk Porenbeton

Mauerwerk Kalksandstein

Trockenbau-Innenwände (innerhalb Wohneinheit), gem. Schallschutz und Brandschutz (Montage gemäß Herstellerangaben, z.B. Knauf W112 o.g.w.)

Außenwände in Holztafelbauweise mit Faserzementtafeln oder Holz Verkleidung gem. Schallschutz und Brandschutz

Stahlbeton

Beton

Brandschutzanforderungen

Positionennummern, Angaben siehe Statik

Positionennummern, Fenster / Türen

Durchbruch

C

-

-

-

B

-

-

-

A

01.03.2022

AE

SF Erweiterung, Fensterhöhen

Index

Datum

Gez

Änderung

Datum:

30.11.2021

Maßstab:

1:50

Bearbeitung:

Projektnummer:

19049

Blattgröße:

830x297

Zeichnungs-nr.

KRE14_AP-19049-SN-B2.1.2-5.0

Plotted by Gneise

Schutzvermerk nach DIN 34 beachten!

HINWEIS zur PLANUNG

Dieser Plan gilt nur in Verbindung mit den Ausführungsdetails.

Für alle Ausführungs- bzw. Anschlussdetails siehe aktuellen Detailplansatz Fenster- und Türenlisten sind zu beachten.

Diese Planung gilt in Verbindung mit dem Ausstattungskatalog.

Die Anwendbarkeit der Detailzeichnung ist durch den Verarbeiter vor Ort an Hand der tatsächlichen Gegebenheiten zu Prüfen.

Die Technischen Merkblätter der Hersteller und Systemzulassungen sind zu beachten!

Alle Maße und Zeichnungsmaße sind am Bau von der auszuführenden Firma eigenverantwortlich zu prüfen.

Der Ausführende ist verpflichtet, den Auftraggeber auf etwaige Unstimmigkeiten der Ausführungsunterlagen hinzuweisen.

(VOB/B §3 nr. 3)

HINWEIS CAD-Zeichnung

Die Erstellung der vorliegenden Planungsunterlagen (GNEISE), basiert auf der durch CAD KÖN und der Scherbeck Gruppe übergebenen CAD-Zeichnung.

Höhenangaben zu den jeweiligen Hausnummern sind dem amtlichen Lageplan zu entnehmen. Die in den Schnitten dargestellte Höhe (x) entspricht der im Lageplan zu entnehmende Höhenkote Gelände / OKFFBEG am Einzelaufgang.

Alle Maße sind am Bau zu prüfen!

Lageplan

Bauherr

Albert Immo 4 S.ö.r.l.

8d, rue Collart, 8414 Steinfort

Luxemburg

Bauvorhaben

Dachgeschoss-Neubau (Bauteil 1) und

Neubau Seitenflügel-Erweiterung (Bauteil 2.1) /

Reihenhäuser (Bauteil 2.2) / Remise (Bauteil 2.3)

Kreuzstraße 14 in 13187 Berlin, Pankow

Architekten/Ingenieure

GNEISE

Planungs- und Beratungsgesellschaft

GNEISE

Dipl.-Ing. E.-R. Frevert-Henske

Planungs- und Beratungsgesellschaft mbH

Kiehlholzstraße 176, 12437 Berlin

Tel. 030 536 01-0

Fax 030 536 01-333

Planinhalt

Ausführungsplanung

Schnitt C-C

Bauteile 2.1, 2.2 + B2.3 Neubau

Kreuzstraße 14 in 13187 Berlin, Pankow

C

-

-

-

B

-

-

-

A

01.03.2022

AE

SF Erweiterung, Fensterhöhen

Index

Datum

Gez

Änderung

Datum:

30.11.2021

Maßstab:

1:50

Bearbeitung:

Projektnummer:

19049

Blattgröße:

830x297


Zeichnungs-nr.

KRE14_AP-19049-SN-B2.1.2-5.0

Plotted by Gneise

Schutzvermerk nach DIN 34 beachten!

Diese Zeichnung ist urheberrechtlich geschützt. Bei Weitergabe -auch auszugsweise- ist die Gneise Planungs- und Beratungsgesellschaft mbH als Urheber auf dem Plan zu vermerken!

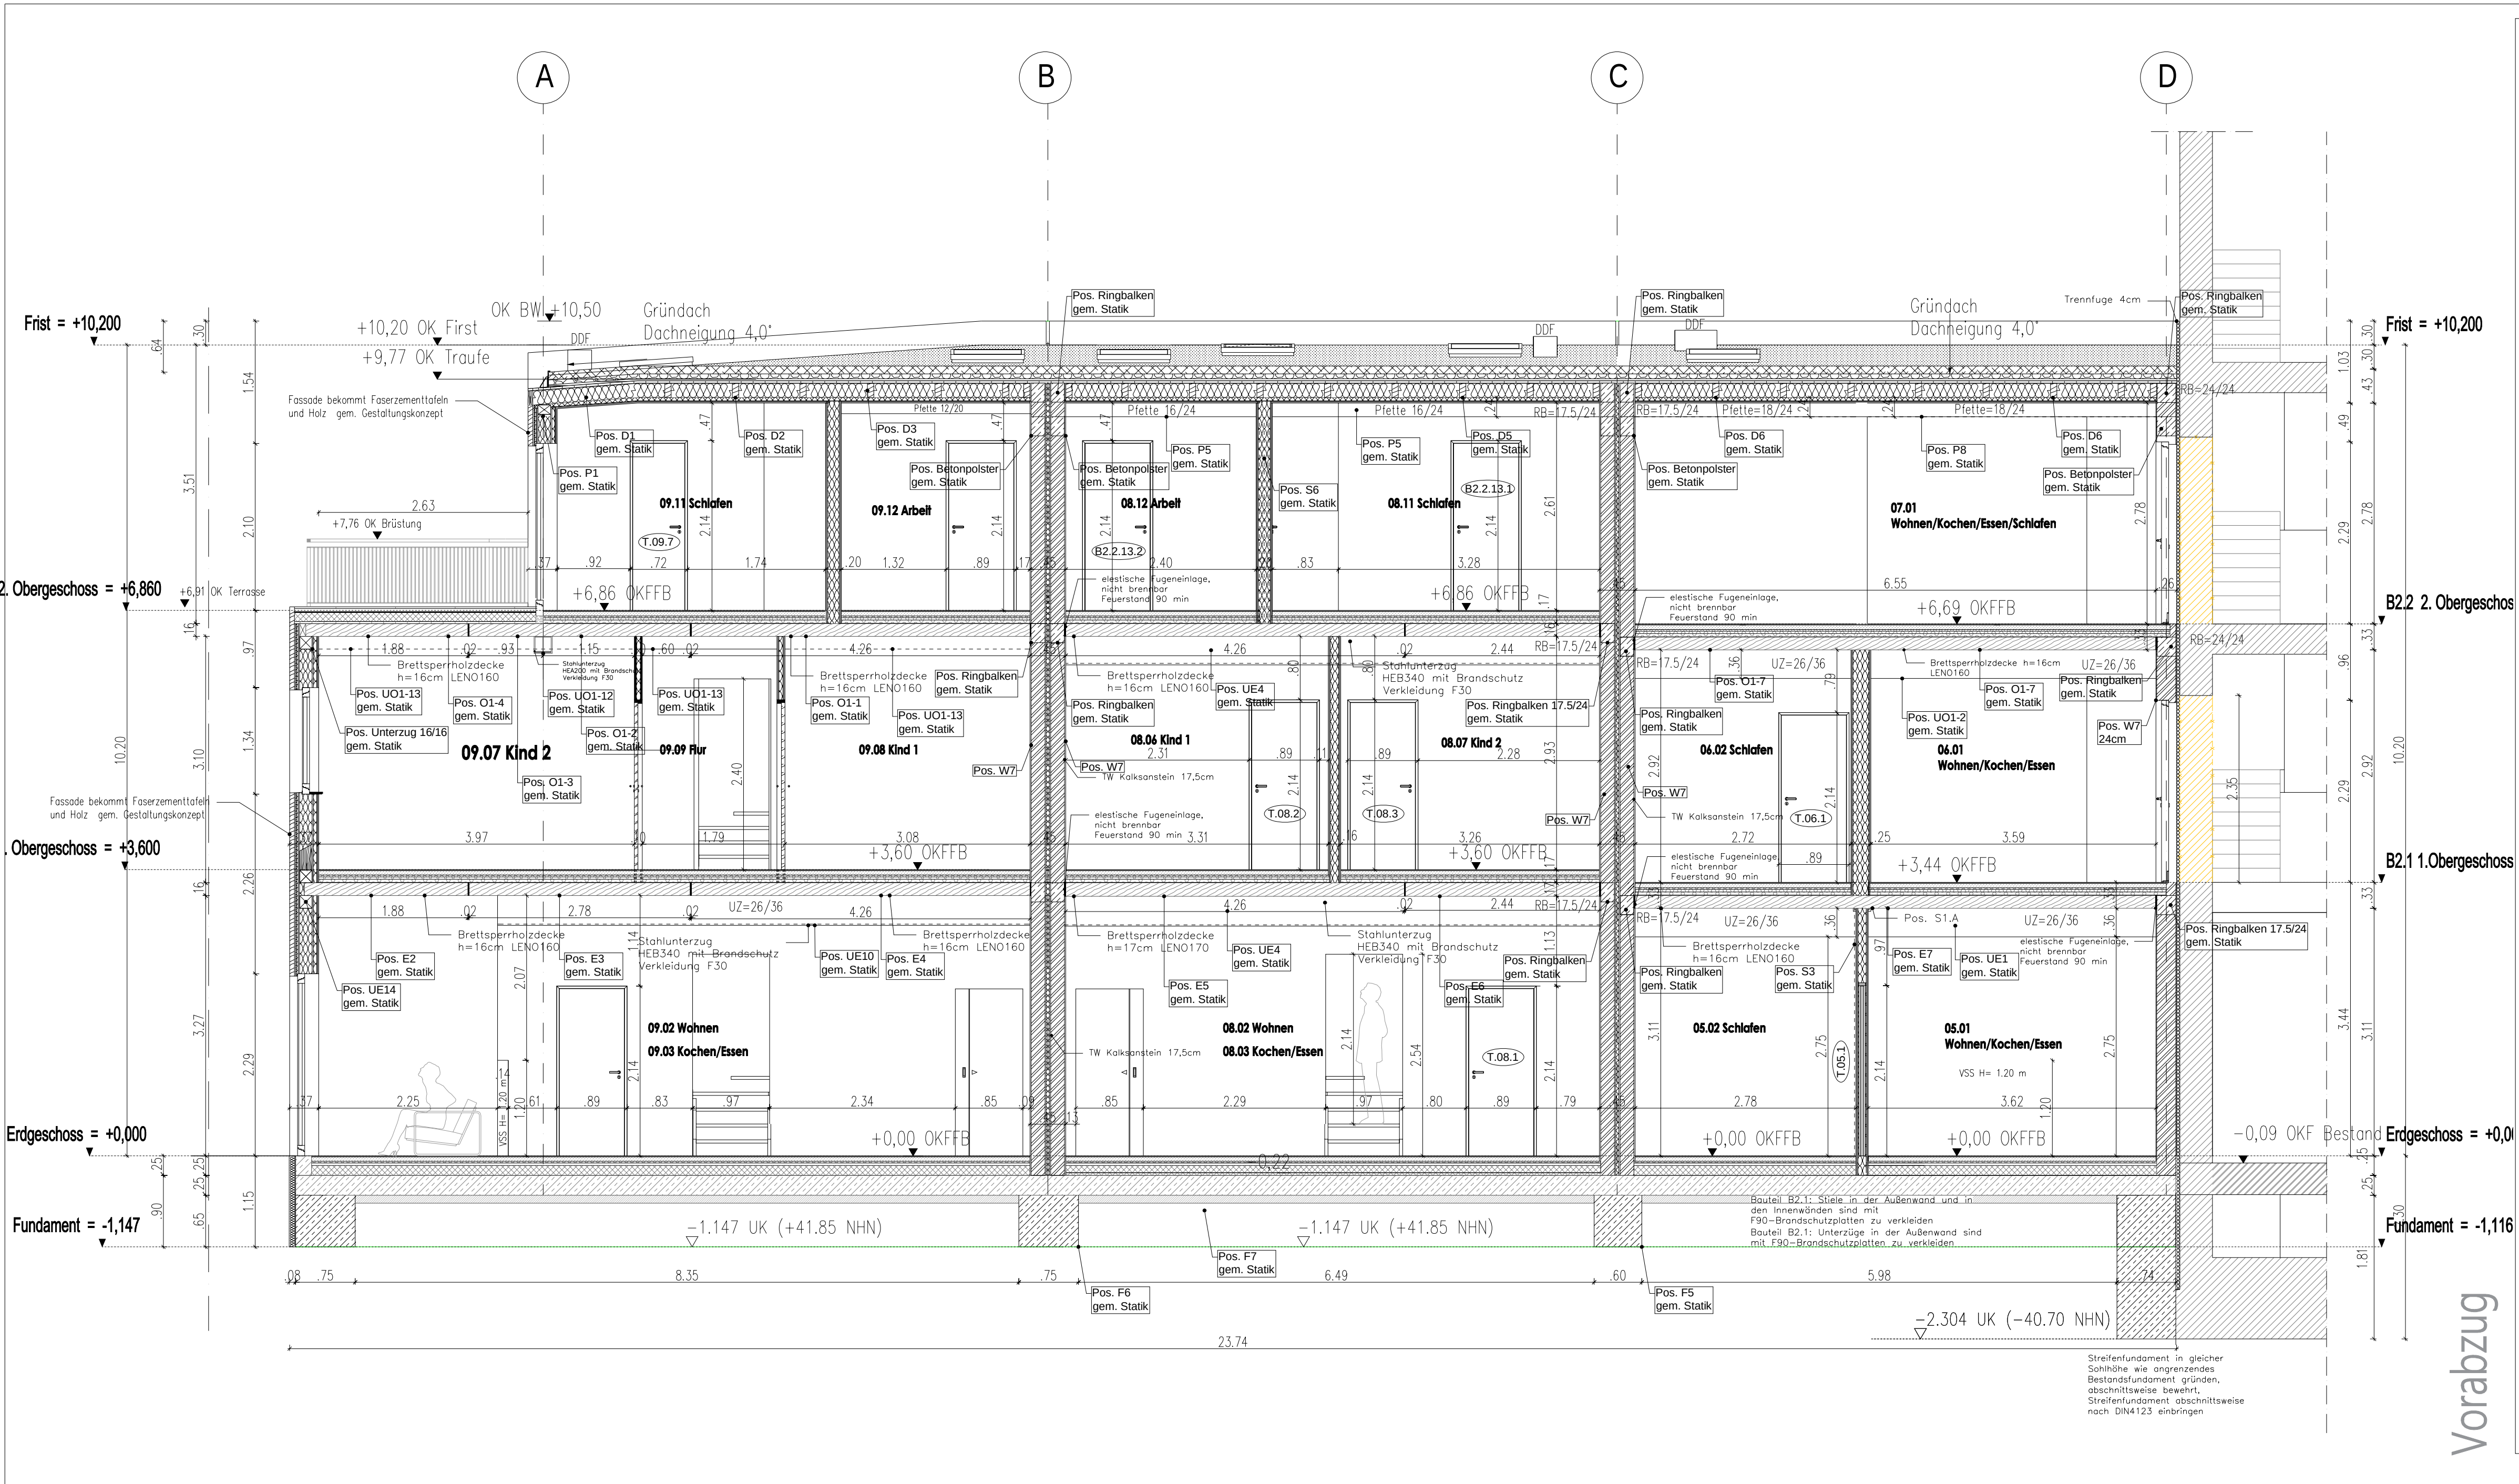

LEGENDE	
AHD	abgehängte Decke
AN	Ansicht
AW	Abwasser
BDW	Badewanne
BRH	Brüstungshöhe ab OKFF
BW	Brandwand
BS	Balkenschuh
d	dichtschließend
DB	Deckenbalken
DDF	Dachdurchführung
dstür	dicht- und selbstschließend
EB	Elastisch gebetteter Balken
ELT	Elektroverteilung
FL	Fläche
F30	Feuerwiderstandsfähigkeit 30min (feuerhemmend)
F60	Feuerwiderstandsfähigkeit 60min (hochfeuerhemmend)
F90	Feuerwiderstandsfähigkeit 90min (feuerbeständig)
GR	Grundriss
H	Höhe
HK	Heizkörper
HKV	Heizkreisverteiler
HT	Haustechnik
IW	Installationswand
LÜ	Lüftung
OK	Oberkante
OKFFB	Oberkante Fertigfußboden
OKG	Oberkante Gelände
OL	Oberlicht
RB	Ringbalken
RFR	Regenfallrohr
rs	rauchdicht
RR	Regenrinne
RA	Rauchabzug
RH	Raumhoch
RW	Rettungsweg
SN	Schnitt
T30	Tür feuerhemmend
T30 rs	Tür feuerhemmend, rauchdicht selbstschließend
T90	Tür feuerbeständig
T90 rs	Tür feuerbeständig, rauchdicht selbstschließend
TRH	Traufhöhe
TW	Trennwand
UB	unbewehrte Frostschrünze
UK	Unterkante
US	Unterschnitt
UZ	Unterzug
ÜZ	Überzug
VSS	Vorsatzschale
WE	Wohnheit
Wfl	Wohnfläche
wmb	widerstandsfähig gegen mechanische Beanspruchung
	verdeckte Element Unterzug, Sparren, usw.
	Mauerwerk Bestand
	Dämmung
	Abriss Wand
	Mauerwerk Porenbeton
	Mauerwerk Kalksandstein
	Trockenbau-Innenwände (innerhalb Wohnheit), gem. Schallschutz und Brandschutz (Montage gemäß Herstellerangaben, z.B. Knauf W112 o.g.w.)
	Außenwände in Holztafelbauweise mit Faserzementtafeln oder Holz Verkleidung gem. Schallschutz und Brandschutz
	Stahlbeton
	Beton
T30rs	Brandschutzanforderungen
Pos 01.1	Positionsnr., Angaben siehe Statik
B3.1.18.F1	Positionsnr., Fenster / Türen
	Durchbruch

HINWEIS zur PLANUNG

Dieser Plan gilt nur in Verbindung mit den Ausführungsdetails.
Für alle Ausführungs- bzw. Anschlussdetails siehe aktuellen Detailplansatz. Fenster- und Türenlisten sind zu beachten.
Diese Planung gilt in Verbindung mit dem Ausstattungskatalog.

Die Anwendbarkeit der Detailzeichnung ist durch den Verarbeiter vor Ort an Hand der tatsächlichen Gegebenheiten zu Prüfen. Die Technischen Merkblätter der Hersteller und Systemzulassungen sind zu beachten!

Alle Maße und Zeichnungsmaße sind am Bau von der auszuführenden Firma eigenverantwortlich zu prüfen.
Der Ausführende ist verpflichtet, den Auftraggeber auf etwaige Unstimmigkeiten der Ausführungsunterlagen hinzuweisen.
(VOB/B §3 nr.3)

HINWEIS CAD-Zeichnung

Die Erstellung der vorliegenden Planungsunterlagen (GNEISE, basiert auf der durch CAD KON und der Schenck Gruppe übergebenen CAD-Zeichnung.
Höhenangaben zu den jeweiligen Hausnummern sind dem amtlichen Lageplan zu entnehmen. Die in den Schnitten dargestellte Höhe (x) entspricht der im Lageplan zu entnehmende Höhenkote Gelände / OKFFB EG an Einzelaufgang.

Alle Maße sind am Bau zu prüfen!

Lageplan

Bauherr

Albert Immo 4 S.ö.r.l.
8d, rue Collart, 8414 Steinfort
Luxemburg

Bauvorhaben

**Dachgeschoss-Neubau (Bauteil 1) und
Neubau Seitenflügel-Erweiterung (Bauteil 2.1) /
Reihenhäuser (Bauteil 2.2) / Remise (Bauteil 2.3)**

Kreuzstraße 14 in 13187 Berlin, Pankow

Architekten/Ingenieure

GNEISE
Planungs- und Beratungsgesellschaft

GNEISE
Dipl.-Ing. E.-R. Frevert-Henske
Planungs- und Beratungsgesellschaft mbH

Kiehlholzstraße 176, 12437 Berlin
Tel. 030 536 01-0
Fax 030 536 01-333

Planinhalt

Ausführungsplanung

Schnitt D-D

Bauteile 2.1, 2.2 + B2.3 Neubau

Kreuzstraße 14 in 13187 Berlin, Pankow

C	-	-	-
B	-	-	-
A	01.03.2022	AE	SF Erweiterung, Fensterhöhen
Index	Datum	Gez	Änderung

Datum:	30.11.2021	Maßstab:	1:50
Bearbeitung:	AE	Projektnummer:	19049
Blattgröße:	830x297	Zeichnungsnr.:	KRE14_AP-19049-SN-B2.1.2-5.1

Plotted by Gneise Schutzvermerk nach DIN 34 beachten!