


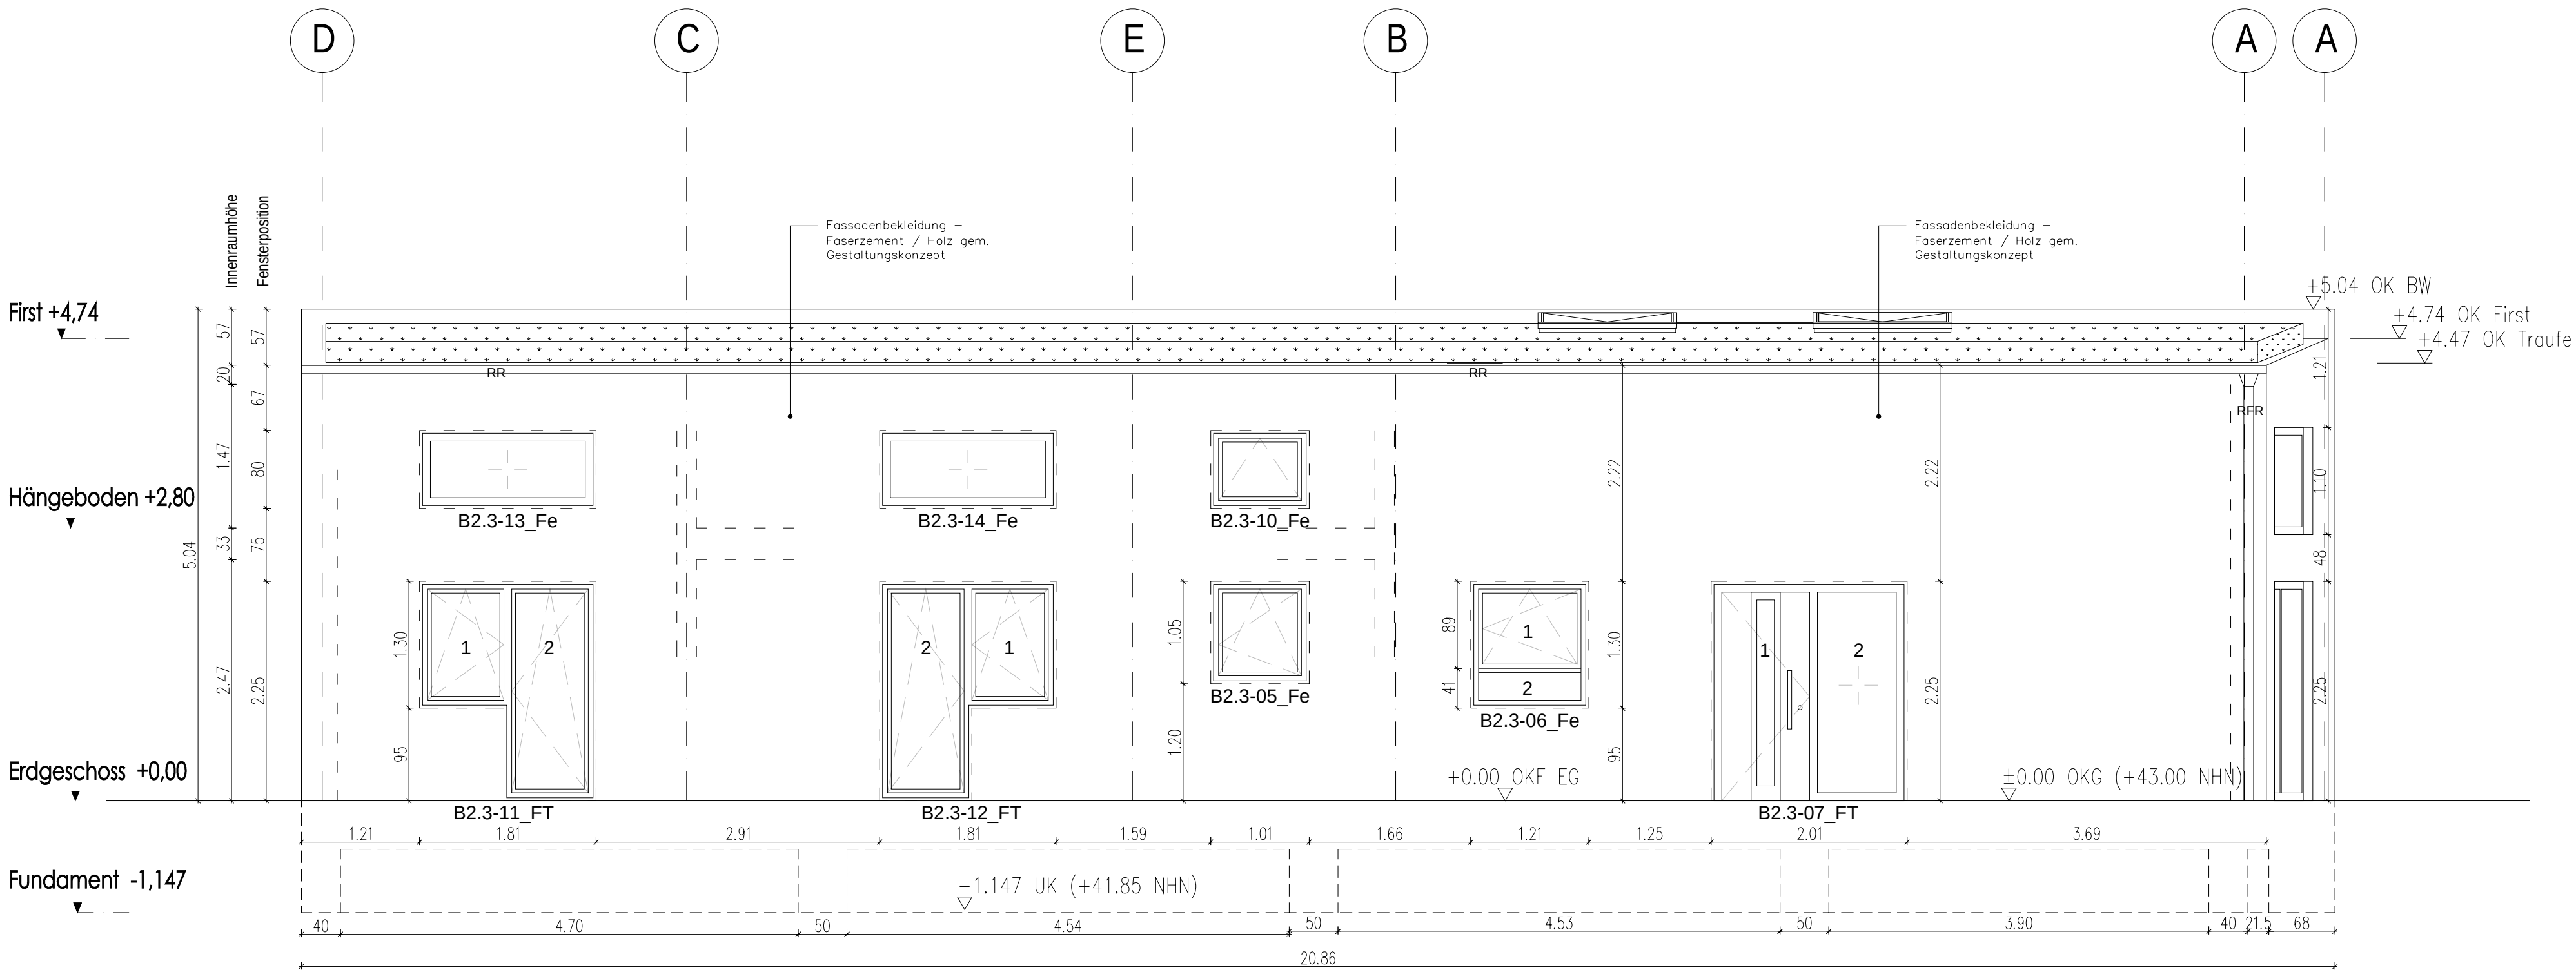

Ansicht B2.3 - Norden

LEGENDE

- AHD abgehängte Decke
- AN Ansicht
- AW Abwasser
- BDW Badewanne
- BRH Brüstungshöhe ab OKFF
- BW Brandwand
- BS Balkenschuh
- d dichtschließend
- DB Deckenbalken
- DDF Dachdurchführung
- dstür dicht- und selbstschließend
- EB Elastisch gebetteter Balken
- ELT Elektrounterverteilung
- FL Fläche
- F30 Feuerwiderstandsfähigkeit 30min (feuerhemmend)
- F60 Feuerwiderstandsfähigkeit 60min (hochfeuerhemmend)
- F90 Feuerwiderstandsfähigkeit 90min (feuerbeständig)
- GR Grundriss
- H Höhe
- HK Heizkörper
- HKV Heizkreisverteiler
- HT Haustechnik
- IW Installationswand
- LÜ Lüftung
- OK Oberkante
- OKFFB Oberkante Fertigfußboden
- OKG Oberkante Gelände
- OL Oberlicht
- RB Ringbalken
- RFR Regenfallrohr
- rs rauchdicht
- RR Regenrinne
- RA Rauchabzug
- RH Raumhoch
- RW Rettungsweg
- SN Schnitt
- T30 Tür feuerhemmend
- T30 rs Tür feuerhemmend, rauchdicht selbstschließ.
- T90 Tür feuerbeständig
- T90 rs Tür feuerbeständig, rauchdicht selbstschließ.
- TRH Traufhöhe
- TW Trennwand
- UB unbewehrte Frostschräge
- UK Unterkante
- US Unterschnitt
- UZ Unterzug
- ÜZ Überzug
- VSS Vorsatzschale
- WE Wohneinheit
- Wfl Wohnfläche
- wmb widerstandsfähig gegen mechanische Beanspruchung
- verdeckte Element Unterzug, Sparren, usw.
- Mauerwerk Bestand
- Dämmung
- Abriss Wand
- Mauerwerk Porenbeton
- Mauerwerk Kalksandstein
- Trockenbau-Innenwände (innerhalb Wohneinheit), gem. Schallschutz und Brandschutz (Montage gemäß Herstellerangaben, z.B. Knauf W112 o.glw.)
- Außenwände in Holztafelbauweise mit Faserzementtafen oder Holz Verkleidung gem. Schallschutz und Brandschutz
- Stahlbeton
- Beton
- Brandschutzanforderungen
- Positionennummern, Angaben siehe Statik
- Positionennummern, Fenster / Türen
- Durchbruch

HINWEIS zur PLANUNG

Dieser Plan gilt nur in Verbindung mit den Ausführungsdetails.
Für alle Ausführungs- bzw. Anschlussdetails siehe aktuellen
Detailplansatz. Fenster- und Türenlisten sind zu beachten.
Diese Planung gilt in Verbindung mit dem Ausstattungskatalog.


Die Anwendbarkeit der Detailzeichnung ist durch den
Verarbeiter vor Ort an Hand der tatsächlichen Gegebenheiten zu
Prüfen. Die Technischen Merkblätter der Hersteller und
Systemzulassungen sind zu beachten!

Alle Maße und Zeichnungsmaße sind am Bau von der
auszuführenden Firma eigenverantwortlich zu prüfen.
Der Ausführende ist verpflichtet, den Auftraggeber auf etwaige
Unstimmigkeiten der Ausführungsunterlagen hinzuweisen.
(VOB/B §3 nr.3)

HINWEIS CAD-Zeichnung

Die Erstellung der vorliegenden Planungsunterlagen (GNEISE, basiert auf
der durch CAD KON und der Scherbeck Gruppe übergebenen
CAD-Zeichnung
Höhenangaben zu den jeweiligen Hausnummern sind dem amtlichen
Lageplan zu entnehmen. Die in den Schnitten dargestellte Höhe (x)
entspricht der im Lageplan zu entnehmende Höhenkote Gelände /
OKFFBEG am Einzelaufgang.

Alle Maße sind am Bau zu prüfen!

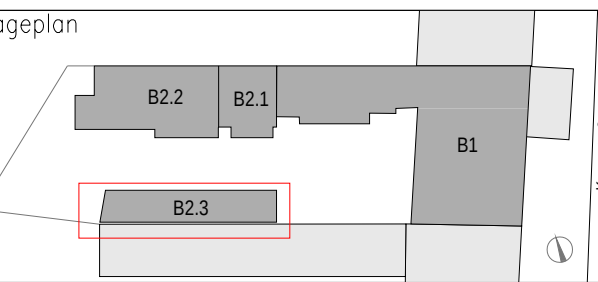

Bauherr

Albert Immo 4 S.ä.r.l.
8d, rue Collart, 8414 Steinfort
Luxemburg

Bauvorhaben
**Dachgeschoss-Neubau (Bauteil 1) und
Neubau Seitenflügel-Erweiterung (Bauteil 2.1) /
Reihenhäuser (Bauteil 2.2) / Remise (Bauteil 2.3)**

Kreuzstraße 14 in 13187 Berlin, Pankow

Architekten/Ingenieure
GNEISE
Planungs- und Beratungsgesellschaft

GNEISE
Dipl.-Ing. E.-R. Frevert-Henske
Planungs- und Beratungsgesellschaft mbH

Kiehlholzstraße 176, 12437 Berlin
Tel. 030 536 01-0
Fax 030 536 01-333

Planinhalt
Ausführungsplanung
Ansicht Nord
Bauteile 2.3 - Neubau
Kreuzstraße 14 in 13187 Berlin, Pankow

C	-	-	-
B	-	-	-
A	01.03.2022	AE	SF Erweiterung, Fensterhöhen
Index	Datum	Gez	Änderung

Datum:	Maßstab:
30.11.2021	1:50
Bearbeitung:	Projektnummer:
AE	19049
Blattgröße:	Zeichnungsnr.
830x297	KRE14_AP-19049-AN-B2.3-6.0

Plotted by Gneise Schutzvermerk nach DIN 34 beachten!

Vorabzug