

LEGENDE

- AHD abgehängte Decke
AN Ansicht
AW Abwasser
BDW Badewanne
BRH Brüstungshöhe ab OKFF
BW Brandwand
BS Balkenschuh
d dichtschließend
DB Deckenbalken
DDF Dachdurchführung
dstür dicht- und selbstschließend
EB Elastisch gebetteter Balken
ELT Elektrounterverteilung
FL Fläche
F30 Feuerwiderstandsfähigkeit 30min (feuerhemmend)
F60 Feuerwiderstandsfähigkeit 60min (hochfeuerhemmend)
F90 Feuerwiderstandsfähigkeit 90min (feuerbeständig)
GR Grundriss
H Höhe
HK Heizkörper
HKV Heizkreisverteiler
HT Haustechnik
IW Installationswand
LÜ Lüftung
OK Oberkante
OKFFB Oberkante Fertigfußboden
OKG Oberkante Gelände
OL Oberlicht
RB Ringbalken
RFR Regenfallrohr
rs rauchdicht
RR Regenrinne
RA Rauchabzug
RH Raumhoch
RW Rettungsweg
SN Schnitt
T30 Tür feuerhemmend
T30 rs Tür feuerhemmend, rauchdicht selbstschließ.
T90 Tür feuerbeständig
T90 rs Tür feuerbeständig, rauchdicht selbstschließ.
TRH Traufhöhe
TW Trennwand
UB unbewehrte Frostschürze
UK Unterkante
UZ Unterzug
ÜZ Überzug
VSS Vorsatzschale
WE Wohneinheit
Wfl Wohnfläche
wmB widerstandsfähig gegen mechanische Beanspruchung
verdeckte Element Unterzug, Sparren, usw.
Mauerwerk Bestand
Dämmung
Abriss Wand
Mauerwerk Porenbeton
Mauerwerk Kalksandstein
Trockenbau-Innenwände (innerhalb Wohneinheit), gem. Schallschutz und Brandschutz (Montage gemäß Herstellerangaben, z.B. Knuf W112 o.glw.)
Außenwände in Holztafelbauweise mit Faserzementtafen oder Holz Verkleidung gem. Schallschutz und Brandschutz
Stahlbeton
Beton
Brandschutzanforderungen
Positionennummern, Angaben siehe Statik
Positionennummern, Fenster / Türen
Durchbruch

HINWEIS zur PLANUNG

Dieser Plan gilt nur in Verbindung mit den Ausführungsdetails
Für alle Ausführungs- bzw. Anschlussdetails siehe aktuellen
Detailplansatz Fenster- und Türenlisten sind zu beachten
Diese Planung gilt in Verbindung mit dem Ausstattungskatalog


Die Anwendbarkeit der Detailzeichnung ist durch den
Verarbeiter vor Ort an Hand der tatsächlichen Gegebenheiten zu
Prüfen Die Technischen Merkblätter der Hersteller und
Systemzulassungen sind zu beachten!

Alle Maße und Zeichnungsmaße sind am Bau von der
auszuführenden Firma eigenverantwortlich zu prüfen
Der Ausführende ist verpflichtet, den Auftraggeber auf etwaige
Unstimmigkeiten der Ausführungsunterlagen hinzuweisen.
(VOB/B §3 nr.3)

HINWEIS CAD-Zeichnung

Die Erstellung der vorliegenden Planungsunterlage (GNEISE, basiert auf
der durch CAD KON und der Schernbeck Gruppe übergebenen
CAD-Zeichnung
Höhenangaben zu den jeweiligen Hausnummern sind dem amtlichen
Lageplan zu entnehmen. Die in den Schnitten dargestellte Höhe (x) entspricht der im Lageplan zu entnehmende Höhenkote Gelände /
OKFFBEG am Einzelaufgang.

Alle Maße sind am Bau zu prüfen!

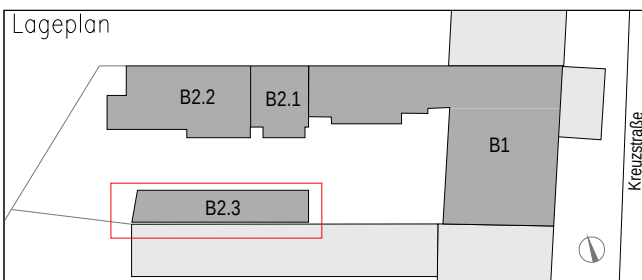

Bauherr

Albert Immo 4 S.ö.r.l.
8d, rue Collart, 8414 Steinfort
Luxemburg

Bauvorhaben
**Dachgeschoss-Neubau (Bauteil 1) und
Neubau Seitenflügel-Erweiterung (Bauteil 2.1) /
Reihenhäuser (Bauteil 2.2) / Remise (Bauteil 2.3)**

Kreuzstraße 14 in 13187 Berlin, Pankow

Architekten/Ingenieure
GNEISE
Planungs- und Beratungsgesellschaft


GNEISE Dipl.-Ing. E.-R. Frevert-Henske
Planungs- und Beratungsgesellschaft mbH
Kiehlholzstraße 176, 12437 Berlin
Tel. 030 536 01-0
Fax 030 536 01-333

Planinhalt
**Ausführungsplanung
Ansicht Ost, West
Bauteile 2.3 - Neubau**
Kreuzstraße 14 in 13187 Berlin, Pankow

C	-	-	-
B	-	-	-
A	01.03.2022	AE	SF Erweiterung, Fensternhöhen
Index	Datum	Gez	Änderung

Datum:	Maßstab:
30.11.2021	1:50
Bearbeitung:	Projektnummer:
AE	19049
Blattgröße:	Zeichnungsnr.
830x297	KRE14_AP-19049-AN-B2.3-6.1

Plotted by Gneise Schutzvermerk nach DIN 34 beachten!

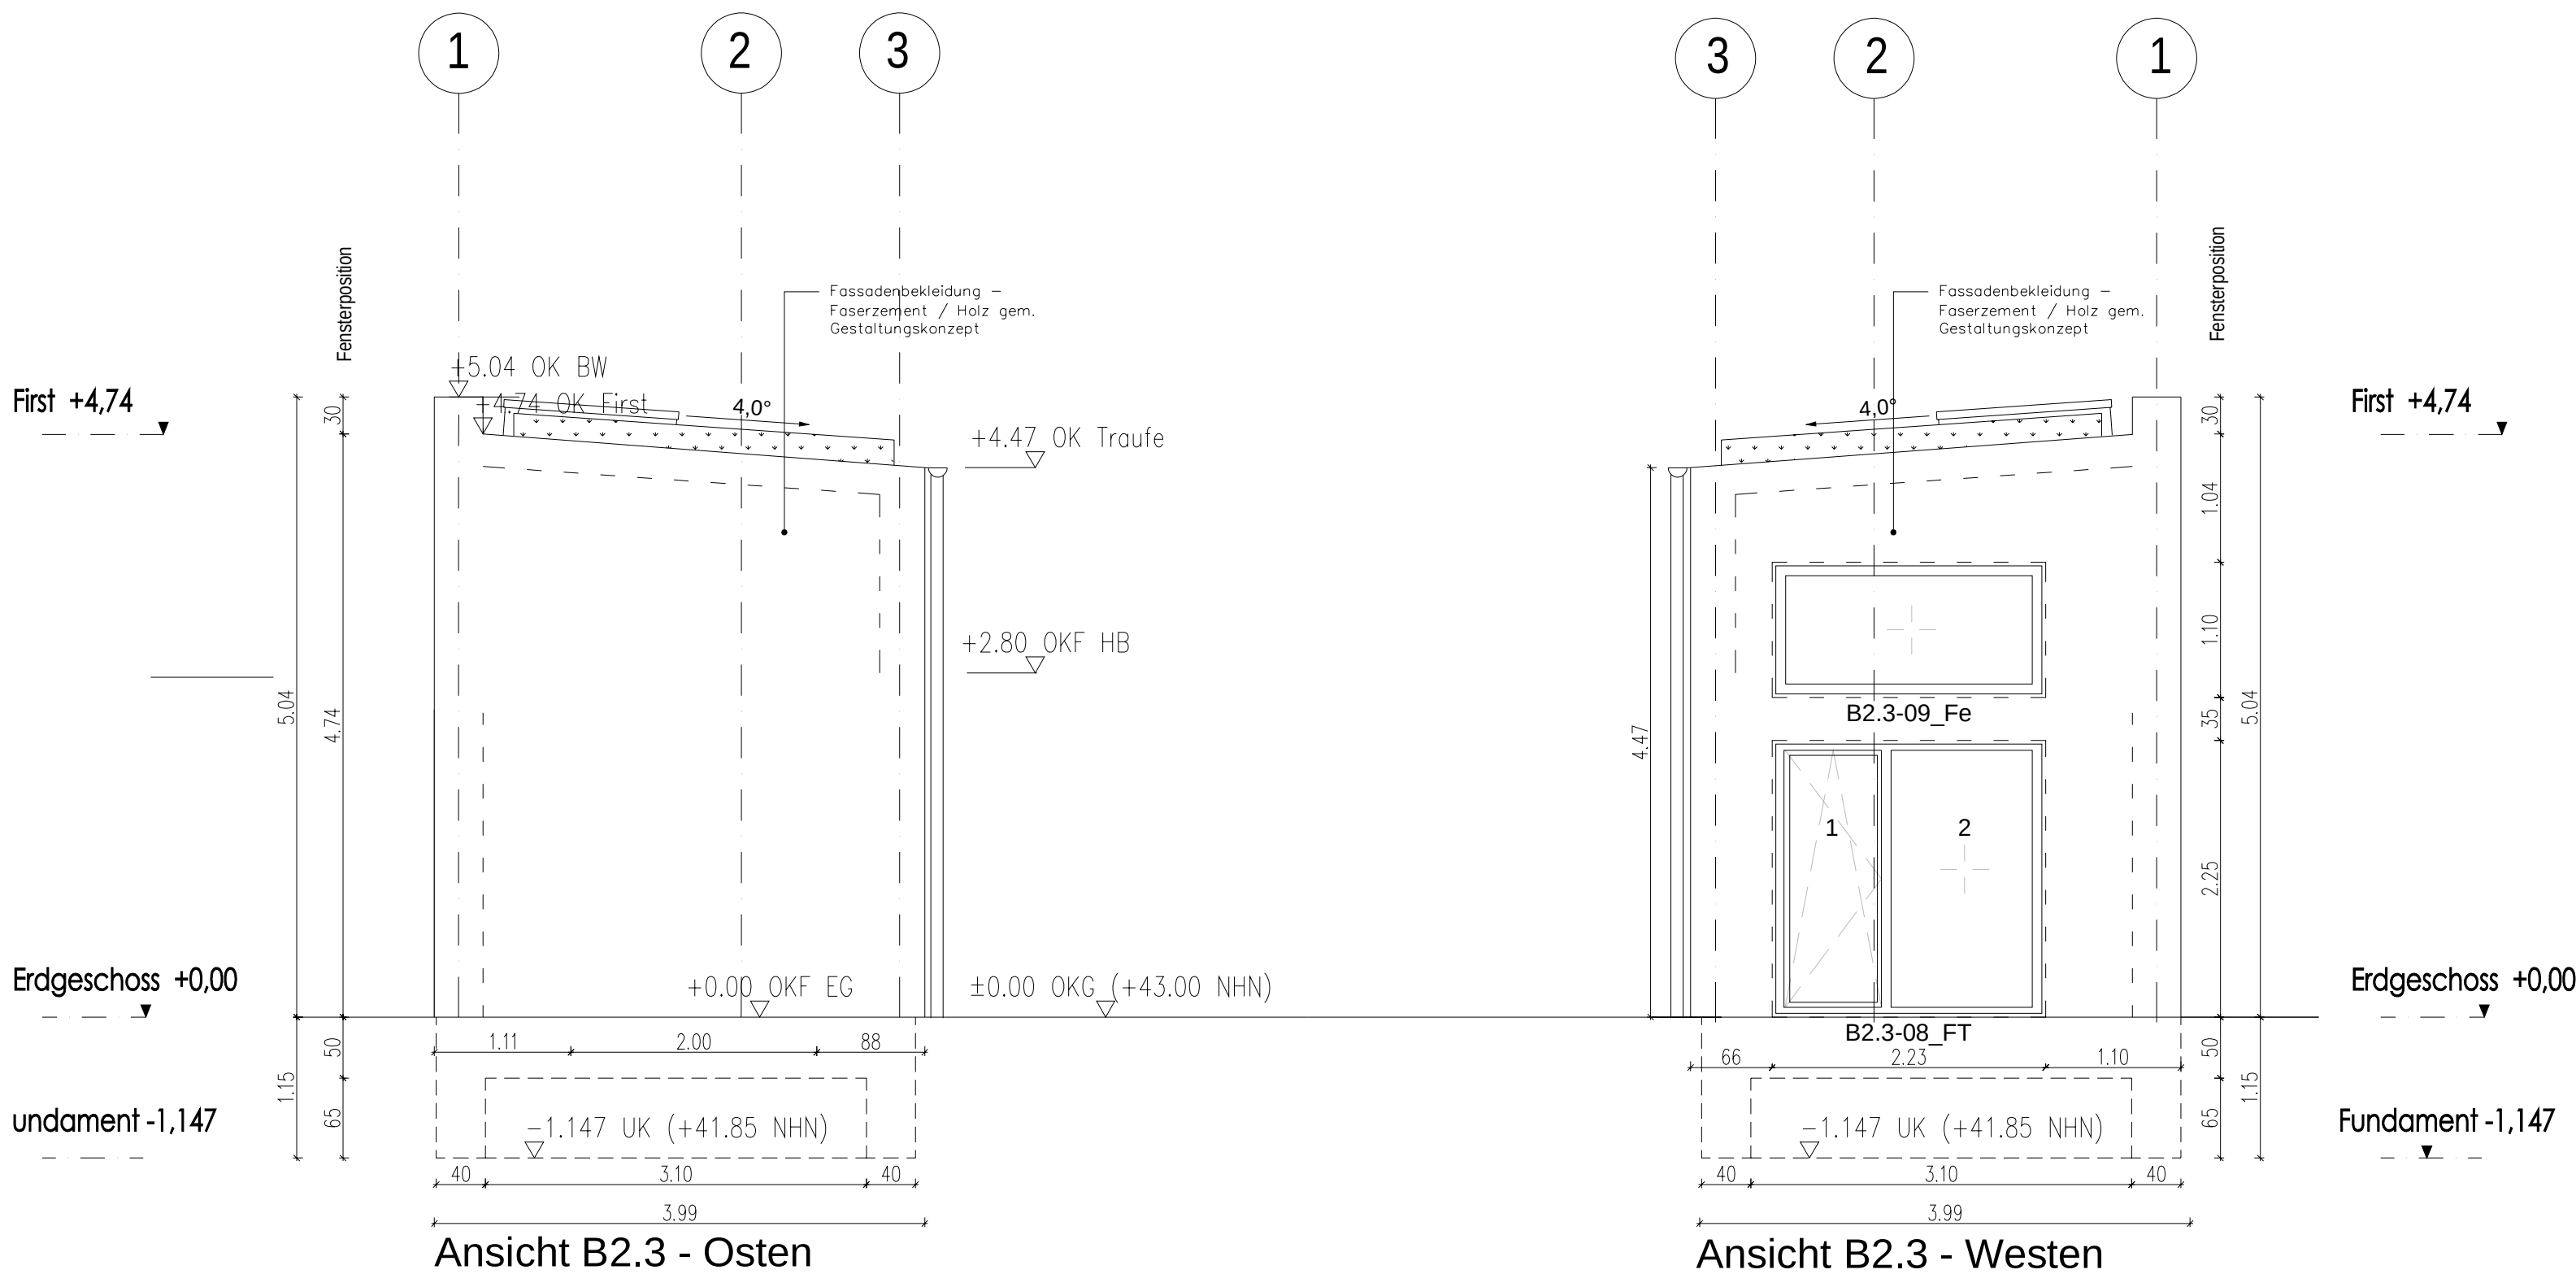

Vorabzug