


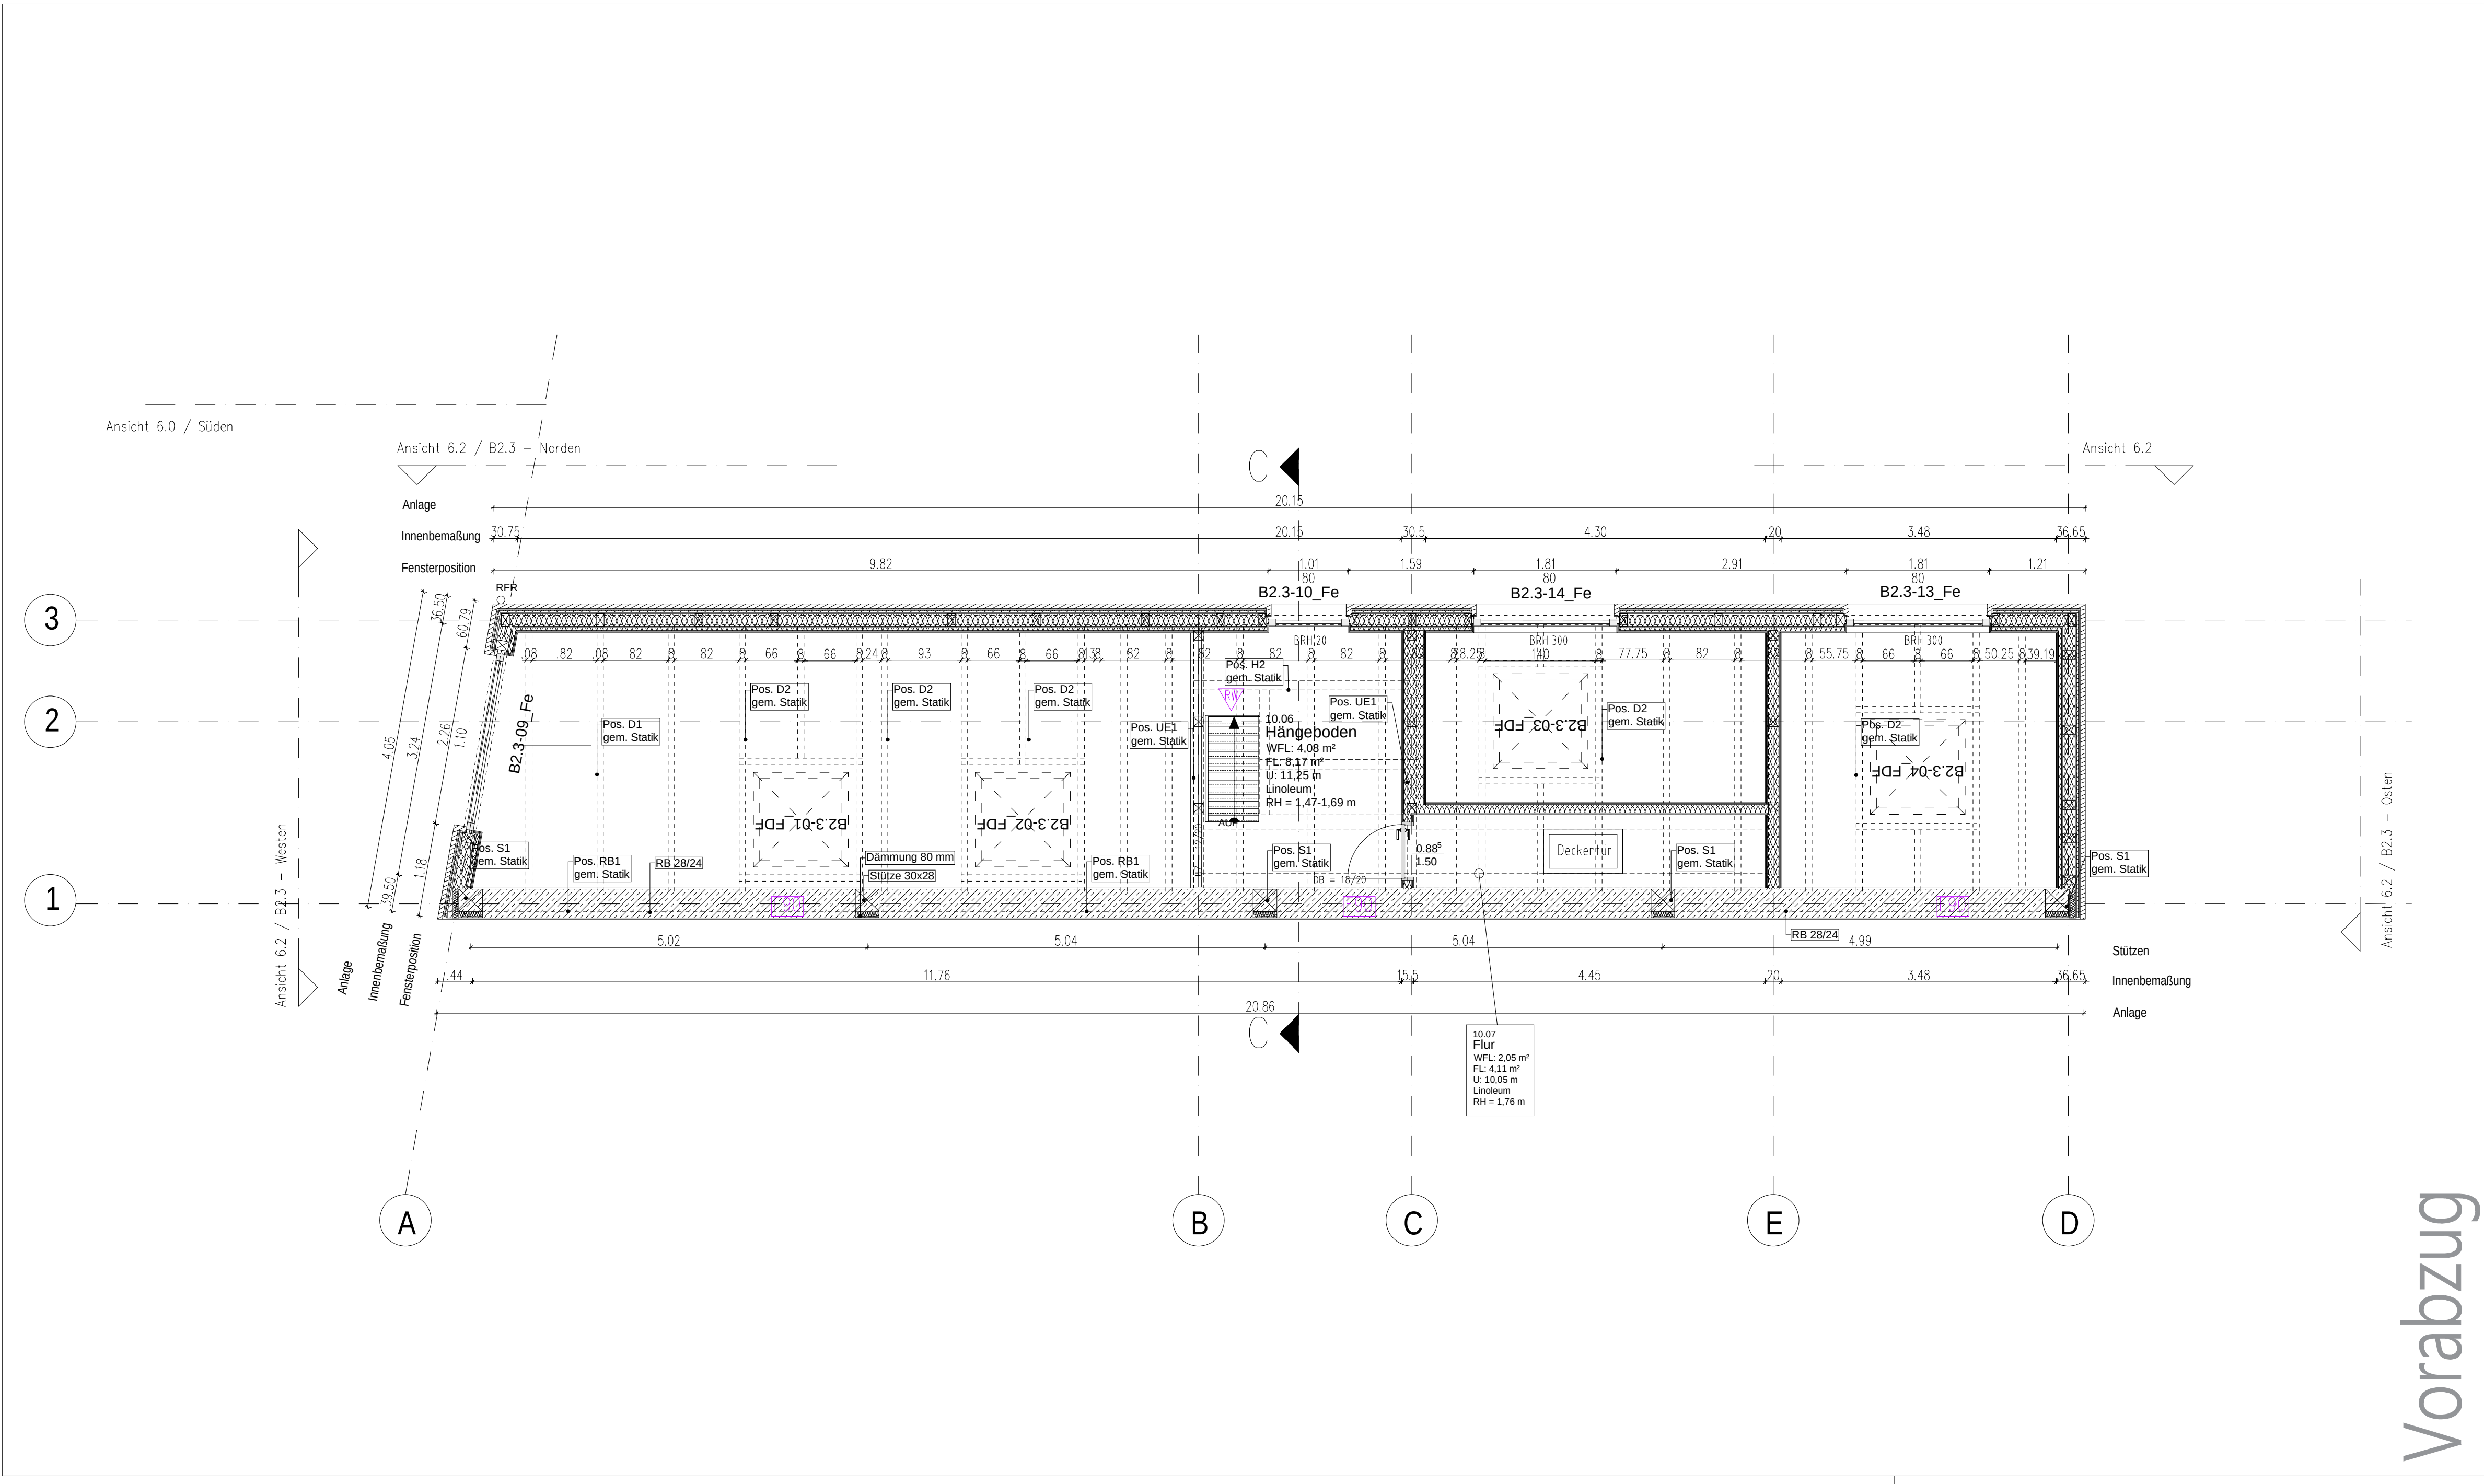

LEGENDE

AHD

abgehängte Decke

AN

Ansicht

AW

Abwasser

BDW

Badewanne

BRH

Brüstungshöhe ab OKFF

BW

Brandwand

BS

Balkenschuh

d

dichtschließend

DB

Deckenbalken

DDF

Dochdurchführung

dstür

dicht- und selbstschließend

EB

Elastisch gebetteter Balken

ELT

Elektrounterverteilung

FL

Fläche

F30

Feuerwiderstandsfähigkeit 30min (feuerhemmend)

F60

Feuerwiderstandsfähigkeit 60min (hochfeuerhemmend)

F90

Feuerwiderstandsfähigkeit 90min (feuerbeständig)

GR

Grundriss

H

Höhe

HK

Heizkörper

HKV

Heizkreisverteiler

HT

Haustechnik

IW

Installationswand

LÜ

Lüftung

OK

Oberkante

OKFFB

Oberkante Fertigfußboden

OKG

Oberkante Gelände

OL

Oberlicht

RB

Ringbalken

RFR

Regenfallrohr

rs

rauchdicht

RR

Regenrinne

RA

Rauchabzug

RH

Raumhoch

RW

Rettungsweg

SN

Schnitt

T30

Tür feuerhemmend

T30 rs

Tür feuerhemmend, rauchdicht selbstschließend

T90

Tür feuerbeständig

T90 rs

Tür feuerbeständig, rauchdicht selbstschließend

TRH

Traufhöhe

TW

Trennwand

UB

unbewehrte Frostschräge

UK

Unterkannte

US

Unterschnitt

UZ

Unterzug

ÜZ

Überzug

VSS

Vorsatzschale

WE

Wohneinheit

Wfl

Wohnfläche

wmb

widerstandsfähig gegen mechanische Beanspruchung

verdeckte Element

Unterzug, Sparren, usw.

Mauerwerk Bestand

Dämmung

Abriss Wand

Mauerwerk Porenbeton

Mauerwerk Kalksandstein

Trockenbau-Innenwände (innerhalb Wohneinheit), gem. Schallschutz und Brandschutz (Montage gemäß Herstellerangaben, z.B. Knaf W112 o.g.lw.)

Außenwände in Holztafelbauweise mit Faserzementtafeln oder Holz Verkleidung gem. Schallschutz und Brandschutz

Stahlbeton

Beton

Brandschutzanforderungen

Positionennummern, Angaben siehe Statik

Positionennummern, Fenster / Türen

Durchbruch

HINWEIS zur PLANUNG

Dieser Plan gilt nur in Verbindung mit den Ausführungsdetails.
Für alle Ausführungs- bzw. Anschlussdetails siehe aktuellen Detailplansatz. Fenster- und Türenlisten sind zu beachten.
Diese Planung gilt in Verbindung mit dem Ausstattungskatalog.

Die Anwendbarkeit der Detailzeichnung ist durch den Verarbeiter vor Ort an Hand der tatsächlichen Gegebenheiten zu Prüfen. Die Technischen Merkblätter der Hersteller und Systemzulassungen sind zu beachten!

Alle Maße und Zeichnungsmaße sind am Bau von der auszuführenden Firma eigenverantwortlich zu prüfen.
Der Ausführende ist verpflichtet, den Auftraggeber auf etwaige Unstimmigkeiten der Ausführungsunterlagen hinzuweisen.
(VOB/B §3 nr. 3)

HINWEIS CAD-Zeichnung

Die Erstellung der vorliegenden Planungsunterlagen (GNEISE, basiert auf der durch CAD KON und der Scherneck Gruppe übergebenen CAD-Zeichnung.
Hohenangaben zu den jeweiligen Hausnummern sind dem amtlichen Lageplan zu entnehmen. Die in den Schnitten dargestellte Höhe (x) entspricht der im Lageplan zu entnehmende Höhenkote Gelände / OKFFBEG am Einzelaufgang.

Alle Maße sind am Bau zu prüfen!

Lageplan

Bauherr

Albert Immo 4 S.ä.r.l.
8d, rue Collart, 8414 Steinfort
Luxemburg

Bauvorhaben

Dachgeschoss-Neubau (Bauteil 1) und
Neubau Seitenflügel-Erweiterung (Bauteil 2.1) /
Reihenhäuser (Bauteil 2.2) / Remise (Bauteil 2.3)

Kreuzstraße 14 in 13187 Berlin, Pankow

Architekten/Ingenieure

GNEISE

Planungs- und Beratungsgesellschaft

GNEISE

Dipl.-Ing. E.-R. Frevert-Henske

Planungs- und Beratungsgesellschaft mbH

Kiehlholzstraße 176, 12437 Berlin

Tel. 030 536 01-0

Fax 030 536 01-333

Planinhalt

C	-	-	-
B	-	-	-
A	01.03.2022	AE	SF Erweiterung, Fensterhöhen
Index	Datum	Gez	Änderung

Ausführungsplanung

1. Obergeschoss

Bauteile 2.3 - Neubau

Kreuzstraße 14 in 13187 Berlin, Pankow

Datum:	30.11.2021	Maßstab:	1:50
Bearbeitung:	AE	Projektnummer:	19049
Blattgröße:	850x400	Zeichnungs-nr.	KRE14_AP-19049-GR-B2.3-4.1

Plotted by Gneise

Schutzvermerk nach DIN 34 beachten!

Diese Zeichnung ist urheberrechtlich geschützt. Bei Weitergabe -auch auszugsweise- ist die Gneise Planungs- und Beratungsgesellschaft mbH als Urheber auf dem Plan zu vermerken!