


AUSFÜHRUNGSPLANUNG**VORABZUG****Bauteil 2.3****Stand:** 01.03.2022**INDEX:** A

Bauvorhaben: Dachgeschoss-Neubau (Bauteil 1) und
Neubau Seitenflügel-Erweiterung (Bauteil 2.1) /
Reihenhäuser (Bauteil 2.2) / Remise (Bauteil 2.3)

Kreuzstraße 14
13187 Berlin

Bauherr: Albert Immo 4 S.à.r.l.
8d, Rue Collart
8414 Steinfort
Luxemburg

Zeichnungs-Nr.			Inhalt	Maßstab	Datum	Index
Ansichten						
LP5	19049	KRE14_AP-19049-AN-B2.3-6.0	Ansicht Nord	1:50	01.03.2022	A
LP5	19049	KRE14_AP-19049-AN-B2.3-6.1	Ansicht Ost, West	1:50	01.03.2022	A
LP5	19049	KRE14_AP-19049-DA-B2.3-1.0	Dachaufsicht	1:50	01.03.2022	A
Grundrisse						
LP5	19049	KRE14_AP-19049-GR-B2.3-4.0	Erdgeschoss	1:50	01.03.2022	A
LP5	19049	KRE14_AP-19049-GR-B2.3-4.1	1. Obergeschoss	1:50	01.03.2022	A
LP5	19049	KRE14_AP-19049-DA-B2.3-1.1	Gründung	1:50	01.03.2022	A
Schnitte						
LP5	19049	KRE14 AP-19049-SN-B2.3-5.0	Schnitt C	1:50	01.03.2022	A

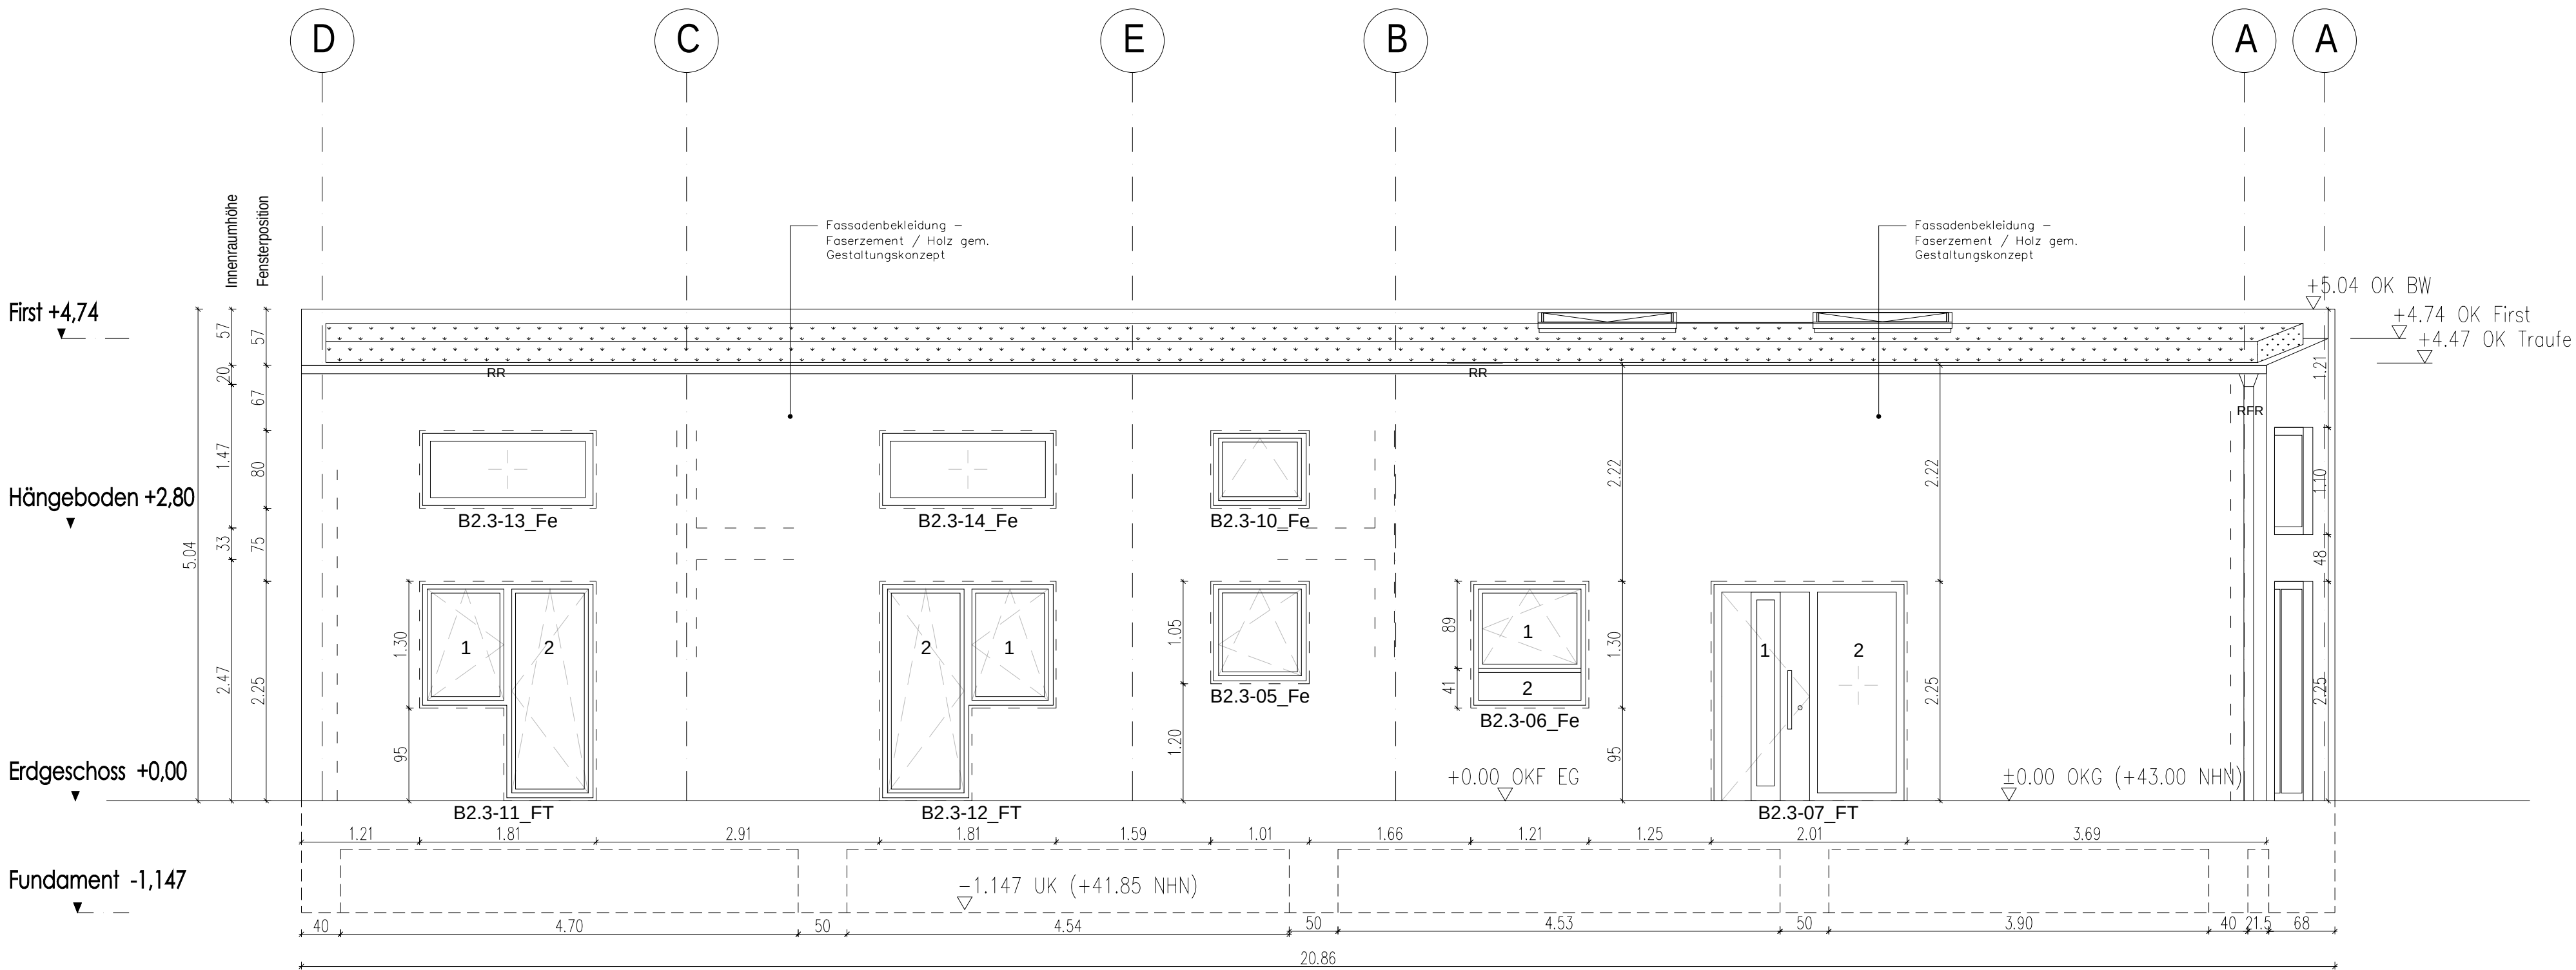

Ansicht B2.3 - Norden

LEGENDE

- AHD abgehängte Decke
- AN Ansicht
- AW Abwasser
- BDW Badewanne
- BRH Brüstungshöhe ab OKFF
- BW Brandwand
- BS Balkenschuh
- d dichtschießend
- DB Deckenbalken
- DDF Dachdurchführung
- dstür dicht- und selbstschließend
- EB Elastisch gebetteter Balken
- ELT Elektrounterverteilung
- FL Fläche
- F30 Feuerwiderstandsfähigkeit 30min (feuerhemmend)
- F60 Feuerwiderstandsfähigkeit 60min (hochfeuerhemmend)
- F90 Feuerwiderstandsfähigkeit 90min (feuerbeständig)
- GR Grundriss
- H Höhe
- HK Heizkörper
- HKV Heizkreisverteiler
- HT Haustechnik
- IW Installationswand
- LÜ Lüftung
- OK Oberkante
- OKFFB Oberkante Fertigfußboden
- OKG Oberkante Gelände
- OL Oberlicht
- RB Ringbalken
- RFR Regenfallrohr
- rs rauchdicht
- RR Regenrinne
- RA Rauchabzug
- RH Raumhoch
- RW Rettungsweg
- SN Schnitt
- T30 Tür feuerhemmend
- T30 rs Tür feuerhemmend, rauchdicht selbstschließ.
- T90 Tür feuerbeständig
- T90 rs Tür feuerbeständig, rauchdicht selbstschließ.
- TRH Traufhöhe
- TW Trennwand
- UB unbewehrte Frostschräge
- UK Unterkante
- US Unterschnitt
- UZ Unterzug
- ÜZ Überzug
- VSS Vorsatzschale
- WE Wohneinheit
- Wfl Wohnfläche
- wmb widerstandsfähig gegen mechanische Beanspruchung
- verdeckte Element Unterzug, Sparren, usw.
- Mauerwerk Bestand
- Dämmung
- Abriss Wand
- Mauerwerk Porenbeton
- Mauerwerk Kalksandstein
- Trockenbau-Innenwände (innerhalb Wohneinheit), gem. Schallschutz und Brandschutz (Montage gemäß Herstellerangaben, z.B. Knaf W112 o.glw.)
- Außenwände in Holztafelbauweise mit Faserzementtafeln oder Holz Verkleidung gem. Schallschutz und Brandschutz
- Stahlbeton
- Beton
- Brandschutzanforderungen
- Positionennummern, Angaben siehe Statik
- Positionennummern, Fenster / Türen
- Durchbruch

HINWEIS zur PLANUNG

Dieser Plan gilt nur in Verbindung mit den Ausführungsdetails.
Für alle Ausführungs- bzw. Anschlussdetails siehe aktuellen
Detailplansatz. Fenster- und Türenlisten sind zu beachten.
Diese Planung gilt in Verbindung mit dem Ausstattungskatalog.


Die Anwendbarkeit der Detailzeichnung ist durch den
Verarbeiter vor Ort an Hand der tatsächlichen Gegebenheiten zu
Prüfen. Die Technischen Merkblätter der Hersteller und
Systemzulassungen sind zu beachten!

Alle Maße und Zeichnungsmaße sind am Bau von der
auszuführenden Firma eigenverantwortlich zu prüfen.
Der Ausführende ist verpflichtet, den Auftraggeber auf etwaige
Unstimmigkeiten der Ausführungsunterlagen hinzuweisen.
(VOB/B §3 nr.3)

HINWEIS CAD-Zeichnung

Die Erstellung der vorliegenden Planungsunterlagen (GNEISE, basiert auf
der durch CAD KON und der Scherbeck Gruppe übergebenen
CAD-Zeichnung
Höhenangaben zu den jeweiligen Hausnummern sind dem amtlichen
Lageplan zu entnehmen. Die in den Schnitten dargestellte Höhe (x)
entspricht der im Lageplan zu entnehmende Höhenkote Gelände /
OKFFBEG am Einzelaufgang.

Alle Maße sind am Bau zu prüfen!

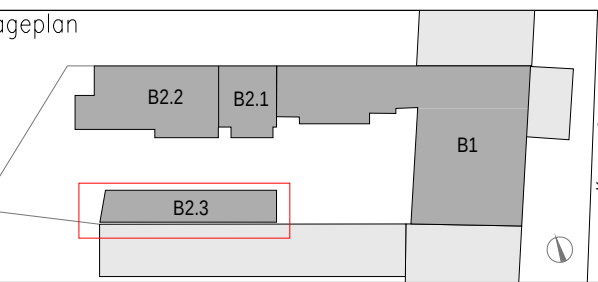

Bauherr

Albert Immo 4 S.ä.r.l.
8d, rue Collart, 8414 Steinfort
Luxemburg

Bauvorhaben
**Dachgeschoss-Neubau (Bauteil 1) und
Neubau Seitenflügel-Erweiterung (Bauteil 2.1) /
Reihenhäuser (Bauteil 2.2) / Remise (Bauteil 2.3)**

Kreuzstraße 14 in 13187 Berlin, Pankow

Architekten/Ingenieure
GNEISE
Planungs- und Beratungsgesellschaft

GNEISE
Dipl.-Ing. E.-R. Frevert-Henske
Planungs- und Beratungsgesellschaft mbH

Kiehlholzstraße 176, 12437 Berlin
Tel. 030 536 01-0
Fax 030 536 01-333

Planinhalt
Ausführungsplanung
Ansicht Nord
Bauteile 2.3 - Neubau
Kreuzstraße 14 in 13187 Berlin, Pankow

C	-	-	-
B	-	-	-
A	01.03.2022	AE	SF Erweiterung, Fensterhöhen
Index	Datum	Gez	Änderung

Datum:	Maßstab:
30.11.2021	1:50
Bearbeitung:	Projektnummer:
AE	19049
Blattgröße:	Zeichnungsnr.
830x297	KRE14_AP-19049-AN-B2.3-6.0

Plotted by Gneise Schutzvermerk nach DIN 34 beachten!

Vorabzug

LEGENDE

- AHD abgehängte Decke
AN Ansicht
AW Abwasser
BDW Badewanne
BRH Brüstungshöhe ab OKFF
BW Brandwand
BS Balkenschuh
d dichtschließend
DB Deckenbalken
DDF Dachdurchführung
dstür dicht- und selbstschließend
EB Elastisch gebetteter Balken
ELT Elektrounterverteilung
FL Fläche
F30 Feuerwiderstandsfähigkeit 30min (feuerhemmend)
F60 Feuerwiderstandsfähigkeit 60min (hochfeuerhemmend)
F90 Feuerwiderstandsfähigkeit 90min (feuerbeständig)
GR Grundriss
H Höhe
HK Heizkörper
HKV Heizkreisverteiler
HT Haustechnik
IW Installationswand
LÜ Lüftung
OK Oberkante
OKFFB Oberkante Fertigfußboden
OKG Oberkante Gelände
OL Oberlicht
RB Ringbalken
RFR Regenfallrohr
rs rauchdicht
RR Regenrinne
RA Rauchabzug
RH Raumhoch
RW Rettungsweg
SN Schnitt
T30 Tür feuerhemmend
T30 rs Tür feuerhemmend, rauchdicht selbstschließ.
T90 Tür feuerbeständig
T90 rs Tür feuerbeständig, rauchdicht selbstschließ.
TRH Traufhöhe
TW Trennwand
UB unbewehrte Frostschürze
UK Unterkante
UZ Unterzug
ÜZ Überzug
VSS Vorsatzschale
WE Wohneinheit
Wfl Wohnfläche
wmB widerstandsfähig gegen mechanische Beanspruchung
verdeckte Element Unterzug, Sparren, usw.
Mauerwerk Bestand
Dämmung
Abriss Wand
Mauerwerk Porenbeton
Mauerwerk Kalksandstein
Trockenbau-Innenwände (innerhalb Wohneinheit), gem. Schallschutz und Brandschutz (Montage gemäß Herstellerangaben, z.B. Knuf W112 o.glw.)
Außenwände in Holztafelbauweise mit Faserzementtafen oder Holz Verkleidung gem. Schallschutz und Brandschutz
Stahlbeton
Beton
Brandschutzanforderungen
Positionennummern, Angaben siehe Statik
Positionennummern, Fenster / Türen
Durchbruch

HINWEIS zur PLANUNG

Dieser Plan gilt nur in Verbindung mit den Ausführungsdetails
Für alle Ausführungs- bzw. Anschlussdetails siehe aktuellen
Detailplansatz Fenster- und Türenlisten sind zu beachten
Diese Planung gilt in Verbindung mit dem Ausstattungskatalog


Die Anwendbarkeit der Detailzeichnung ist durch den
Verarbeiter vor Ort an Hand der tatsächlichen Gegebenheiten zu
Prüfen Die Technischen Merkblätter der Hersteller und
Systemzulassungen sind zu beachten!

Alle Maße und Zeichnungsmaße sind am Bau von der
auszuführenden Firma eigenverantwortlich zu prüfen
Der Ausführende ist verpflichtet, den Auftraggeber auf etwaige
Unstimmigkeiten der Ausführungsunterlagen hinzuweisen.
(VOB/B §3 nr.3)

HINWEIS CAD-Zeichnung

Die Erstellung der vorliegenden Planungsunterlage (GNEISE, basiert auf
der durch CAD KON und der Schernbeck Gruppe übergebenen
CAD-Zeichnung
Höhenangaben zu den jeweiligen Hausnummern sind dem amtlichen
Lageplan zu entnehmen. Die in den Schnitten dargestellte Höhe (x) entspricht der im Lageplan zu entnehmende Höhenkote Gelände /
OKFFBEG am Einzelaufgang.

Alle Maße sind am Bau zu prüfen!

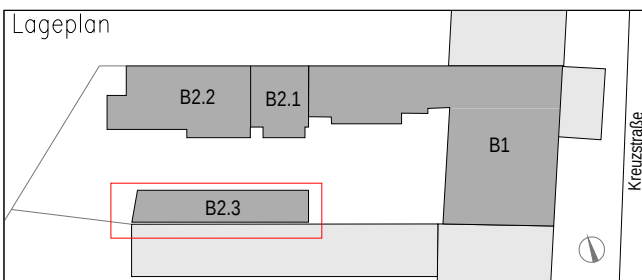

Bauherr

Albert Immo 4 S.ö.r.l.
8d, rue Collart, 8414 Steinfort
Luxemburg

Bauvorhaben
**Dachgeschoss-Neubau (Bauteil 1) und
Neubau Seitenflügel-Erweiterung (Bauteil 2.1) /
Reihenhäuser (Bauteil 2.2) / Remise (Bauteil 2.3)**

Kreuzstraße 14 in 13187 Berlin, Pankow

Architekten/Ingenieure
GNEISE
Planungs- und Beratungsgesellschaft


GNEISE Dipl.-Ing. E.-R. Frevert-Henske
Planungs- und Beratungsgesellschaft mbH
Kiehlholzstraße 176, 12437 Berlin
Tel. 030 536 01-0
Fax 030 536 01-333

Planinhalt
**Ausführungsplanung
Ansicht Ost, West
Bauteile 2.3 - Neubau**
Kreuzstraße 14 in 13187 Berlin, Pankow


C	-	-	-
B	-	-	-
A	01.03.2022	AE	SF Erweiterung, Fensternhöhen
Index	Datum	Gez	Änderung

Datum:	Maßstab:
30.11.2021	1:50
Bearbeitung:	Projektnummer:
AE	19049
Blattgröße:	Zeichnungsnr.
830x297	KRE14_AP-19049-AN-B2.3-6.1

Plotted by Gneise Schutzvermerk nach DIN 34 beachten!

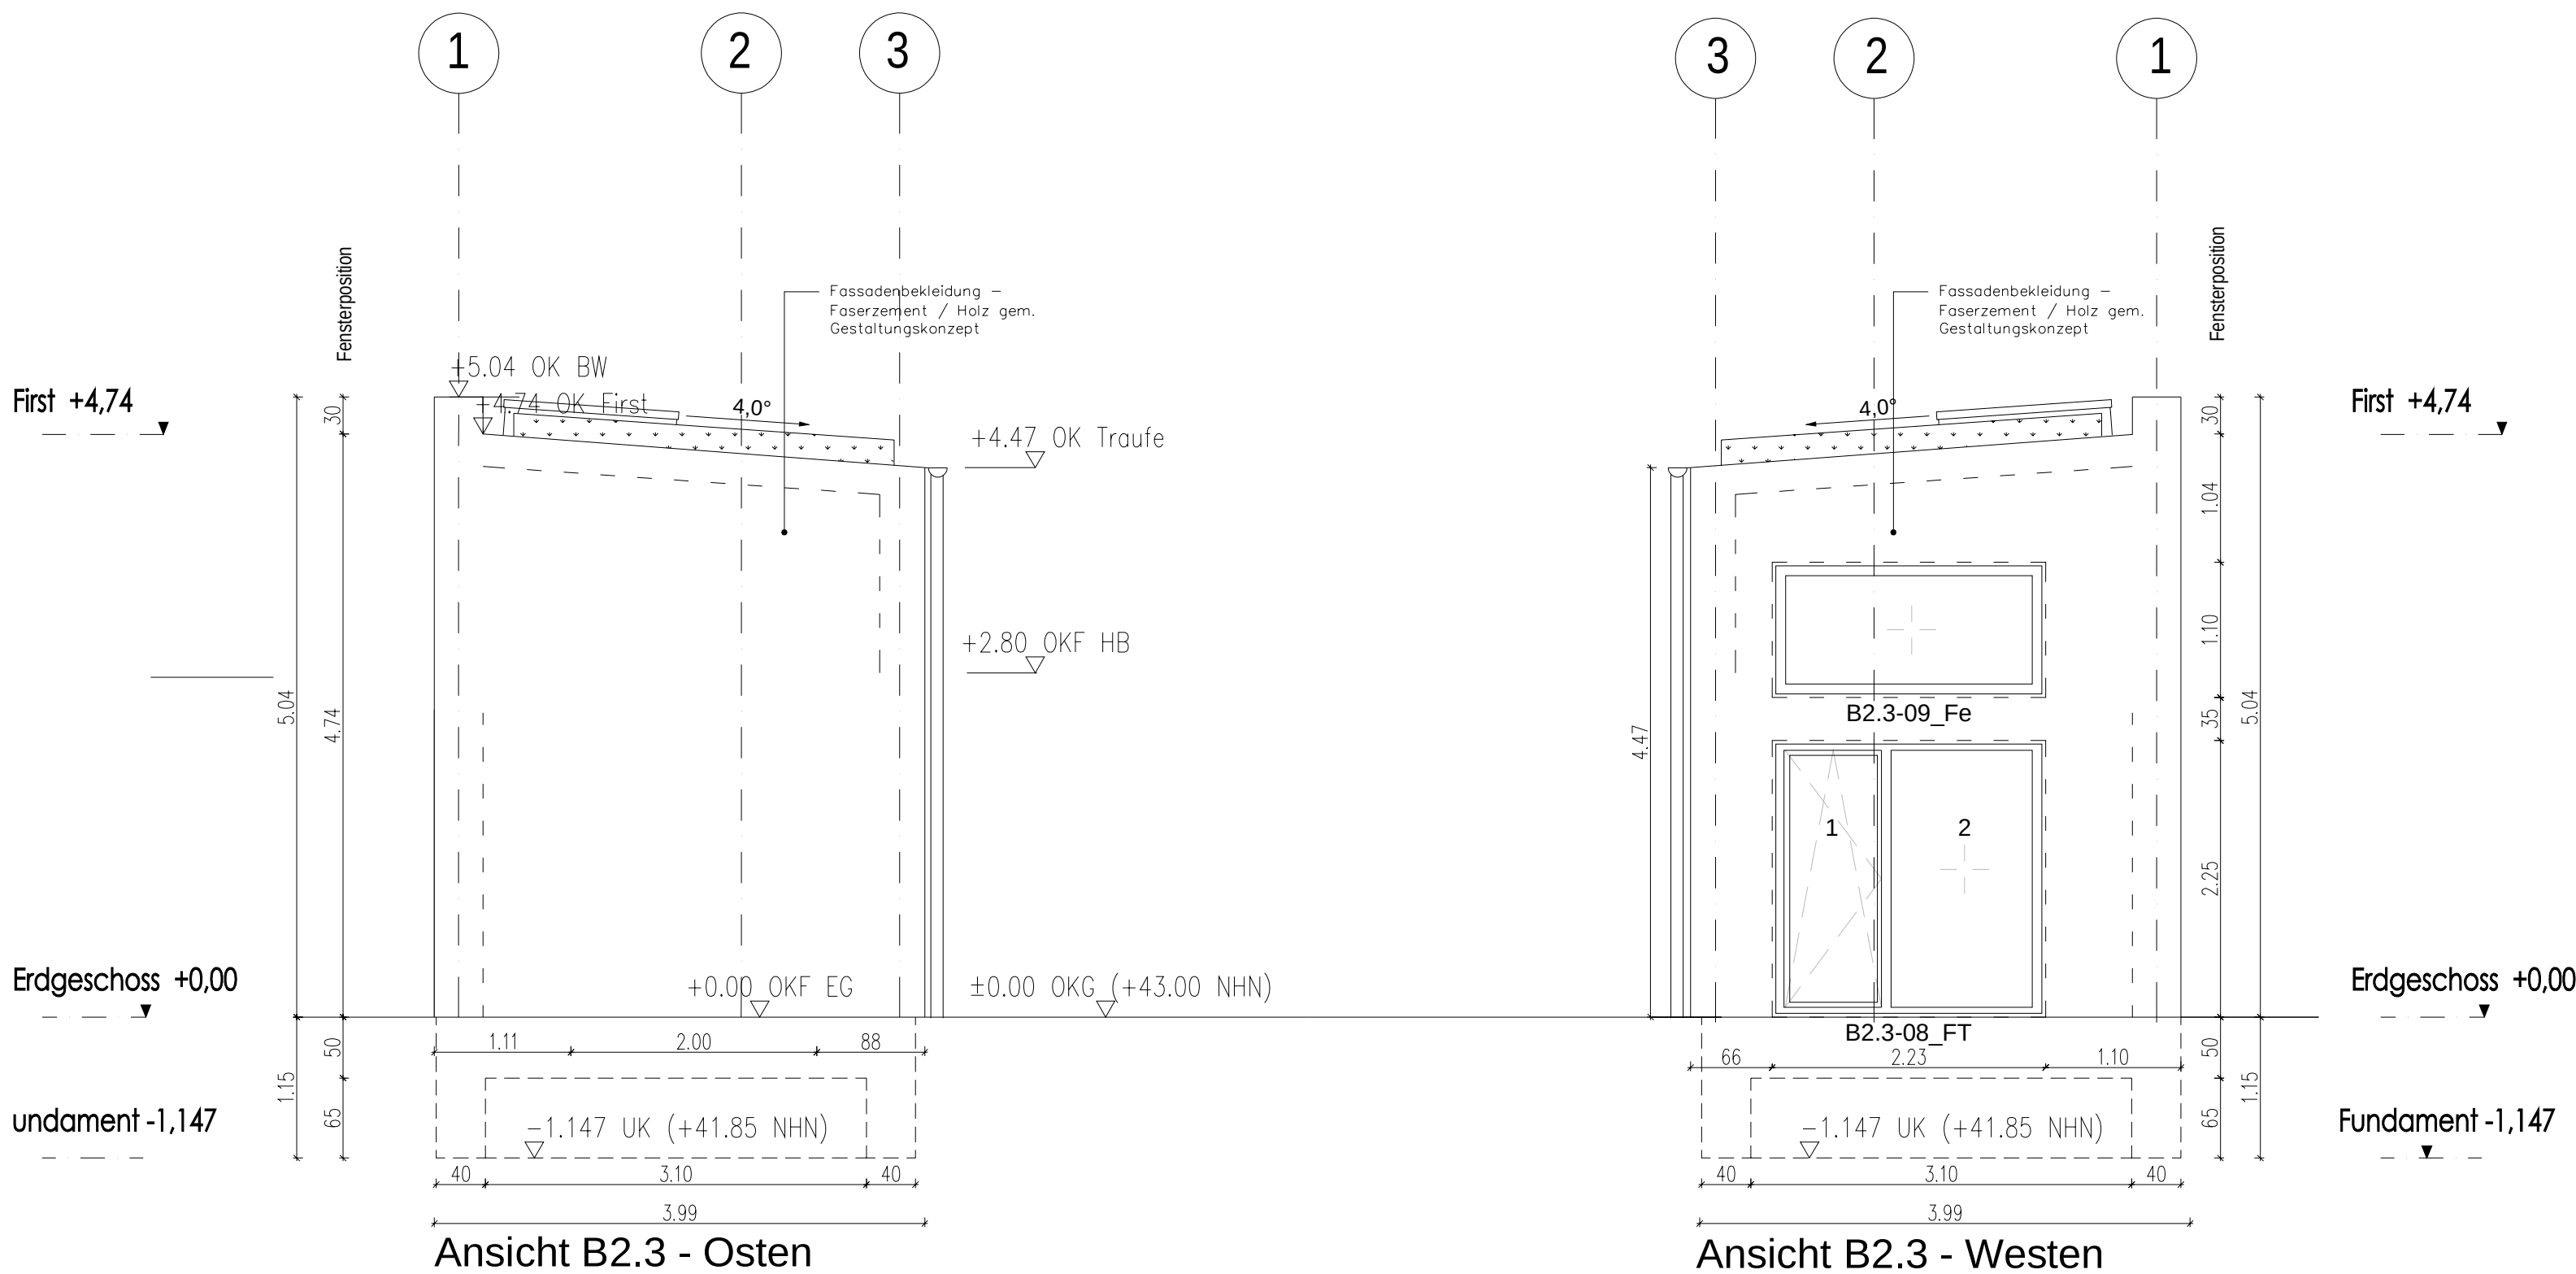

Vorabzug

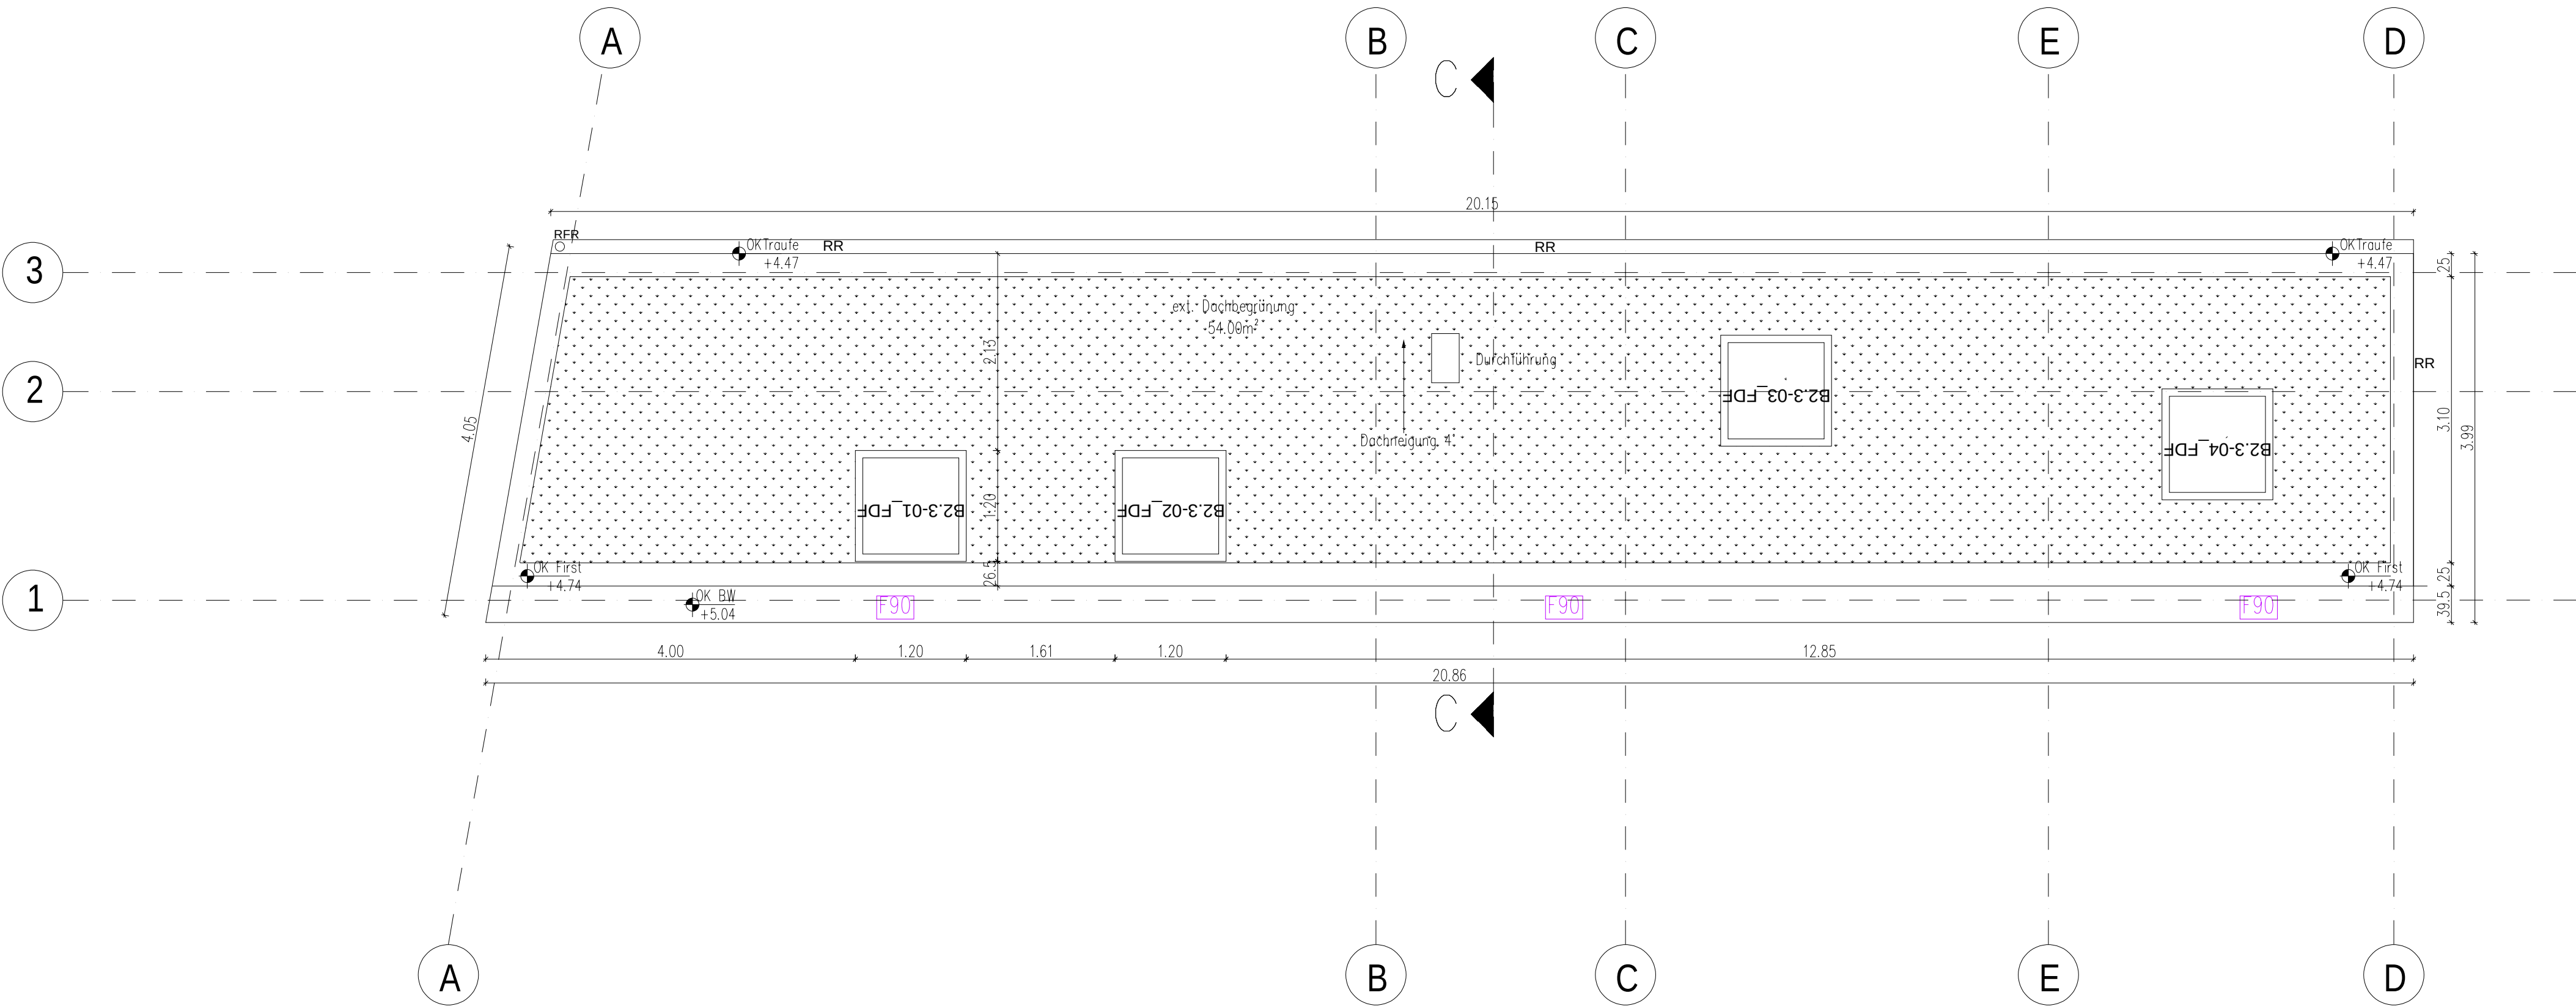

LEGENDE

AHD

abgehängte Decke

AN

Ansicht

AW

Abwasser

BDW

Badewanne

BRH

Brüstungshöhe ab OKFF

BW

Brandwand

BS

Balkenschuh

d

dichtschließend

DB

Deckenbalken

DDF

Dachdurchführung

dstür

dicht- und selbstschließend

EB

Elastisch gebetteter Balken

ELT

Elektrounterverteilung

FL

Fläche

F30

Feuerwiderstandsfähigkeit 30min (feuerhemmend)

F60

Feuerwiderstandsfähigkeit 60min (hochfeuerhemmend)

F90

Feuerwiderstandsfähigkeit 90min (feuerbeständig)

GR

Grundriss

H

Höhe

HK

Heizkörper

HKV

Heizkreisverteiler

HT

Haus Technik

IW

Installationswand

LÜ

Lüftung

OK

Oberkante

OKFFB

Oberkante Fertigfußboden

OKG

Oberkante Gelände

OL

Oberlicht

RB

Ringbalken

RFR

Regenfallrohr

rs

rauchdicht

RR

Regenrinne

RA

Rauchabzug

RH

Raumhoch

RW

Rettungsweg

SN

Schnitt

T30

Tür feuerhemmend

T30 rs

Tür feuerhemmend, rauchdicht selbstschließend

T90

Tür feuerbeständig

T90 rs

Tür feuerbeständig, rauchdicht selbstschließend

TRH

Traufhöhe

TW

Trennwand

UB

unbewehrte Frostschürze

UK

Unterkante

US

Unterschnitt

UZ

Unterzug

ÜZ

Überzug

VSS

Vorsatzschale

WE

Wohneinheit

Wfl

Wohnfläche

wmB

widerstandsfähig gegen mechanische Beanspruchung

verdeckte Element Unterzug, Sparren, usw.

Mauerwerk Bestand

Dämmung

Abriss Wand

Mauerwerk Porenbeton

Mauerwerk Kalksandstein

Trockenbau-Innenwände (innerhalb Wohneinheit), gem. Schallschutz und Brandschutz (Montage gemäß Herstellerangaben, z.B. Knauf W112 o.g.l.w.)

Außenwände in Holztafelbauweise mit Faserzementtafeln oder Holz Verkleidung gem. Schallschutz und Brandschutz

Stahlbeton

Beton

Brandschutzanforderungen

Positionsnummern, Angaben siehe Statik

Positionsnummern, Fenster / Türen

Durchbruch

HINWEIS zur PLANUNG

Dieser Plan gilt nur in Verbindung mit den Ausführungsdetails.
Für alle Ausführungs- bzw. Anschlussdetails siehe aktuellen
Detailplansatz. Fenster- und Türenlisten sind zu beachten.
Diese Planung gilt in Verbindung mit dem Ausstattungskatalog.

Die Anwendbarkeit der Detailzeichnung ist durch den
Verarbeiter vor Ort an Hand der tatsächlichen Gegebenheiten zu
Prüfen. Die Technischen Merkblätter der Hersteller und
Systemzulassungen sind zu beachten!

Alle Maße und Zeichnungsmaße sind am Bau von der
auszuführenden Firma eigenverantwortlich zu prüfen.
Der Ausführende ist verpflichtet, den Auftraggeber auf etwaige
Unstimmigkeiten der Ausführungsunterlagen hinzuweisen.
(VOB/B §3 nr.3)

HINWEIS CAD-Zeichnung

Die Erstellung der vorliegenden Planungsunterlagen (GNEISE, basiert auf
der durch CAD KON und der Schernbeck Gruppe übergebenen
CAD-Zeichnung
Höhenangaben zu den jeweiligen Hausnummern sind dem amtlichen
Lageplan zu entnehmen. Die in den Schnitten dargestellte Höhe (x)
entspricht der im Lageplan zu entnehmende Höhenkote Gelände /
OKFFBEG am Einzelaufgang.

Alle Maße sind am Bau zu prüfen!

Bauherr

Albert Immo 4 S.ä.r.l.
8d, rue Collart, 8414 Steinfort
Luxemburg

Bauvorhaben

Dachgeschoss-Neubau (Bauteil 1) und
Neubau Seitenflügel-Erweiterung (Bauteil 2.1) /
Reihenhäuser (Bauteil 2.2) / Remise (Bauteil 2.3)

Kreuzstraße 14 in 13187 Berlin, Pankow

Architekten/Ingenieure

GNEISE

Planungs- und Beratungsgesellschaft

GNEISE
Dipl.-Ing. E.-R. Frevert-Henske
Planungs- und Beratungsgesellschaft mbH

Kiehlholzstraße 176, 12437 Berlin
Tel. 030 536 01-0
Fax 030 536 01-333

Planinhalt

Ausführungsplanung

Dachaufsicht

Bauteile 2.3 - Neubau

Kreuzstraße 14 in 13187 Berlin, Pankow


C	-	-	-
B	-	-	-
A	01.03.2022	AE	SF Erweiterung, Fensterhöhen
Index	Datum	Gez	Änderung

Datum:	Maßstab:
30.11.2021	1:50
Bearbeitung:	Projektnummer:
AE	19049
Blattgröße:	Zeichnungs-nr.
850x400	KRE14_AP-19049-DA-B2.3-1.0

Plotted by Gneise Schutzvermerk nach DIN 34 beachten!

Vorabzug

Diese Zeichnung ist urheberrechtlich geschützt. Bei Weitergabe -auch auszugsweise- ist die Gneise Planungs- und Beratungsgesellschaft mbH als Urheber auf dem Plan zu vermerken!

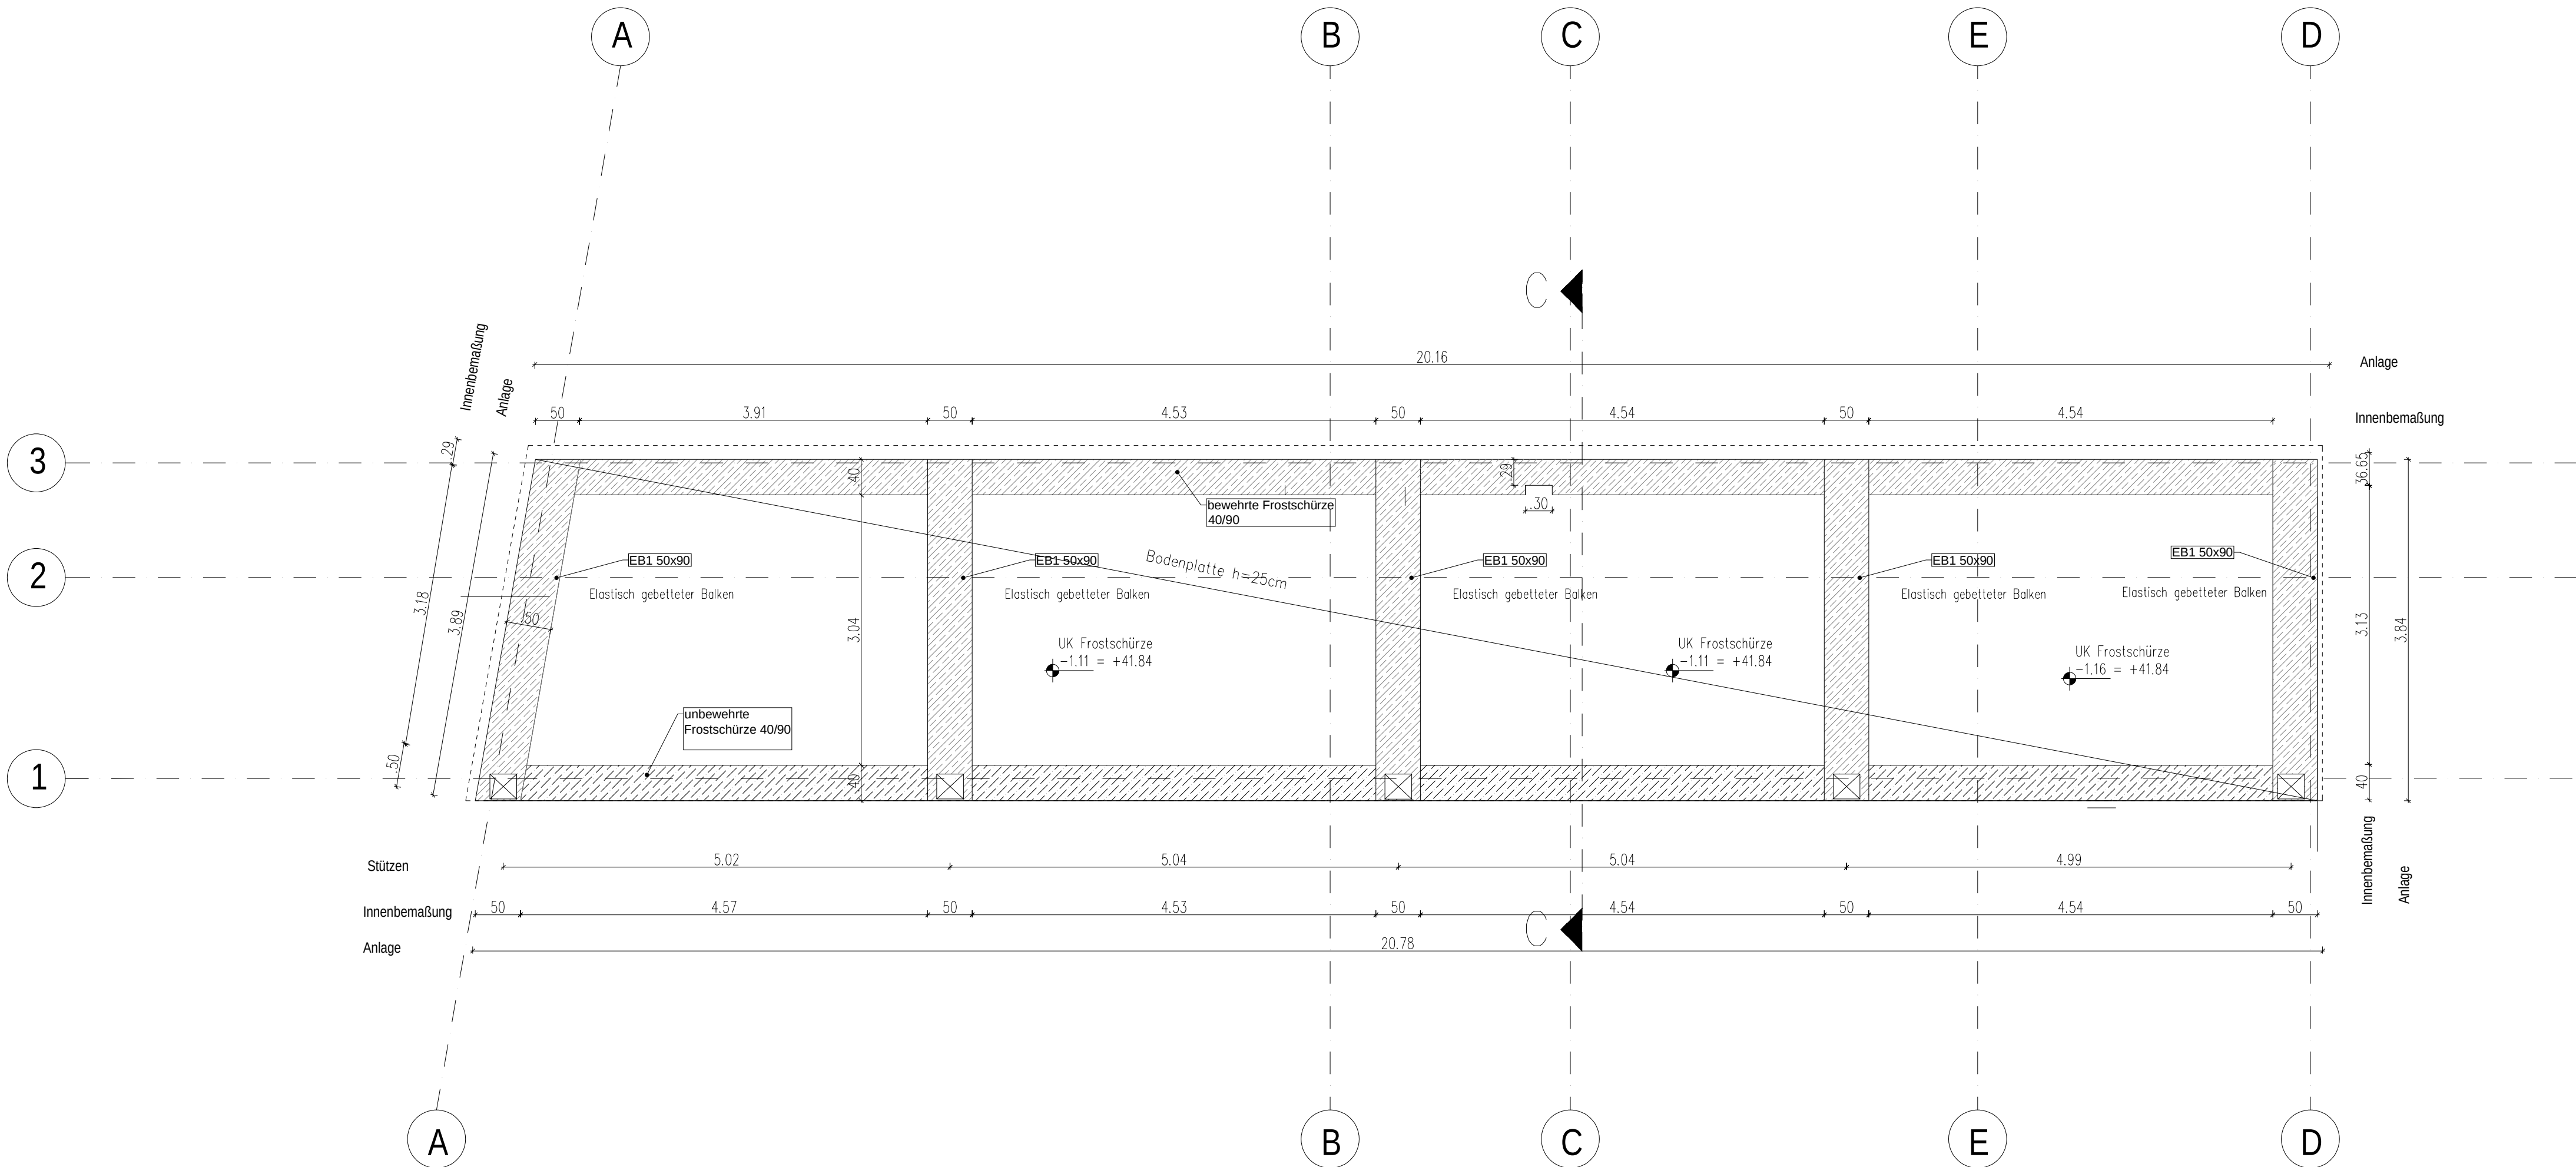

- LEGENDE**
- AHD** abgehängte Decke
AN Ansicht
AW Abwasser
BDW Badewanne
BRH Brüstungshöhe ab OKFF
BW Brandwand
BS Balkenschuh
d dichtschließend
DB Deckenbalken
DDF Dachdurchführung
dstür dicht- und selbstschließend
EB Elastisch gebetteter Balken
ELT Elektrounterverteilung
FL Fläche
F30 Feuerwiderstandsfähigkeit 30min (feuerhemmend)
F60 Feuerwiderstandsfähigkeit 60min (hochfeuerhemmend)
F90 Feuerwiderstandsfähigkeit 90min (feuerbeständig)
GR Grundriss
H Höhe
HK Heizkörper
HKV Heizkreisverteiler
HT Haustechnik
IW Installationswand
LÜ Lüftung
OK Oberkante
OKFFB Oberkante Fertigfußboden
OKG Oberkante Gelände
OL Oberlicht
RB Ringbalken
RFR Regenfallrohr
rs rauchdicht
RR Regenrinne
RA Rauchabzug
RH Raumhoch
RW Rettungsweg
SN Schnitt
T30 Tür feuerhemmend
T30 rs Tür feuerhemmend, rauchdicht selbstschließ.
T90 Tür feuerbeständig
T90 rs Tür feuerbeständig, rauchdicht selbstschließ.
TRH Traufhöhe
TW Trennwand
UB unbewehrte Frostschürze
UK Unterkante
UZ Unterschnitt
UZ Unterzug
ÜZ Überzug
VSS Vorsatzschale
WE Wohneinheit
Wfl Wohnfläche
wMB widerstandsfähig gegen mechanische Beanspruchung
- verdeckte Element Unterzug, Sparren, usw.
Mauerwerk Bestand
Dämmung
Abriss Wand
Mauerwerk Porenbeton
Mauerwerk Kalksandstein
Trockenbau-Innenwände (innerhalb Wohneinheit), gem. Schallschutz und Brandschutz (Montage gemäß Herstellerangaben, z.B. Knauf W112 o.g.w.)
Außenwände in Holztafelbauweise mit Faserzementtafeln oder Holz Verkleidung gem. Schallschutz und Brandschutz
- Stahlbeton
Beton
Brandschutzanforderungen
Positionsnummern, Angaben siehe Statik
Positionsnummern, Fenster / Türen
Durchbruch

HINWEIS zur PLANUNG

Dieser Plan gilt nur in Verbindung mit den Ausführungsdetails.
Für alle Ausführungs- bzw. Anschlussdetails siehe aktuellen Detailplansatz. Fenster- und Türenlisten sind zu beachten.
Diese Planung gilt in Verbindung mit dem Ausstattungskatalog.


Die Anwendbarkeit der Detailzeichnung ist durch den Verarbeiter vor Ort an Hand der tatsächlichen Gegebenheiten zu Prüfen. Die Technischen Merkblätter der Hersteller und Systemzulassungen sind zu beachten!

Alle Maße und Zeichnungsmaße sind am Bau von der auszuführenden Firma eigenverantwortlich zu prüfen.
Der Ausführende ist verpflichtet, den Auftraggeber auf etwaige Unstimmigkeiten der Ausführungsunterlagen hinzuweisen.
(VOB/B §3 nr.3)

HINWEIS CAD-Zeichnung

Die Erstellung der vorliegenden Planungsunterlagen (GNEISE, basiert auf der durch CAD KON und der Schernbeck Gruppe übergebenen CAD-Zeichnung.
Höhenangaben zu den jeweiligen Hausnummern sind dem amtlichen Lageplan zu entnehmen. Die in den Schnitten dargestellte Höhe (x) entspricht der im Lageplan zu entnehmende Höhenkote Gelände / OKFFBEG am Einzelaufgang.

Alle Maße sind am Bau zu prüfen!

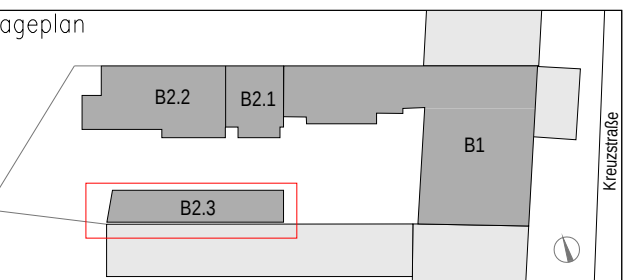

Bauherr

Albert Immo 4 S.ä.r.l.
8d, rue Collart, 8414 Steinfort
Luxemburg

Bauvorhaben

**Dachgeschoss-Neubau (Bauteil 1) und
Neubau Seitenflügel-Erweiterung (Bauteil 2.1) /
Reihenhäuser (Bauteil 2.2) / Remise (Bauteil 2.3)**

Kreuzstraße 14 in 13187 Berlin, Pankow

Architekten/Ingenieure

GNEISE
Planungs- und Beratungsgesellschaft

GNEISE
Dipl.-Ing. E.-R. Frevert-Henske
Planungs- und Beratungsgesellschaft mbH

Kiehlholzstraße 176, 12437 Berlin
Tel. 030 536 01-0
Fax 030 536 01-333

Planinhalt

Ausführungsplanung

Gründung

Bauteile 2.3 - Neubau


Kreuzstraße 14 in 13187 Berlin, Pankow

C	-	-	-
B	-	-	-
A	01.03.2022	AE	SF Erweiterung, Fensternhöhen
Index	Datum	Gez	Änderung

Datum:	Maßstab:
30.11.2021	1:50
Bearbeitung:	Projektnummer:
AE	19049
Blattgröße:	Zeichnungsnr.
850x400	KRE14_AP-19049-GR-B2.3-1.1

Plotted by Gneise Schutzvermerk nach DIN 34 beachten!

Vorabzug

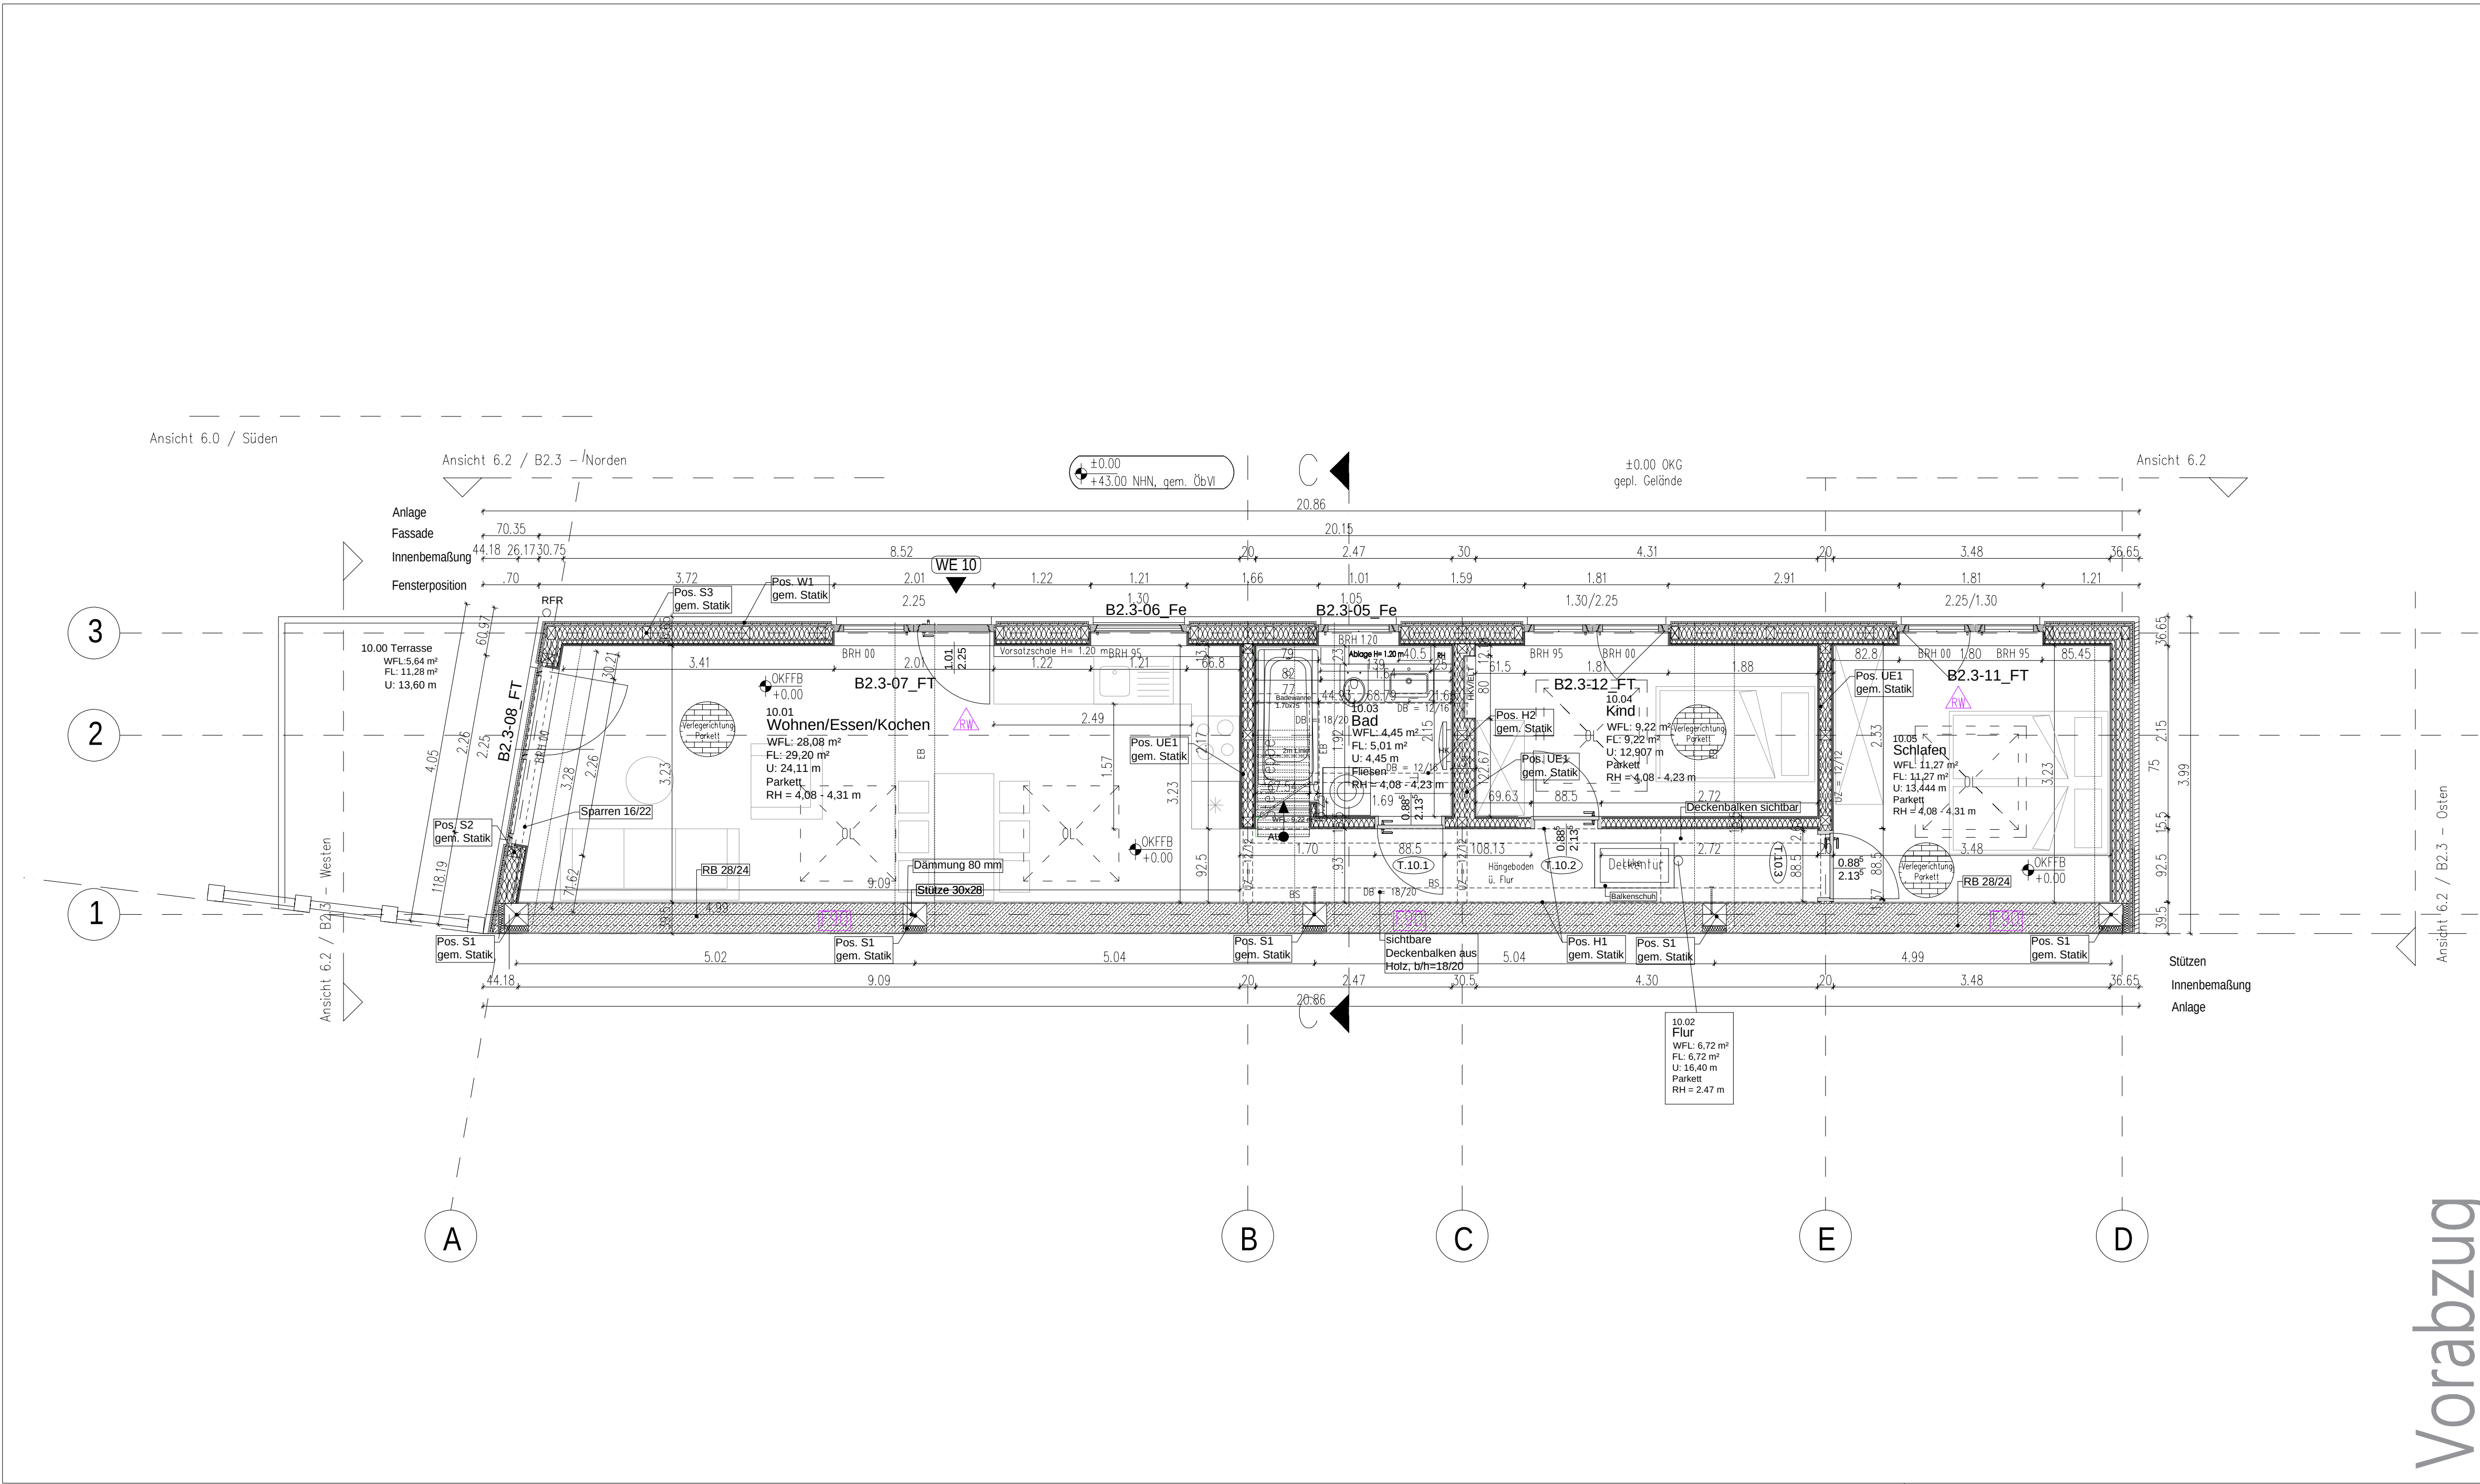

LEGENDE

- AHD** abgehängte Decke
AN Ansicht
AW Abwasser
BDW Badewanne
BRH Brüstungshöhe ab OKFF
BW Brandwand
BS Balkenschuh
d dichtschließend
DB Deckenbalken
DDF Dachdurchführung
dstür dicht- und selbstschließend
EB Elastisch gebetteter Balken
ELT Elektrounterverteilung
FL Fläche
F30 Feuerwiderstandsfähigkeit 30min (feuerhemmend)
F60 Feuerwiderstandsfähigkeit 60min (hochfeuerhemmend)
F90 Feuerwiderstandsfähigkeit 90min (feuerbeständig)
GR Grundriss
H Höhe
HK Heizkörper
HKV Heizkreisverteiler
HT Haustechnik
IW Installationswand
LÜ Lüftung
OK Oberkante
OKFFB Oberkante Fertigfußboden
OKG Oberkante Gelände
OL Oberlicht
RB Ringbalken
RFR Regenfallrohr
rs rauchdicht
RR Regenrinne
RA Rauchabzug
RH Raumhoch
RW Rettungsweg
SN Schnitt
T30 Tür feuerhemmend
T30 rs Tür feuerhemmend, rauchdicht selbstschließ.
T90 Tür feuerbeständig
T90 rs Tür feuerbeständig, rauchdicht selbstschließ.
TRH Traufhöhe
TW Trennwand
UB unbewehrte Frostschräge
UK Unterkante
US Unterschnitt
UZ Unterzug
ÜZ Überzug
VSS Vorsatzschale
WE Wohneinheit
Wfl Wohnfläche
wmB widerstandsfähig gegen mechanische Beanspruchung
verdeckte Element Unterzug, Sparren, usw.
Mauerwerk Bestand
Dämmung
Abriss Wand
Mauerwerk Porenbeton
Mauerwerk Kalksandstein
Trockenbau-Innenwände (innerhalb Wohneinheit),
gem. Schallschutz und Brandschutz (Montage
gemäß Herstellerangaben, z.B. Knauf W112 o.g.w.)
Außenwände in Holztafelbauweise mit
Faserzementtafeln oder Holz Verkleidung gem.
Schallschutz und Brandschutz
Stahlbeton
Beton
Brandschutzanforderungen
Positionennummern, Angaben siehe Statik
Positionennummern, Fenster / Türen
Durchbruch

HINWEIS zur PLANUNG

Dieser Plan gilt nur in Verbindung mit den Ausführungsdetails.
Für alle Ausführungs- bzw. Anschlussdetails siehe aktuellen
Detailplansatz. Fenster- und Türenlisten sind zu beachten.
Diese Planung gilt in Verbindung mit dem Ausstattungskatalog.


Die Anwendbarkeit der Detailzeichnung ist durch den
Verarbeiter vor Ort an Hand der tatsächlichen Gegebenheiten zu
Prüfen. Die Technischen Merkblätter der Hersteller und
Systemzulassungen sind zu beachten!

Alle Maße und Zeichnungsmaße sind am Bau von der
auszuführenden Firma eigenverantwortlich zu prüfen.
Der Ausführende ist verpflichtet, den Auftraggeber auf etwaige
Unstimmigkeiten der Ausführungsunterlagen hinzuweisen.
(VOB/B §3 nr. 3)

HINWEIS CAD-Zeichnung

Die Erstellung der vorliegenden Planungsunterlagen (GNEISE, basiert auf
der durch CAD KON und der Schernbeck Gruppe übergebenen
CAD-Zeichnung
Höhenangaben zu den jeweiligen Hausnummern sind dem amtlichen
Lageplan zu entnehmen. Die in den Schnitten dargestellte Höhe (x)
entspricht der im Lageplan zu entnehmende Höhenkote Gelände /
OKFFBEG am Einzelaufgang.

Alle Maße sind am Bau zu prüfen!

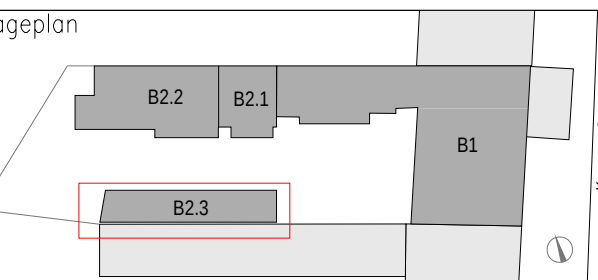

Bauherr
Albert Immo 4 S.ä.r.l.
8d, rue Collart, 8414 Steinfort
Luxemburg


Bauvorhaben
Dachgeschoss-Neubau (Bauteil 1) und
Neubau Seitenflügel-Erweiterung (Bauteil 2.1) /
Reihenhäuser (Bauteil 2.2) / Remise (Bauteil 2.3)
Kreuzstraße 14 in 13187 Berlin, Pankow

Architekten/Ingenieure
GNEISE
Planungs- und Beratungsgesellschaft
GNEISE
Dipl.-Ing. E.-R. Frevert-Henske
Planungs- und Beratungsgesellschaft mbH
Kiehlholzstraße 176, 12437 Berlin
Tel. 030 536 01-0
Fax 030 536 01-333

Planinhalt
Ausführungsplanung
Erdgeschoss
Bauteile 2.3 - Neubau
Kreuzstraße 14 in 13187 Berlin, Pankow

C	-	-	-
B	-	-	-
A	01.03.2022	AE	SF Erweiterung, Fensterhöhen
Index	Datum	Gez	Änderung

Datum:	Maßstab:
30.11.2021	1:50
Bearbeitung:	Projektnummer:
AE	19049
Blattgröße:	Zeichnungsnr.
830x297	KRE14_AP-19049-GR-B2.3-4.0
Plotted by Gneise	Schutzvermerk nach DIN 34 beachten!

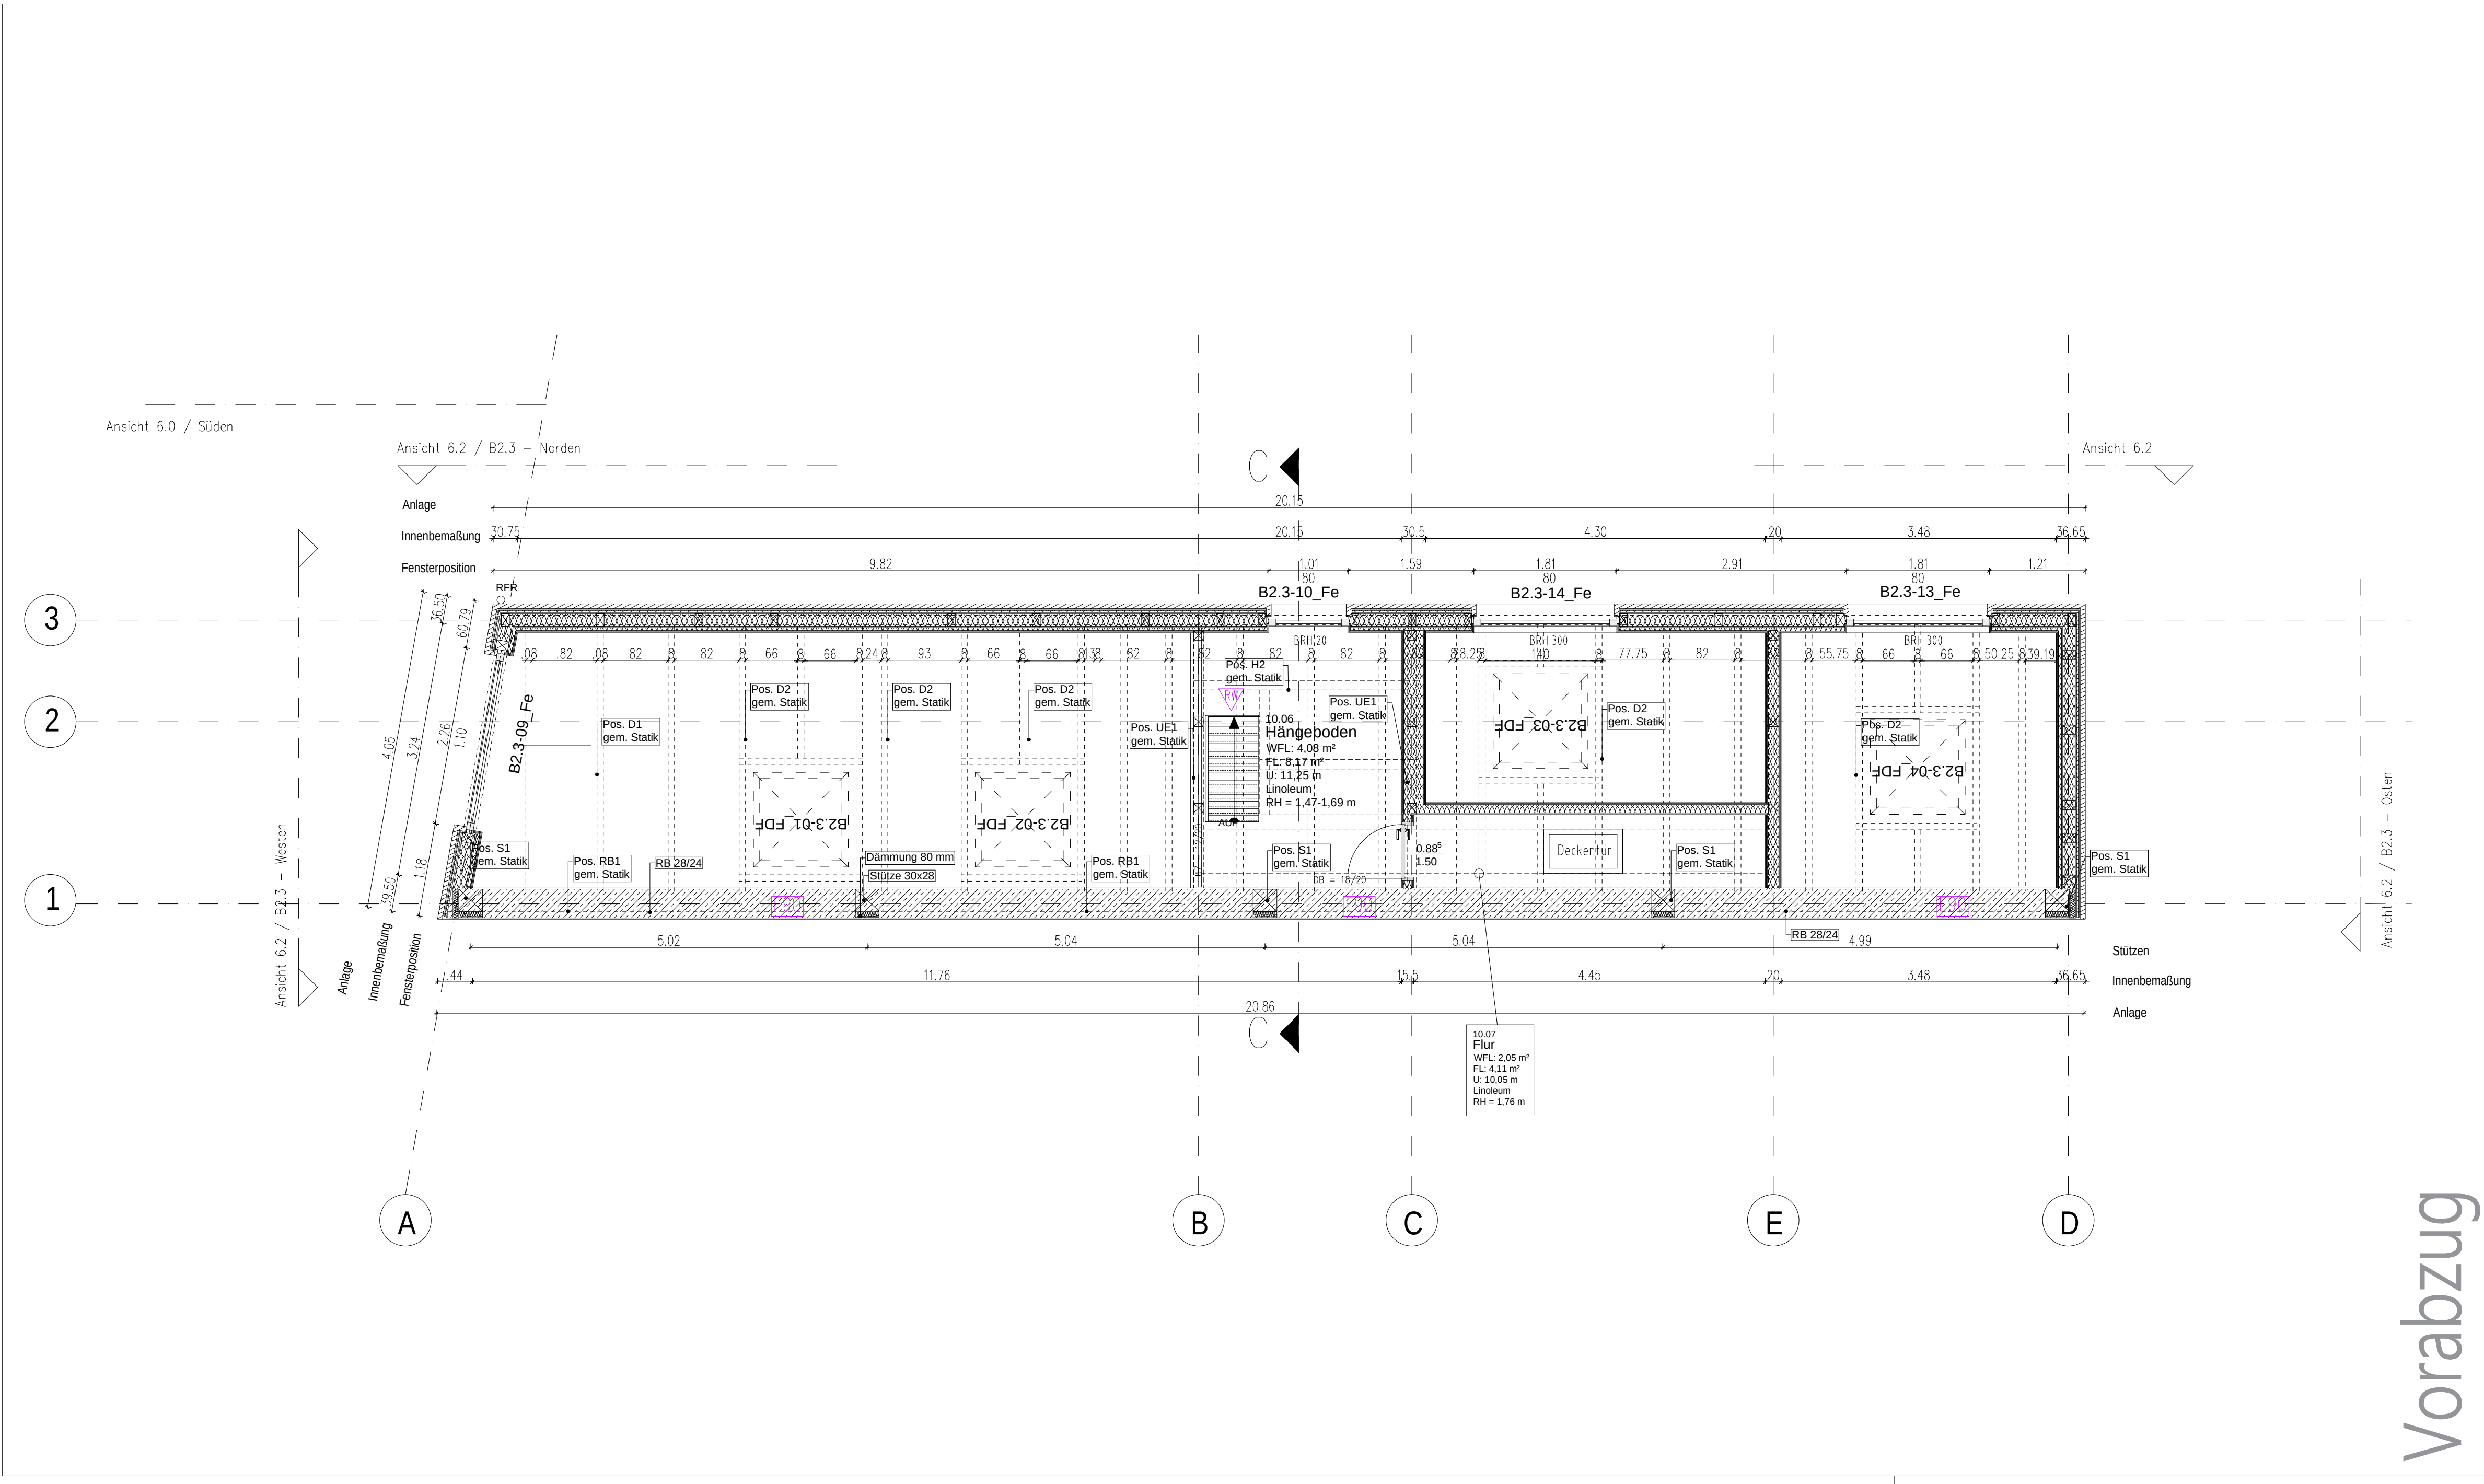

LEGENDE

AHD

abgehängte Decke

AN

Ansicht

AW

Abwasser

BDW

Badewanne

BRH

Brüstungshöhe ab OKFF

BW

Brandwand

BS

Balkenschuh

d

dichtschließend

DB

Deckenbalken

DDF

Dochdurchführung

dstür

dicht- und selbstschließend

EB

Elastisch gebetteter Balken

ELT

Elektrounterverteilung

FL

Fläche

F30

Feuerwiderstandsfähigkeit 30min (feuerhemmend)

F60

Feuerwiderstandsfähigkeit 60min (hochfeuerhemmend)

F90

Feuerwiderstandsfähigkeit 90min (feuerbeständig)

GR

Grundriss

H

Höhe

HK

Heizkörper

HKV

Heizkreisverteiler

HT

Haustechnik

IW

Installationswand

LÜ

Lüftung

OK

Oberkante

OKFFB

Oberkante Fertigfußboden

OKG

Oberkante Gelände

OL

Oberlicht

RB

Ringbalken

RFR

Regenfallrohr

rs

rauchdicht

RR

Regenrinne

RA

Rauchabzug

RH

Raumhoch

RW

Rettungsweg

SN

Schnitt

T30

Tür feuerhemmend

T30 rs

Tür feuerhemmend, rauchdicht selbstschließend

T90

Tür feuerbeständig

T90 rs

Tür feuerbeständig, rauchdicht selbstschließend

TRH

Traufhöhe

TW

Trennwand

UB

unbewehrte Frostschräge

UK

Unterkannte

US

Unterschnitt

UZ

Unterzug

ÜZ

Überzug

VSS

Vorsatzschale

WE

Wohneinheit

Wfl

Wohnfläche

wmb

widerstandsfähig gegen mechanische Beanspruchung

verdeckte Element Unterzug, Sparren, usw.

Mauerwerk Bestand

Dämmung

Abriss Wand

Mauerwerk Porenbeton

Mauerwerk Kalksandstein

Trockenbau-Innenwände (innerhalb Wohneinheit), gem. Schallschutz und Brandschutz (Montage gemäß Herstellerangaben, z.B. Knaf W112 o.g.lw.)

Außenwände in Holztafelbauweise mit Faserzementtafeln oder Holz Verkleidung gem. Schallschutz und Brandschutz

Stahlbeton

Beton

Brandschutzanforderungen

Positionennummern, Angaben siehe Statik

Positionennummern, Fenster / Türen

Durchbruch

HINWEIS zur PLANUNG

Dieser Plan gilt nur in Verbindung mit den Ausführungsdetails.
Für alle Ausführungs- bzw. Anschlussdetails siehe aktuellen Detailplansatz. Fenster- und Türenlisten sind zu beachten.
Diese Planung gilt in Verbindung mit dem Ausstattungskatalog.

Die Anwendbarkeit der Detailzeichnung ist durch den Verarbeiter vor Ort an Hand der tatsächlichen Gegebenheiten zu Prüfen. Die Technischen Merkblätter der Hersteller und Systemzulassungen sind zu beachten!

Alle Maße und Zeichnungsmaße sind am Bau von der auszuführenden Firma eigenverantwortlich zu prüfen.
Der Ausführende ist verpflichtet, den Auftraggeber auf etwaige Unstimmigkeiten der Ausführungsunterlagen hinzuweisen.
(VOB/B §3 nr. 3)

HINWEIS CAD-Zeichnung

Die Erstellung der vorliegenden Planungsunterlagen (GNEISE, basiert auf der durch CAD KON und der Scherneck Gruppe übergebenen CAD-Zeichnung.
Höhenangaben zu den jeweiligen Hausnummern sind dem amtlichen Lageplan zu entnehmen. Die in den Schnitten dargestellte Höhe (x) entspricht der im Lageplan zu entnehmende Höhenkote Gelände / OKFFBEG am Einzelaufgang.

Alle Maße sind am Bau zu prüfen!

Lageplan

Bauherr

Albert Immo 4 S.ä.r.l.
8d, rue Collart, 8414 Steinfort
Luxemburg

Bauvorhaben

Dachgeschoss-Neubau (Bauteil 1) und
Neubau Seitenflügel-Erweiterung (Bauteil 2.1) /
Reihenhäuser (Bauteil 2.2) / Remise (Bauteil 2.3)

Kreuzstraße 14 in 13187 Berlin, Pankow

Architekten/Ingenieure

GNEISE
Planungs- und Beratungsgesellschaft

GNEISE
Dipl.-Ing. E.-R. Frevert-Henske
Planungs- und Beratungsgesellschaft mbH

Kiehlholzstraße 176, 12437 Berlin
Tel. 030 536 01-0
Fax 030 536 01-333

Planinhalt

Ausführungsplanung

1. Obergeschoss

Bauteile 2.3 - Neubau

Kreuzstraße 14 in 13187 Berlin, Pankow

Index

C	-	-	-
B	-	-	-
A	01.03.2022	AE	SF Erweiterung, Fensterhöhen
Index	Datum	Gez	Änderung

Datum:

30.11.2021

Maßstab:

1:50

Bearbeitung:

AE

Projektnummer:

19049

Blattgröße:

850x400


Zeichnungs-nr.

KRE14_AP-19049-GR-B2.3-4.1

Plotted by Gneise

Schutzvermerk nach DIN 34 beachten!

Diese Zeichnung ist urheberrechtlich geschützt. Bei Weitergabe -auch auszugsweise- ist die Gneise Planungs- und Beratungsgesellschaft mbH als Urheber auf dem Plan zu vermerken!

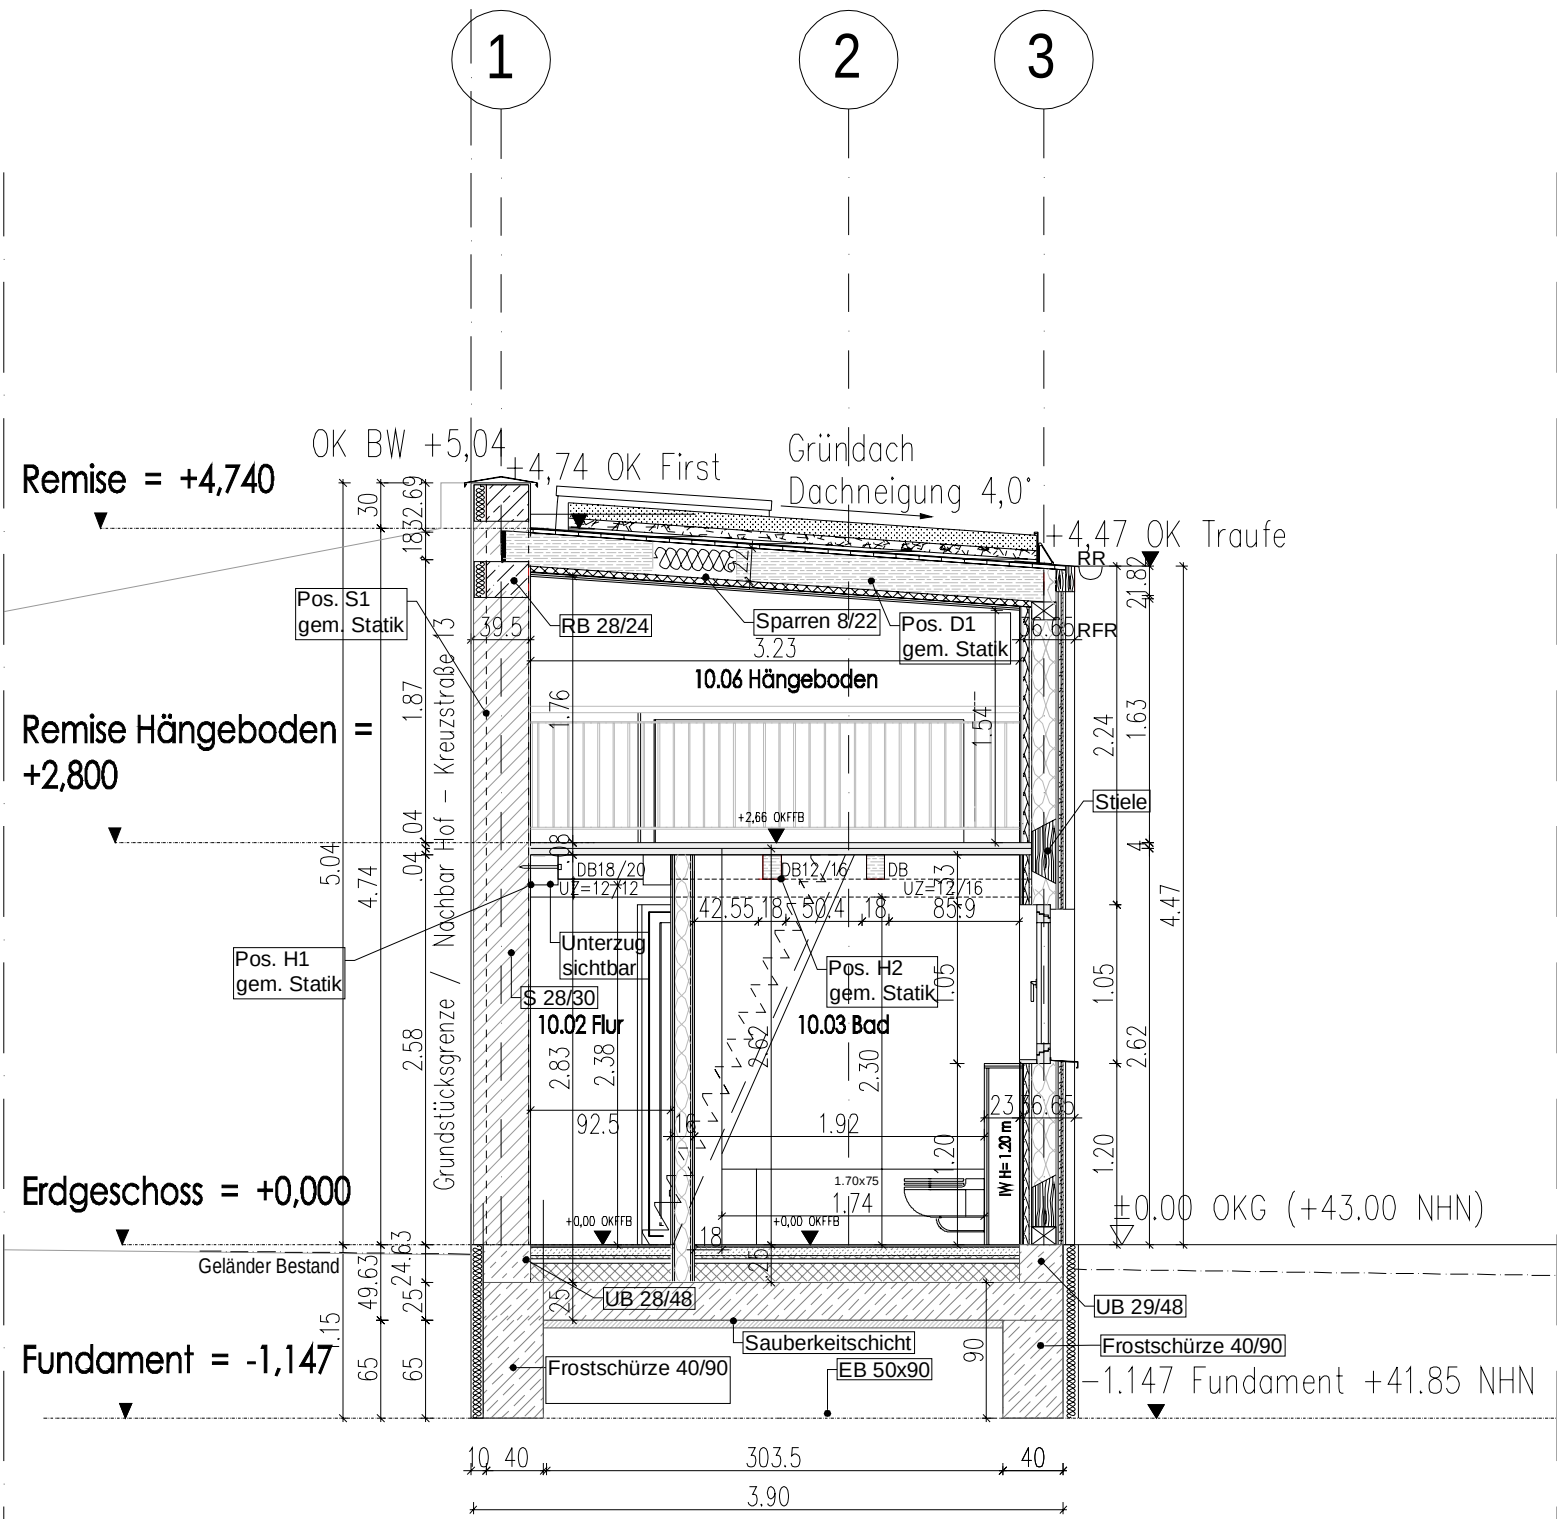

Schnitt c-c

LEGENDE

- AHD** abgehängte Decke
AN Ansicht
AW Abwasser
BDW Badewanne
BRH Brüstungshöhe ab OKFF
BW Brandwand
BS Balkenschuh
d dichtschlieend
DB Deckenbalken
DDF Dachdurchfhrung
dstr dicht- und selbstschlieend
EB Elastisch gebetteter Balken
ELT Elektrounterverteilung
FL Flche
F30 Feuerwiderstandsfhigkeit 30min (feuerhemmend)
F60 Feuerwiderstandsfhigkeit 60min (hochfeuerhemmend)
F90 Feuerwiderstandsfhigkeit 90min (feuerbestndig)
GR Grundriss
H Hhe
HK Heizkrper
HKV Heizkreisverteiler
HT Haustechnik
IW Installationswand
L Lftung
L Oberkante
OKFFB Oberkante Fertigfuboden
OKG Oberkante Gelnde
OL Oberlicht
RB Ringbalken
RFR Regenfallrohr
rs rauchdicht
RR Regenrinne
RA Rauchabzug
RH Raumhoch
RW Rettungsweg
SN Schnitt
T30 Tr feuerhemmend
T30 rs Tr feuerhemmend, rauchdicht selbstschlie.
T90 Tr feuerbestndig
T90 rs Tr feuerbestndig, rauchdicht selbstschlie.
TRH Traufhhe
TW Trennwand
UB unbewehrte Frostschrze
UK Unterkante
US Unterschnitt
UZ Unterzug
Z berzug
VSS Vorsatzschale
WE Wohneinheit
Wfl Wohnflche
wmb widerstandsfhig gegen mechanische Beanspruchung
- verdeckte Element Unterzug, Sparren, usw.**
Mauerwerk Bestand
Dmmung
Abriss Wand
Mauerwerk Porenbeton
Mauerwerk Kalksandstein
Trockenbau-Innenwnde (innerhalb Wohneinheit), gem. Schallschutz und Brandschutz (Montage gem Herstellerangaben, z.B. Knauf W112 o.glw.)
Auenwnde in Holztafelbauweise mit Faserzementtafen oder Holz Verkleidung gem. Schallschutz und Brandschutz
Stahlbeton
Beton
T30dts Brandschutzanforderungen
Pos 01-1 Positionsnummern, Angaben siehe Statik
B2-1-B2-10 Positionsnummern, Fenster / Tren
Durchbruch

HINWEIS zur PLANUNG

Dieser Plan gilt nur in Verbindung mit den Ausfhrungsdetails.
Fr alle Ausfhrungs- bzw. Anschlussdetails siehe aktuellen
Detailplansatz Fenster- und Trenlisten sind zu beachten.
Diese Planung gilt in Verbindung mit dem Ausstattungskatalog.


Die Anwendbarkeit der Detailzeichnung ist durch den
Verarbeiter vor Ort an Hand der tatschlichen Gegebenheiten zu
Prfen. Die Technischen Merkbltter der Hersteller und
Systemzulassungen sind zu beachten!

Alle Mae und Zeichnungsmae sind am Bau von der
auszufhrenden Firma eigenverantwortlich zu prfen.
Der Ausfhrende ist verpflichtet, den Auftraggeber auf etwaige
Unstimmigkeiten der Ausfhrungsunterlagen hinzuweisen.
(VOB/B §3 nr.3)

HINWEIS CAD-Zeichnung

Die Erstellung der vorliegenden Planungsunterlage GNEISE, basiert auf
der durch CAD KON und der Schernbeck Gruppe bergebenen
CAD-Zeichnung.
Hohenangaben zu den jeweiligen Hausnummern sind dem amtlichen
Lageplan zu entnehmen. Die in den Schnitten dargestellte Hhe (x)
entspricht der im Lageplan zu entnehmende Hhenkote Gelnde /
OK.FFB.EG am Einzelaufgang.

Alle Mae sind am Bau zu prfen!

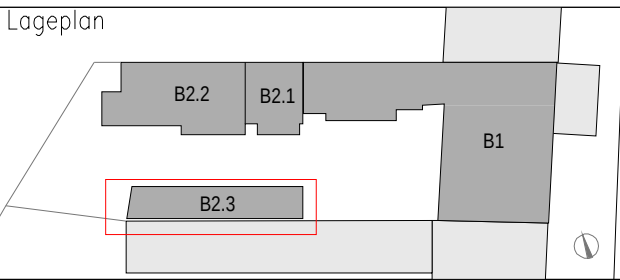

Bauherr

Albert Immo 4 S.r.l.
8d, rue Collart, 8414 Steinfort
Luxemburg

Bauvorhaben
**Dachgeschoss-Neubau (Bauteil 1) und
Neubau Seitenflgel-Erweiterung (Bauteil 2.1) /
Reihenhuser (Bauteil 2.2) / Remise (Bauteil 2.3)**

Kreuzstrae 14 in 13187 Berlin, Pankow

Architekten/Ingenieure
GNEISE
Planungs- und Beratungsgesellschaft

GNEISE
Dipl.-Ing. E.-R. Frevert-Henske
Planungs- und Beratungsgesellschaft mbH
Kieffholzstrae 176, 12437 Berlin
Tel. 030 536 01-0
Fax 030 536 01-333

Planinhalt
Ausfhrungsplanung
Schnitt C-C
Bauteile 2.3 - Neubau
Kreuzstrae 14 in 13187 Berlin, Pankow

C	-	-	-
B	-	-	-
A	01.03.2022	AE	SF Erweiterung, Fensterhhen
Index	Datum	Gez	nderung

Datum: 30.11.2021	Mastab: 1:50
Bearbeitung: AE	Projektnummer: 19049
Blattgre: 830x297	Zeichnungsnr. KRE14_AP-19049-SN-B2.3-5.0

Plotted by Gneise Schutzvermerk nach DIN 34 beachten !